




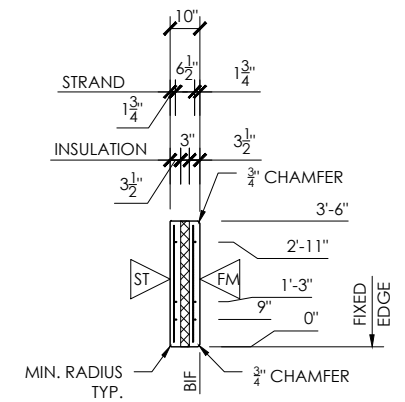

DIAGONAL = $45'-0\frac{5}{8}"$

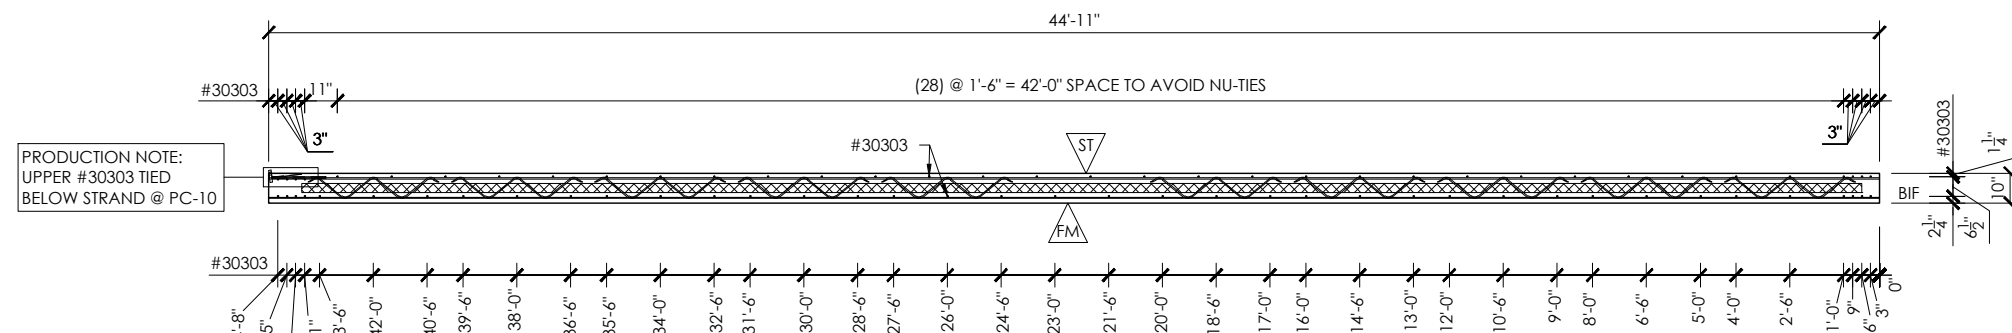

SYMBOLS
 S.I.F. = SIDE IN FORM
 B.I.F. = BOTTOM IN FORM
 T.I.F. = TOP IN FORM
 = STEEL TROWEL
 = FORM FINISH

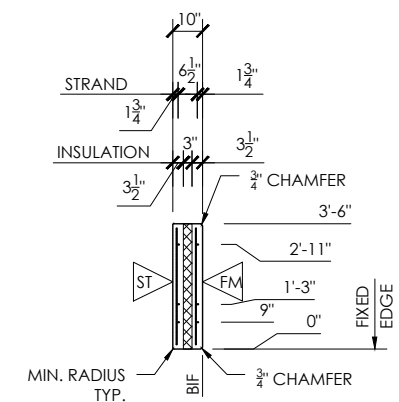

FOAM DRAWING

NOTES:
1. ALL REBAR IS TO BE 1" CLR. UNO
2. ALL DIMENSIONS ARE TO CENTERLINE UNO

SYMBOLS
S.I.F. = SIDE IN FORM
B.I.F. = BOTTOM IN FORM
T.I.F. = TOP IN FORM



REL.	DESCRIPTION	DATE	BY
1	FOR PRODUCTION	9/20/2021	BM

DRAWN: OSJ CHECKED: BM ENGR: LMB PLOTTED: 09/14/2021

NORTHEAST PRECAST

92 REESE ROAD
MILLVILLE, NJ 08332
OFFICE: 866-699-2557 FAX: 856-765-9087
www.northeastprecast.com

PROJECT: HRP HUDSON BUILDING 1		
JOB NO. 20-NE0881	PIECE MARK W004	SHEET NO. 2 of 3

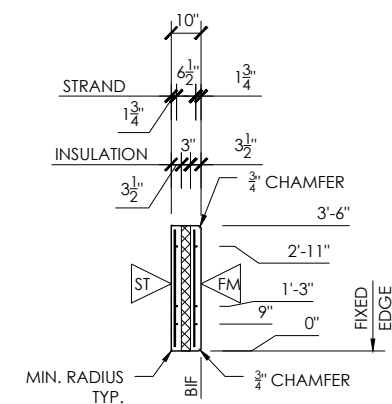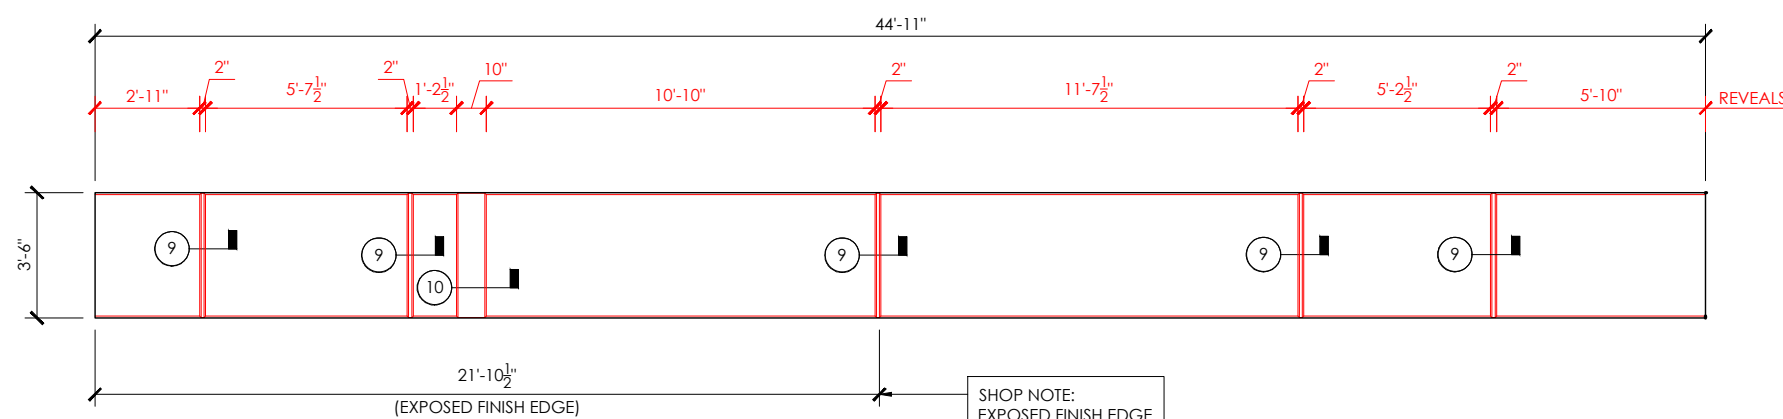

NOTES:
1. ALL REBAR IS TO BE 1" CLR. UNO
2. ALL DIMENSIONS ARE TO CENTERLINE UNO
SYMBOLS
S.I.F. = SIDE IN FORM
B.I.F. = BOTTOM IN FORM
T.I.F. = TOP IN FORM

REL.	DESCRIPTION	DATE	BY
1	FOR PRODUCTION	9/20/2021	BM

DRAWN: OSJ	CHECKED: BM	ENGR: LMB	PLOTTED: 09/14/2021
---------------	----------------	--------------	------------------------