



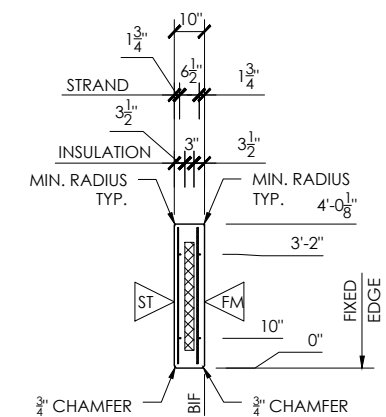

SECTION VIEW

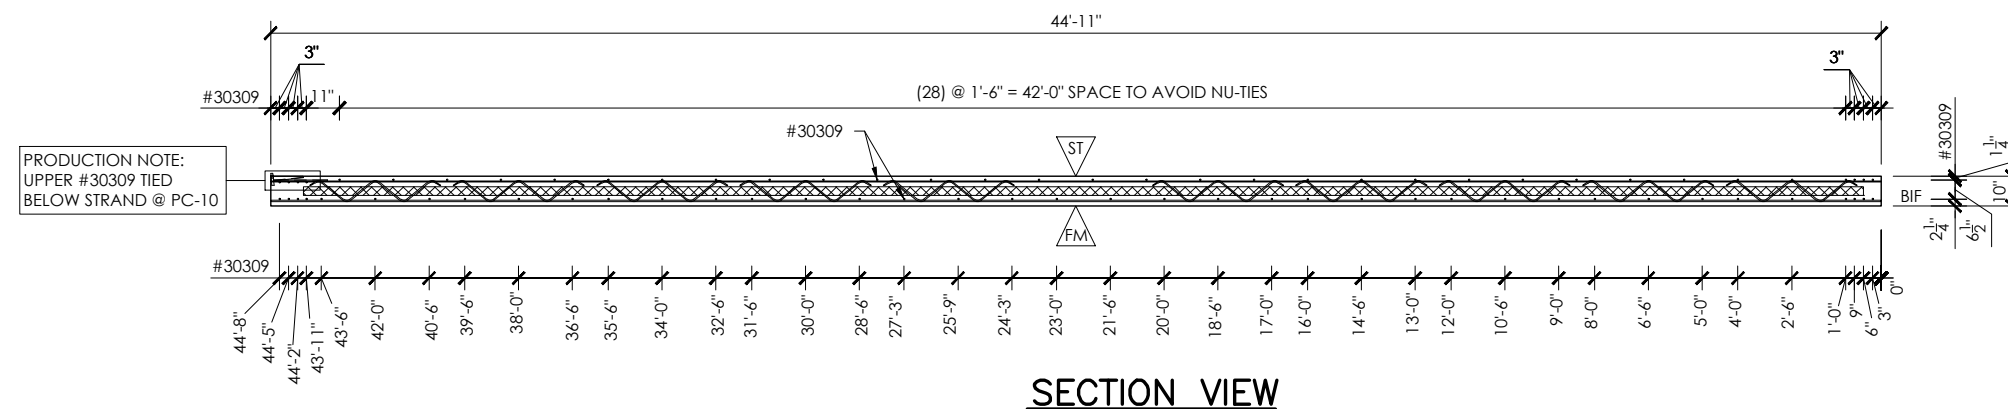

NOTES:
1. ALL REBAR IS TO BE 1" CLR. UNO
2. ALL DIMENSIONS ARE TO CENTERLINE UNO

SYMBOLS
S.I.F. = SIDE IN FORM
B.I.F. = BOTTOM IN FORM
T.I.F. = TOP IN FORM
 **= STEEL TROWEL**
 **= FORM FINISH**

CI-63	3/4" DIA. x 3 1/2" CI-6334312P COIL INSERT	1	EA
NU-TIE	7" NU-TIE	30	EA
PC-10	PL 3/4" x 4" x 0'-7" w/ (2) #4 X 1'-6" BAR & STEEL CHANNEL	2	EA
P003	PL 3/8" x 6" x 0'-6" w/ (4) 1/2" DIA. x 2 5/8" HCA	18	EA
P004	PL 3/8" x 8" x 1'-0" w/ (6) 1/2" DIA. x 2 5/8" HCA	2	EA
QLFIP1217G	12T SAND PANEL ANCHOR	6	EA
MARK	DESCRIPTION	QTY.	UOM

#30309	#3 REBAR X 3'-9" LONG	75	EA
#3BB08	#3 BENT BAR X 3'-3" LONG	9	EA
#6BB01	#6 BENT BAR X 4'-6" LONG	12	EA
#70006	#7 REBAR X 0'-6" LONG	12	EA
1/2 STRAND	1/2 DIAMETER STRAND X 44'-11" LONG 30.9 KIPS	4	EA
MARK		QTY.	UOM

MARK	DESCRIPTION		

CONCRETE MIX		
MIX	CY	B/F
NEP-SP	2.40	B
NEP-15	1.94	F

f'c (28 DAYS)	6,000 PSI
f'c (SHIPPING)	4,000 PSI
f'c (RELEASE)	3,500 PSI

PIECES REQ'D:
1

WEIGHT:
17600 LB

DESIGN:
IWP1.00

PC. FOUND ON
E-DRAWING:
E-3.01

REL.	DESCRIPTION	DATE	BY
1	FOR PRODUCTION	9/20/2021	BM

DRAWN: OSJ CHECKED: BM ENGR: LMB PLOTTED: 09/14/2021

**NORTHEAST
PRECAST**

92 REESE ROAD
MILLVILLE, NJ 08532
OFFICE: 866-699-2557 FAX: 866-765-9087
www.northeastprecast.com

PROJECT: HRP HUDSON BUILDING 1		
JOB NO. 20-NE0881	PIECE MARK W008	SHEET NO. 1 of 3



NOTES:
1. ALL REBAR IS TO BE 1" CLR. UNO
2. ALL DIMENSIONS ARE TO CENTERLINE UNO
SYMBOLS
S.I.F. = SIDE IN FORM
B.I.F. = BOTTOM IN FORM
T.I.F. = TOP IN FORM

REL.	DESCRIPTION	DATE	BY
1	FOR PRODUCTION	9/20/2021	BM

DRAWN: OSJ	CHECKED: BM	ENGINE: LMB	PLOTTED: 09/14/2021
---------------	----------------	----------------	------------------------

NORTHEAST PRECAST

92 REESE ROAD
MILLVILLE, NJ 08332



OFFICE: 866-699-2557 FAX: 856-765-9087

www.northeastprecast.com

PROJECT:

HRP HUDSON BUILDING 1

JOB NO. 20-NE0881	PIECE MARK W008	SHEET NO. 2 of 3
----------------------	--	---------------------

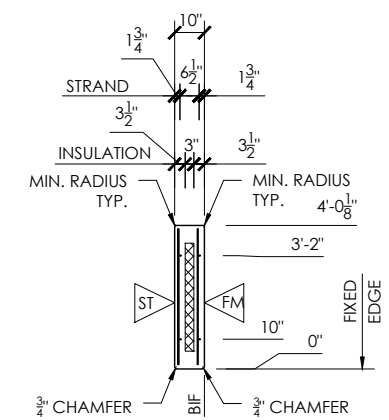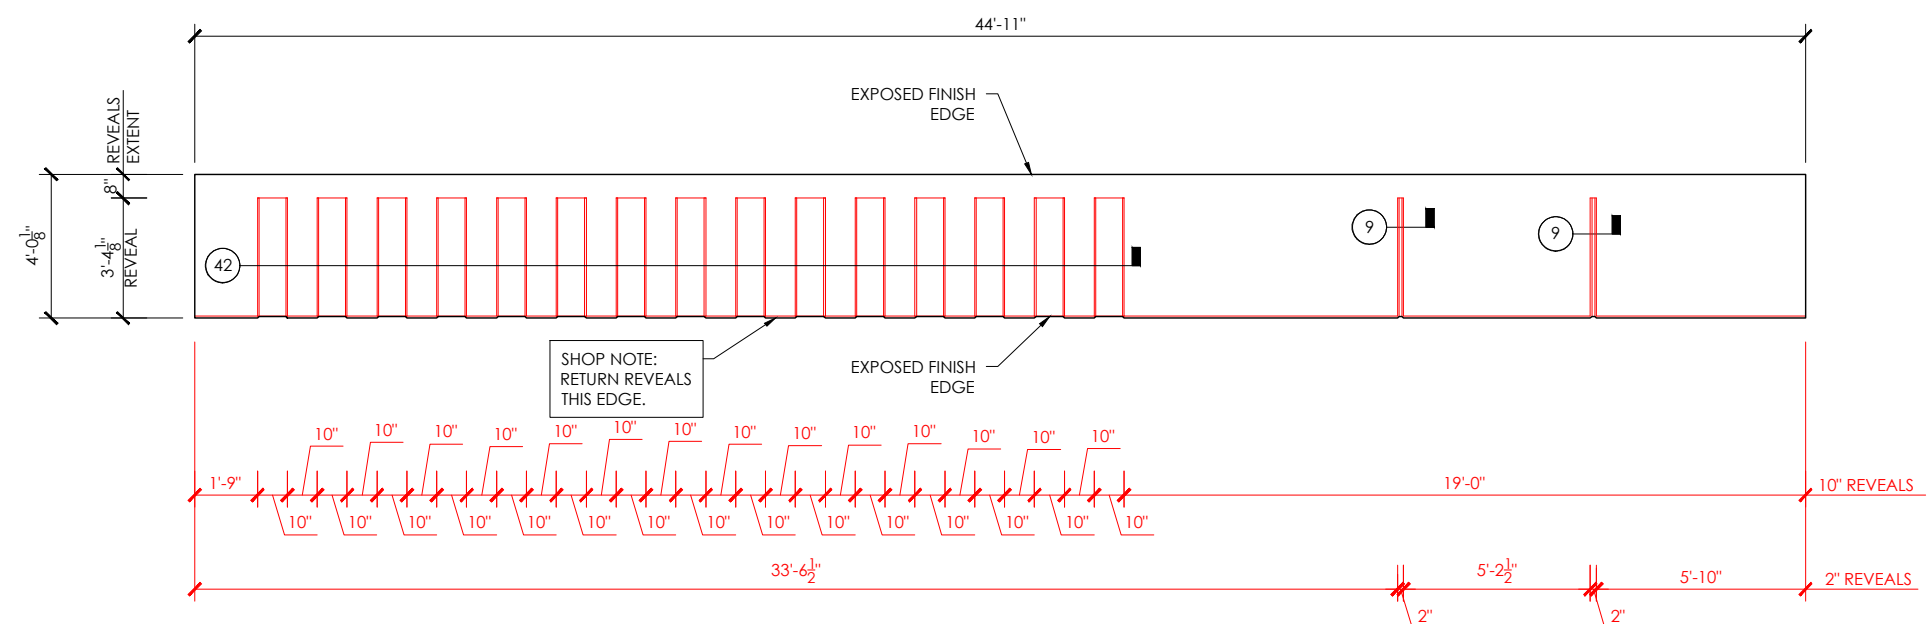

SECTION VIEW

NOTES:
1. ALL REBAR IS TO BE 1" CLR. UNO
2. ALL DIMENSIONS ARE TO CENTERLINE UNO
SYMBOLS
S.I.F. = SIDE IN FORM
B.I.F. = BOTTOM IN FORM
T.I.F. = TOP IN FORM

REL.	DESCRIPTION	DATE	BY
1	FOR PRODUCTION	9/20/2021	BM

DRAWN: OSJ	CHECKED: BM	ENGR: LMB	PLOTTED: 09/14/2021
---------------	----------------	--------------	------------------------

NORTHEAST
PRECAST

92 REESE ROAD
MILLVILLE, NJ 08332
OFFICE: 866-699-2557 FAX: 856-765-9087
www.northeastprecast.com

PROJECT: HRP HUDSON BUILDING 1		
JOB NO. 20-NE0881	PIECE MARK W008	SHEET NO. 3 of 3