



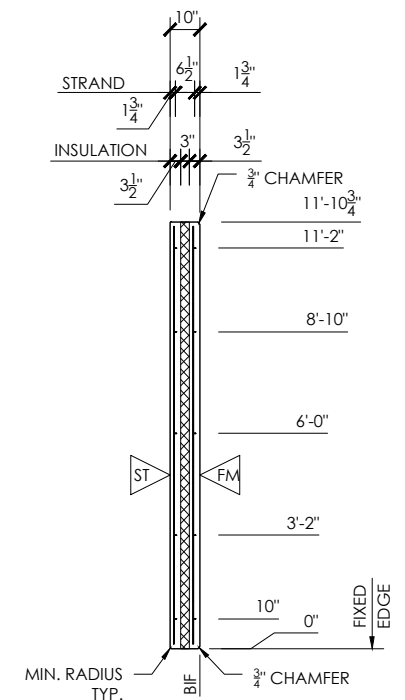

SECTION VIEW

FORM VIEW

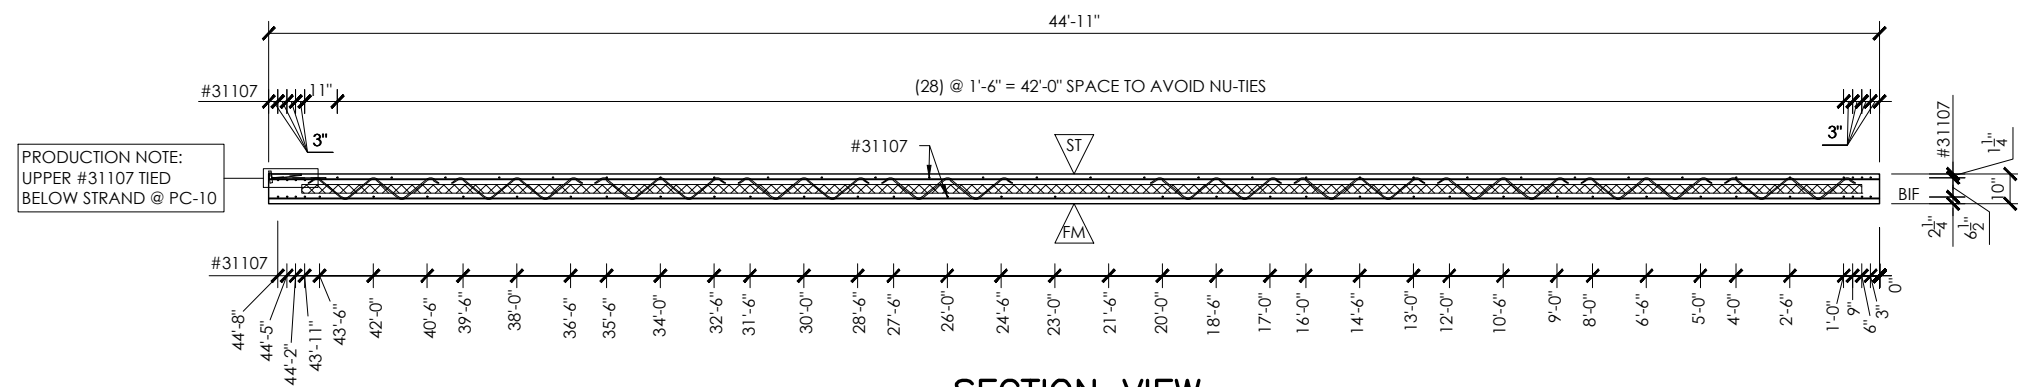

SECTION VIEW

DIAGONAL = $46' - 5\frac{9}{16}"$

NOTES:
1. ALL REBAR IS TO BE 1" CLR. UNO
2. ALL DIMENSIONS ARE TO CENTERLINE UNO

SYMBOLS
S.I.F. = SIDE IN FORM
B.I.F. = BOTTOM IN FORM
T.I.F. = TOP IN FORM
 = STEEL TROWEL
 = FORM FINISH




A/B: (10) PIECES @ 4'-0" X 3'-10 $\frac{1}{2}$ "
C/D: (10) PIECES @ 4'-0" X 8'-0"
E: (1) PIECE @ 3'-6" X 3'-10 $\frac{1}{2}$ "
F (1) PIECE @ 3'-6" X 8'-0"


- NOTES:**
1. ALL REBAR IS TO BE 1" CLR. UNO
2. ALL DIMENSIONS ARE TO CENTERLINE UNO
- SYMBOLS**
S.I.F. = SIDE IN FORM
B.I.F. = BOTTOM IN FORM
T.I.F. = TOP IN FORM

REL.	DESCRIPTION	DATE	BY
1	FOR PRODUCTION	9/15/2021	BM

DRAWN: OSJ	CHECKED: BM	ENGR: LMB	PLOTTED: 09/06/2021
---------------	----------------	--------------	------------------------

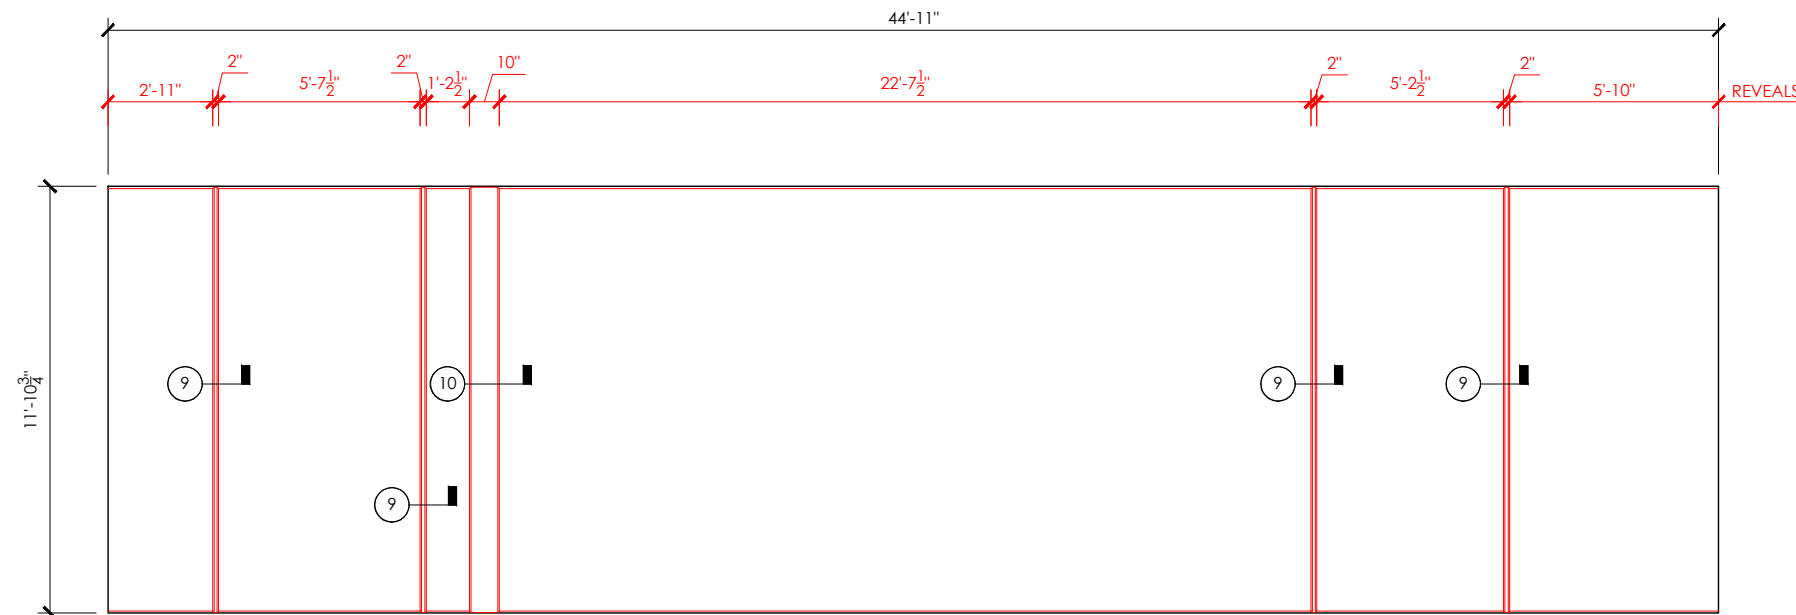

REVEAL DRAWING

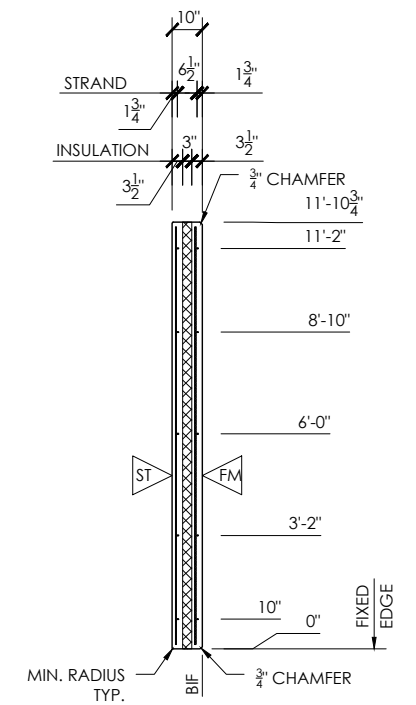

SECTION VIEW

NOTES:
1. ALL REBAR IS TO BE 1" CLR. UNO
2. ALL DIMENSIONS ARE TO CENTERLINE UNO
SYMBOLS
S.I.F. = SIDE IN FORM
B.I.F. = BOTTOM IN FORM
T.I.F. = TOP IN FORM

REL.	DESCRIPTION	DATE	BY
1	FOR PRODUCTION	9/15/2021	BM

DRAWN: OSJ	CHECKED: BM	ENGR: LMB	PLOTTED: 09/06/2021
---------------	----------------	--------------	------------------------

NORTHEAST PRECAST

92 REESE ROAD
MILLVILLE, NJ 08332
OFFICE: 866-699-2557 FAX: 856-765-9087
www.northeastprecast.com

PROJECT: HRP HUDSON BUILDING 1		
JOB NO. 20-NE0881	PIECE MARK W009	SHEET NO. 3 of 3