



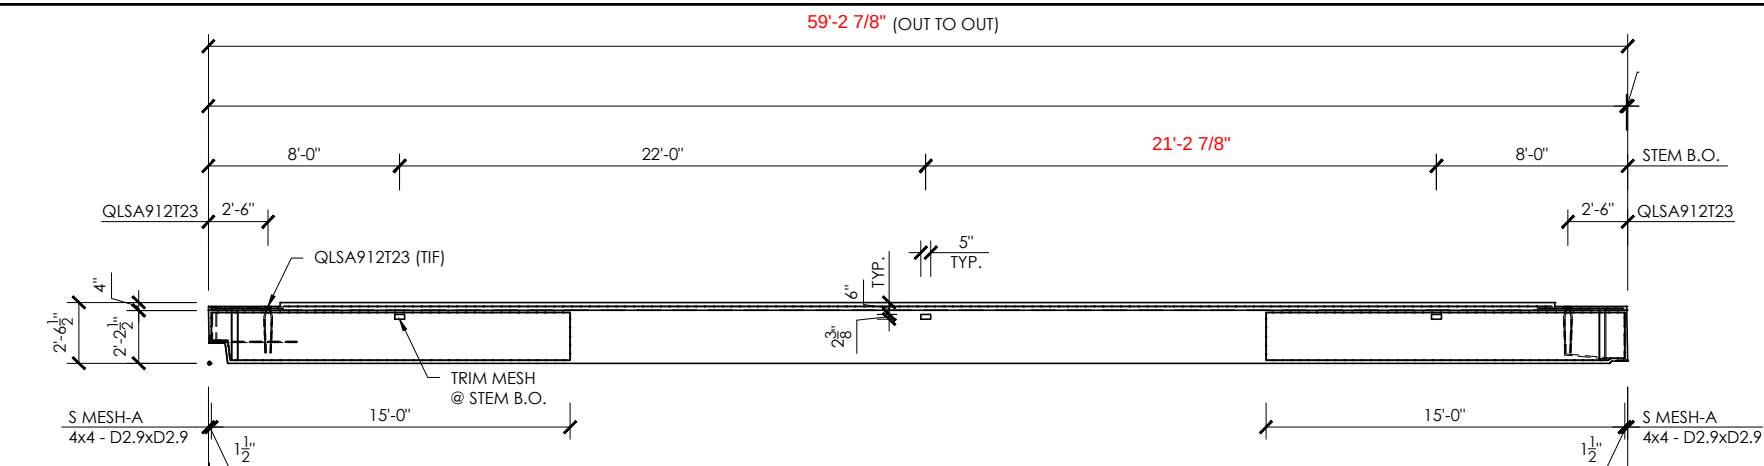


STEM S1
DETAIL B

STEM S2
DETAIL C

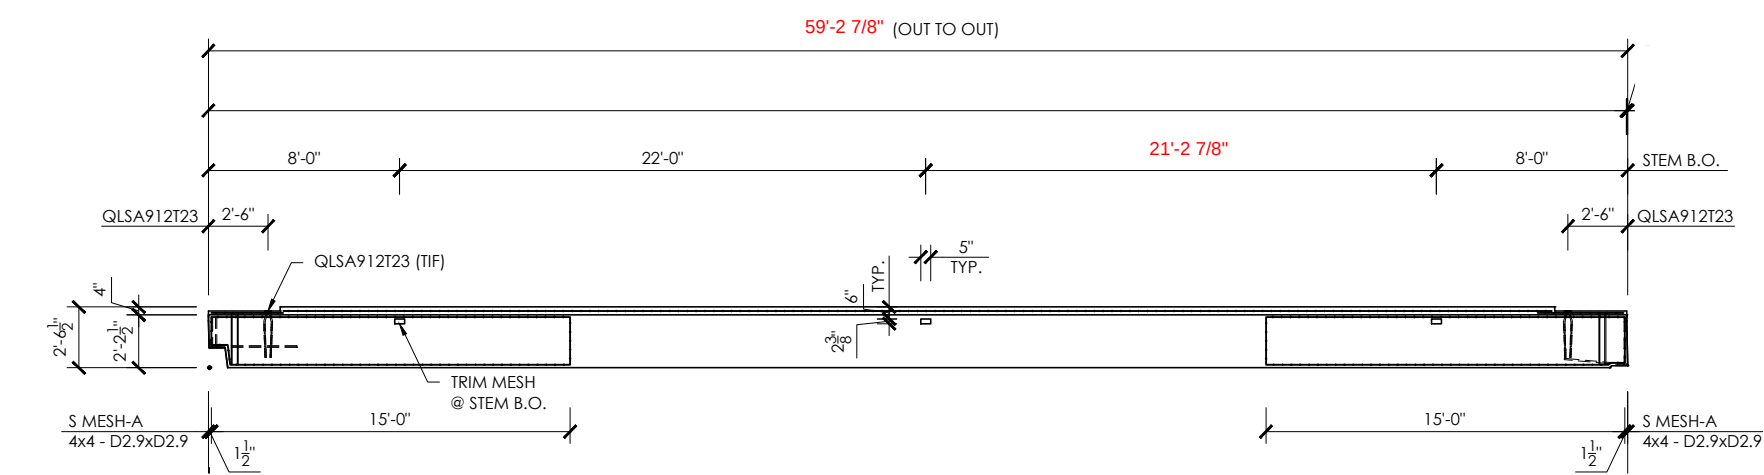


STEM S3
DETAIL B

STEM S4
DETAIL C

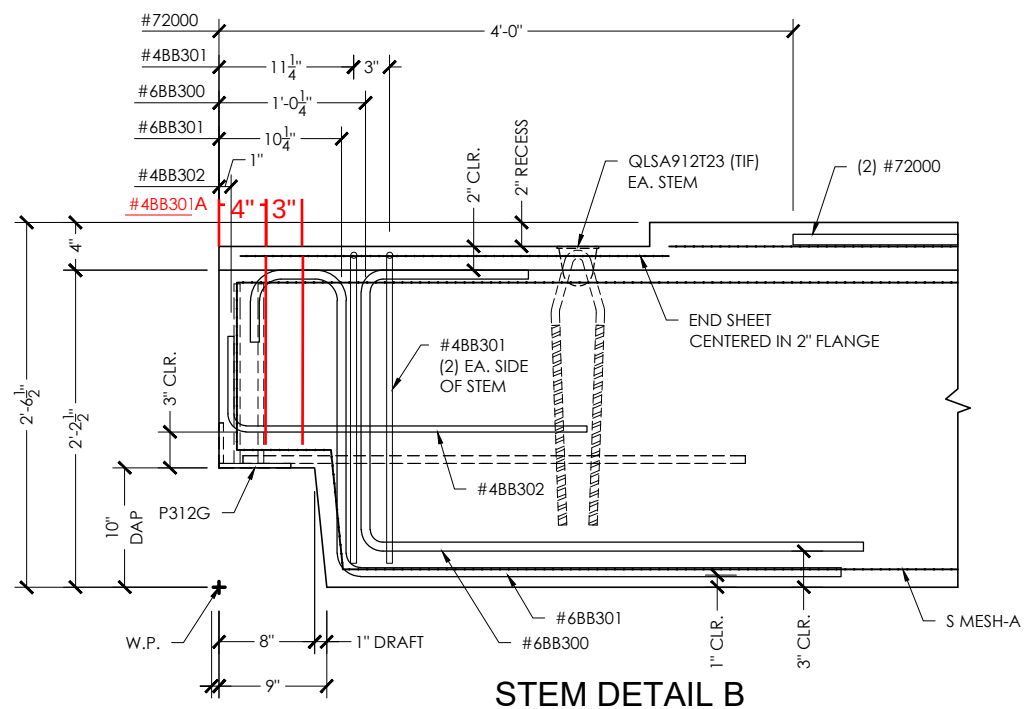

STEM DETAIL B

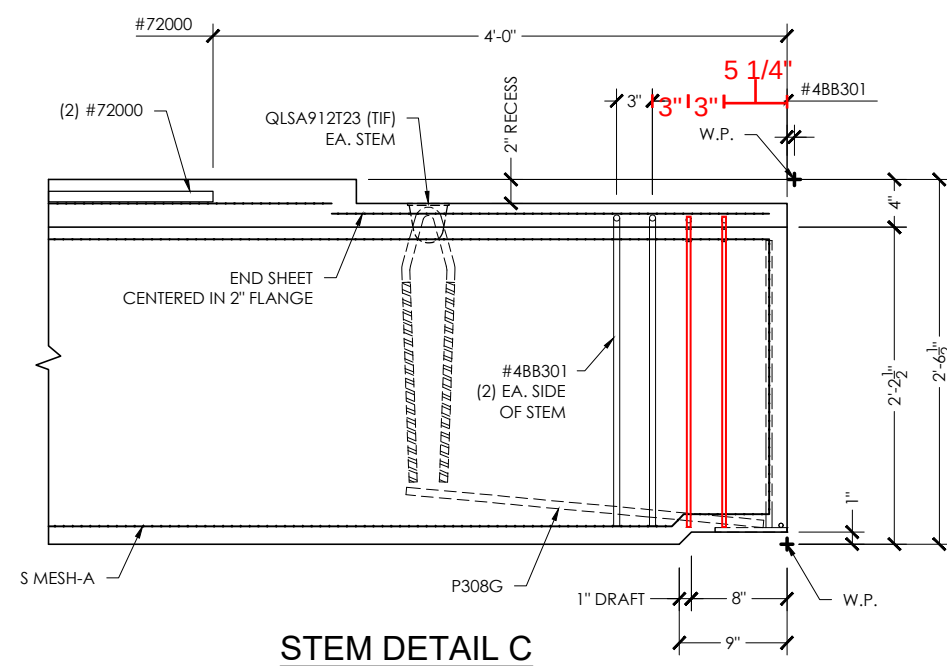

STEM DETAIL C

NOTES:

1. ALL REBAR IS TO BE 1 1/2" CLR. CL OF FLANGE UNO.
2. ALL DIMENSIONS ARE TO CENTERLINE UNO

SYMBOLS

S.I.F. = SIDE IN FORM

B.I.F. = BOTTOM IN FORM

T.I.F. = TOP IN FORM

(S#) = STEM NO. (X") = DAP DIM.

DECK = BROOM SWIRL

RECESSES = ROUGH BROOM (TRANSVERSE)

ALL STEM ENDS = AS CAST

SIDE OF STEM = STEEL FORM

BOTTOM OF STEM = STEEL FORM

REL.	DESCRIPTION	DATE	BY
1	FOR PRODUCTION	07/22/2025	JMW

DRAWN: DAI	CHECKED: CO	ENGR: BEM	PLOTTED: 06/17/2025
------------	-------------	-----------	---------------------

NORTHEAST PRECAST

4081 S. Lincoln Ave., Vineland, NJ 08361
OFFICE: 856-699-2557 FAX: 856-765-9087
www.northeastprecast.com

PROJECT: WOODBRIDGE METROPARK GARAGE

JOB NO. 24-NE1096	PIECE MARK DT007	SHEET NO. 2 of 2
-------------------	------------------	------------------