


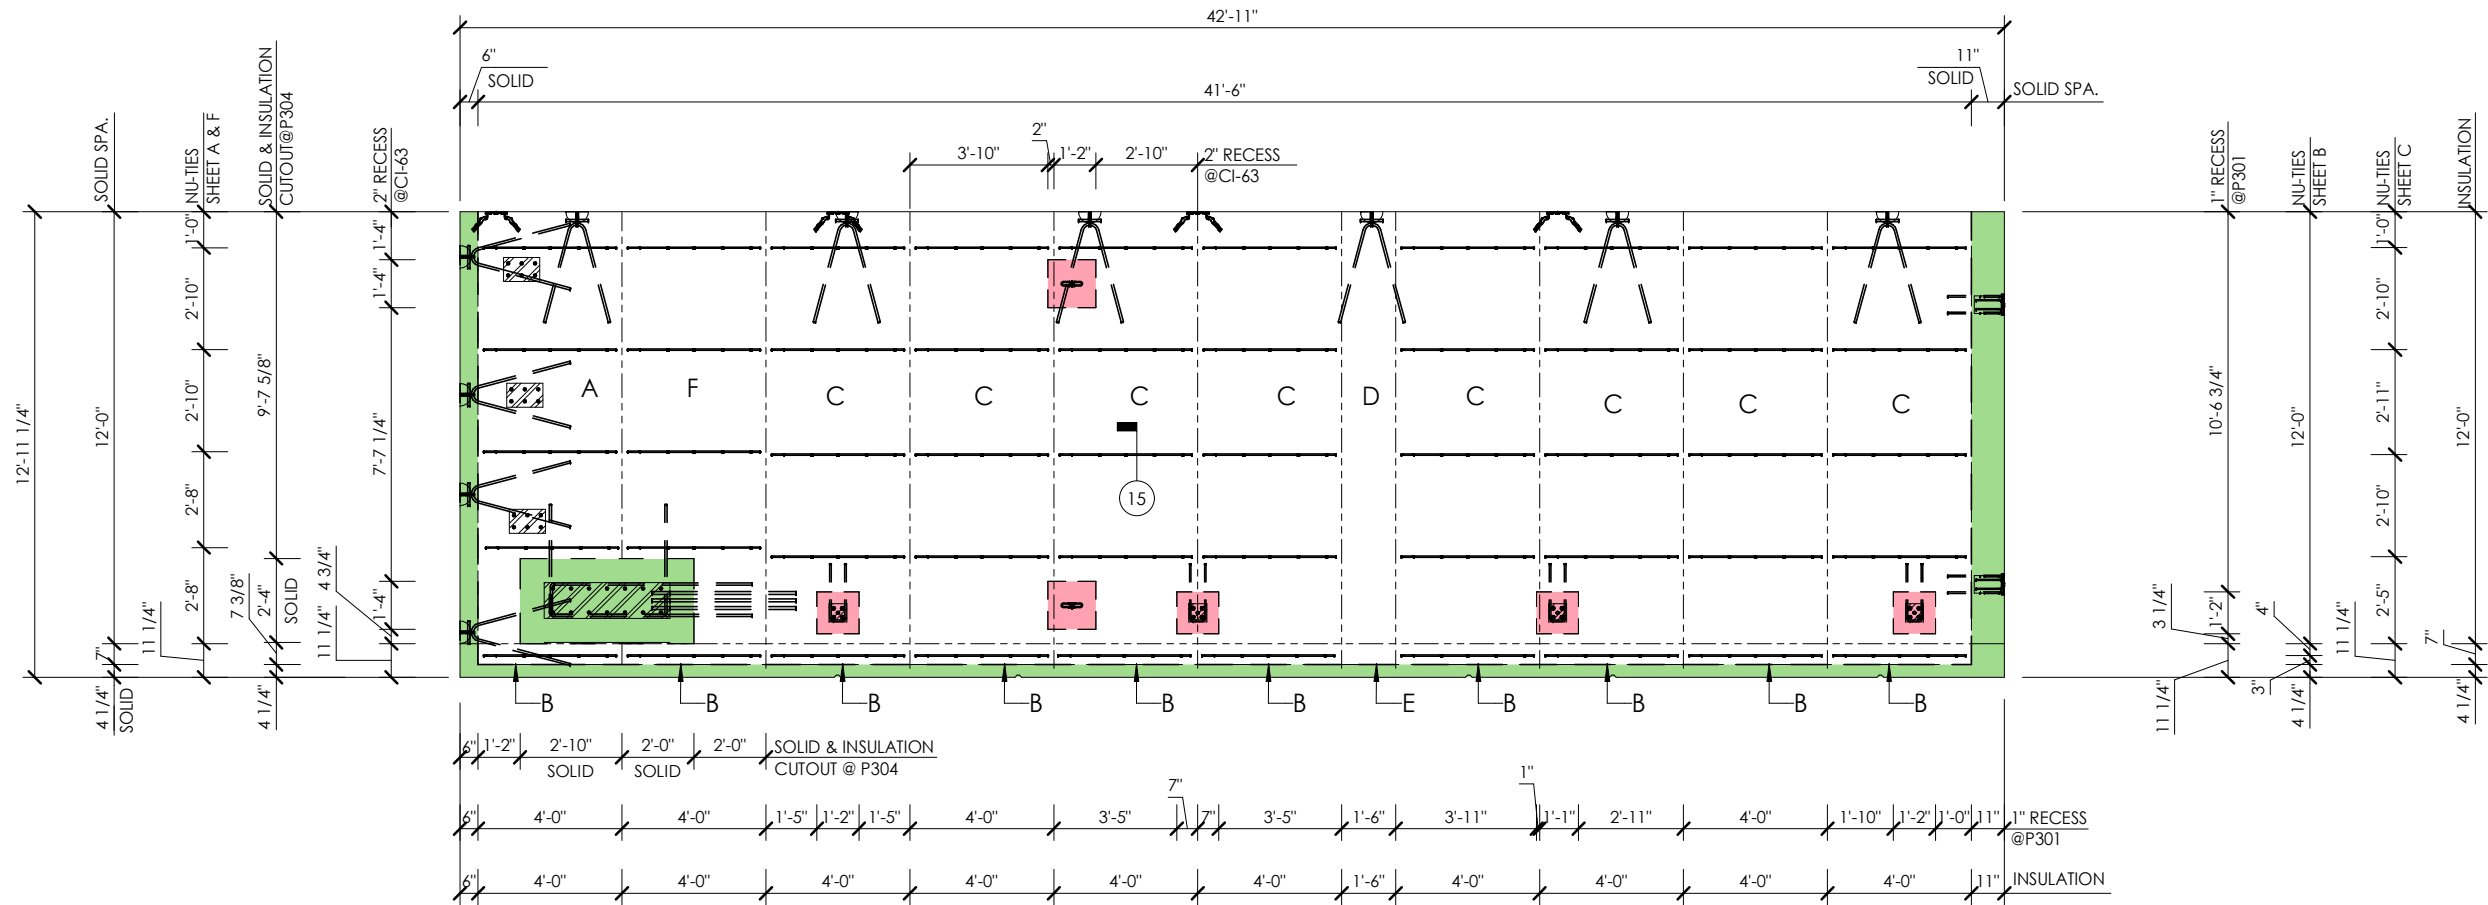

FOAM DRAWING

PIECES OF 1" EPS(1.25 PCF):
CI-63: (2) 1'-4" X1'-4"

PIECES OF 2" EPS(1.25 PCF):
P301: (4) 1'-2" X1'-2"

PIECES OF 3" EPS(1.25 PCF):
A/C/F: (10) PIECES @ 4'-0" X 12'-0"
B: (10) PIECES @ 4'-0" X 0'-7"
D: (1) PIECE @ 1'-6" X 12'-0"
E: (1) PIECE @ 1'-6" X 0'-7"

- NOTES:
- 1. ALL REBAR IS TO BE 1" CLR. UNO
 - 2. ALL DIMENSIONS ARE TO CENTERLINE UNO
 - 3. SPLIT STRONGBACK C.Y. 50/50 FACE MIX / BACK MIX
 - 4. PLACE REBAR 2" FROM EDGE OF ROUGH OPENINGS
- SYMBOLS:
- S.I.F. = SIDE IN FORM
 - B.I.F. = BOTTOM IN FORM
 - T.I.F. = TOP IN FORM
 - E.O.P.= EDGE OF PLATE
 - ST = STEEL TROWEL
 - FM = FORM FINISH

REV.	DESCRIPTION	DATE	BY
1	FOR PRODUCTION	07/01/25	PS

DRAWN: SRB	CHECKED: ACB	ENGR: PP	PLOTTED: 7/2/2025 8:41:30 PM
------------	--------------	----------	------------------------------

PRECAST ENGINEER :

BUILDING THEORY


18 KING ST. EAST SUITE 1400,
TORONTO ON M5C 1C4, CANADA
WWW.BUILDINGTHEORY.COM
TEL: +1-647-906-7812

NORTHEAST PRECAST


4081 S.LINCOLN AVE.
VINELAND, NJ 08361
OFFICE: 866-699-2557 FAX: 856-765-9087
www.northeastprecast.com

PROJECT: EAST PARK 309


FORM NO. 25-NE1193	PIECE MARK W017	SHEET NO. 2 OF 3
--------------------	-----------------	------------------

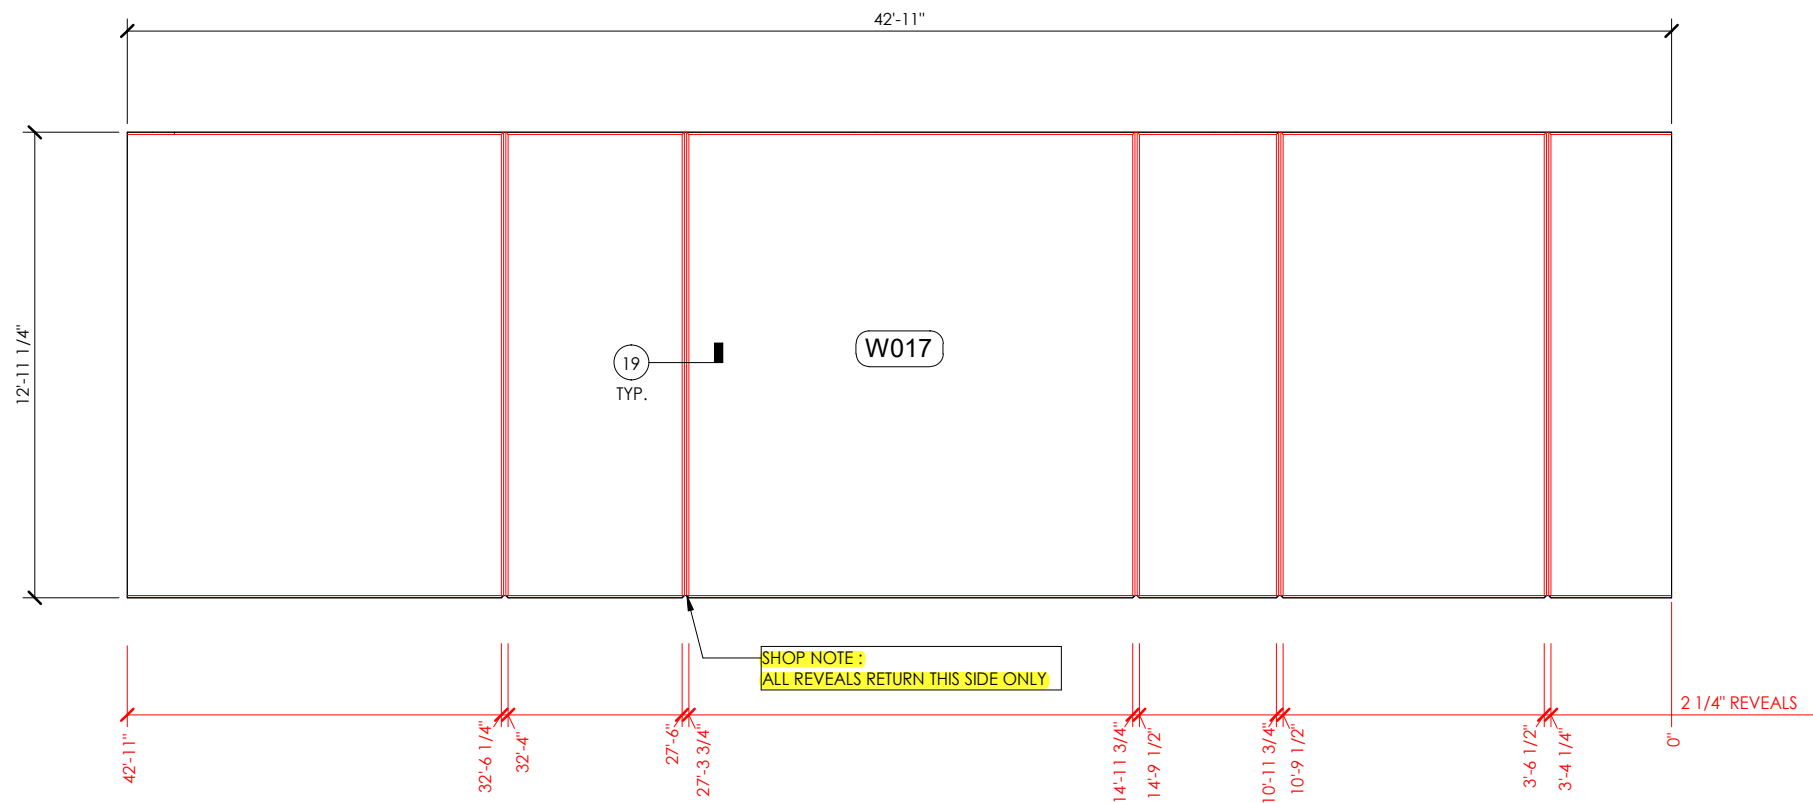

REVEAL DRAWING

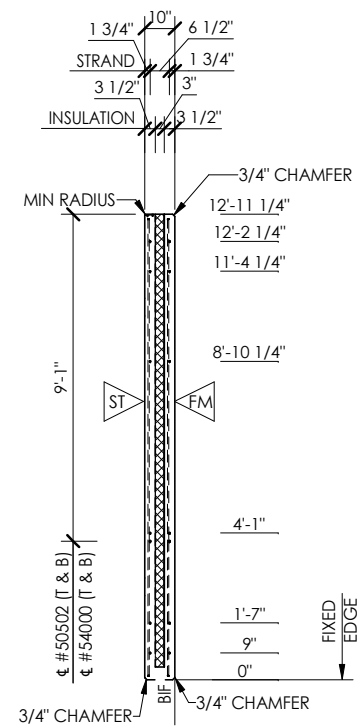

SECTION VIEW

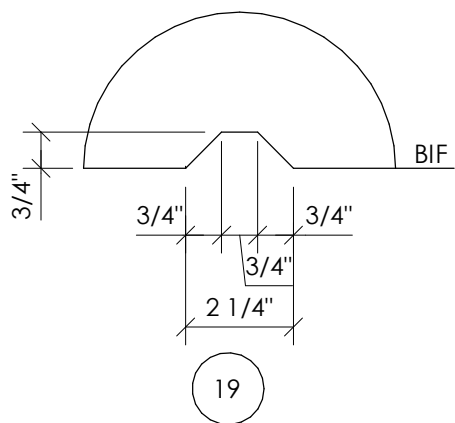

- NOTES:
1. ALL REBAR IS TO BE 1" CLR. UNO
 2. ALL DIMENSIONS ARE TO CENTERLINE UNO
 3. SPLIT STRONGBACK C.Y. 50/50 FACE MIX / BACK MIX
 4. PLACE REBAR 2" FROM EDGE OF ROUGH OPENINGS
- SYMBOLS:
- S.I.F. = SIDE IN FORM
B.I.F. = BOTTOM IN FORM
T.I.F. = TOP IN FORM
E.O.P. = EDGE OF PLATE
- ST = STEEL TROWEL
FM = FORM FINISH

REV.	DESCRIPTION	DATE	BY
1	FOR PRODUCTION	07/01/25	PS

DRAWN: SRB	CHECKED: ACB	ENGINEER: PP	PLOTTED: 7/2/2025 8:41:38 PM
------------	--------------	--------------	------------------------------

PRECAST ENGINEER :

BUILDING THEORY

18 KING ST. EAST SUITE 1400,
TORONTO ON M5C 1C4, CANADA
WWW.BUILDINGTHEORY.COM
TEL: +1-647-906-7812

NORTHEAST PRECAST

4081 S. LINCOLN AVE.
VINELAND, NJ 08361
OFFICE: 866-699-2557 FAX: 856-765-9087
www.northeastprecast.com

PROJECT: EAST PARK 309

DRAW NO.	PIECE MARK	SHEET NO.
25-NE1193	W017	3 OF 3