



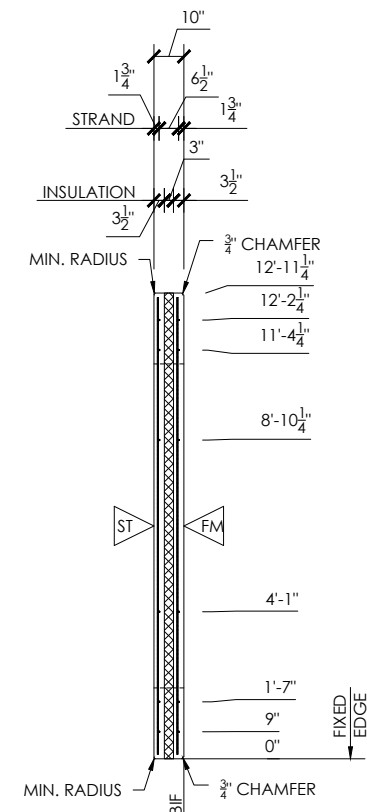

SECTION VIEW

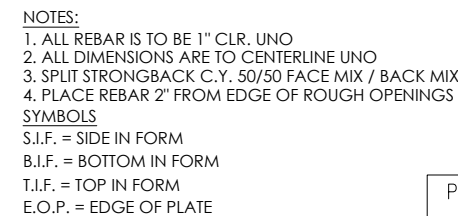

▽ST = STEEL TROWEL

 = FORM FINISH

CONTROL NUMBER 034

PRODUCTION NOTE:
#31208 TIED BELOW
STRAND @ P041

BUILDING THEORY	
CHECKER SP	ENGINEER PP
JUNE. 02, 2025	JUNE.02, 2025

PRECAST ENGINEER:



18 KING ST. EAST SUITE 1400,
TORONTO ON M5C 1C4, CANADA
WWW.BUILDINGTHEORY.COM
TEL: +1-647-906-7812

**NORTHEAST
PRECAST**

4081 S. LINCOLN AVE.
VINELAND, NJ 08361
OFFICE: 856-699-2557 FAX: 856-765-9087
www.northeastprecast.com

PROJECT: LINK - HYATT

JOB NO.
25-NE1204

PIECE MARK	W034
------------	------

SHEET NO.

1 of 3

STEALTH 100	FLANGE CONNECTOR	10	EA
CI-63	3/4" DIA. x 3 1/2" CI-6334312P COIL INSERT	2	EA
NU-TIE	7" NU-TIE	49	EA
P002	#4 x1'-10" BENT BAR THREADED ONE END W/ STANDARD COUPLER	6	EA
P041	PL 3/4" x 4" x 7" W/(2) #4 x 1'-6" BAR & (2) #3 x 1'-3" BAR	2	EA
P302	PL 3/8" x 1'-0" x 1'-4" W/(8) 5/8" DIA. x 4 1/8" HCA	3	EA
QLFIP12T7G	12T SAND PANEL ANCHOR	10	EA
MARK	DESCRIPTION	QTY.	UOM

#30108		8	EA
#31208		73	EA
#50300		8	EA
#51206		4	EA
#51208		4	EA
#5BB001		18	EA
#5BB002		2	EA
#5BB300		2	EA
MARK		QTY.	UOM

#5BB303		3	EA
#80006		20	EA
1/2 STRAND	1/2 DIAMETER STRAND 31 KIPS	12	EA
MARK	DESCRIPTION		

CONCRETE MIX		
MIX	CY	B/F
725N	7.12	B
700A	6.24	F

f'c (28 DAYS)	6,000 PSI
f'c (SHIPPING)	4,000 PSI
f'ci (RELEASE)	3,500 PSI

PIECES REQ'D:
1

WEIGHT:
54200 LB

DESIGN:
IWP1.00

PC. FOUND ON
E-DRAWING:
E-3.03

REL.	DESCRIPTION	DATE	BY
1	FOR PRODUCTION	06/02/25	PS

DRAWN: AK	CHECKED: SP	ENGINE: PP	PLOTTED: 6/2/2025 6:47 PM
-----------	-------------	------------	---------------------------


PROJECT: LINK - HYATT

JOB NO.
25-NE1204

PIECE MARK	W034
------------	------

SHEET NO.

1 of 3

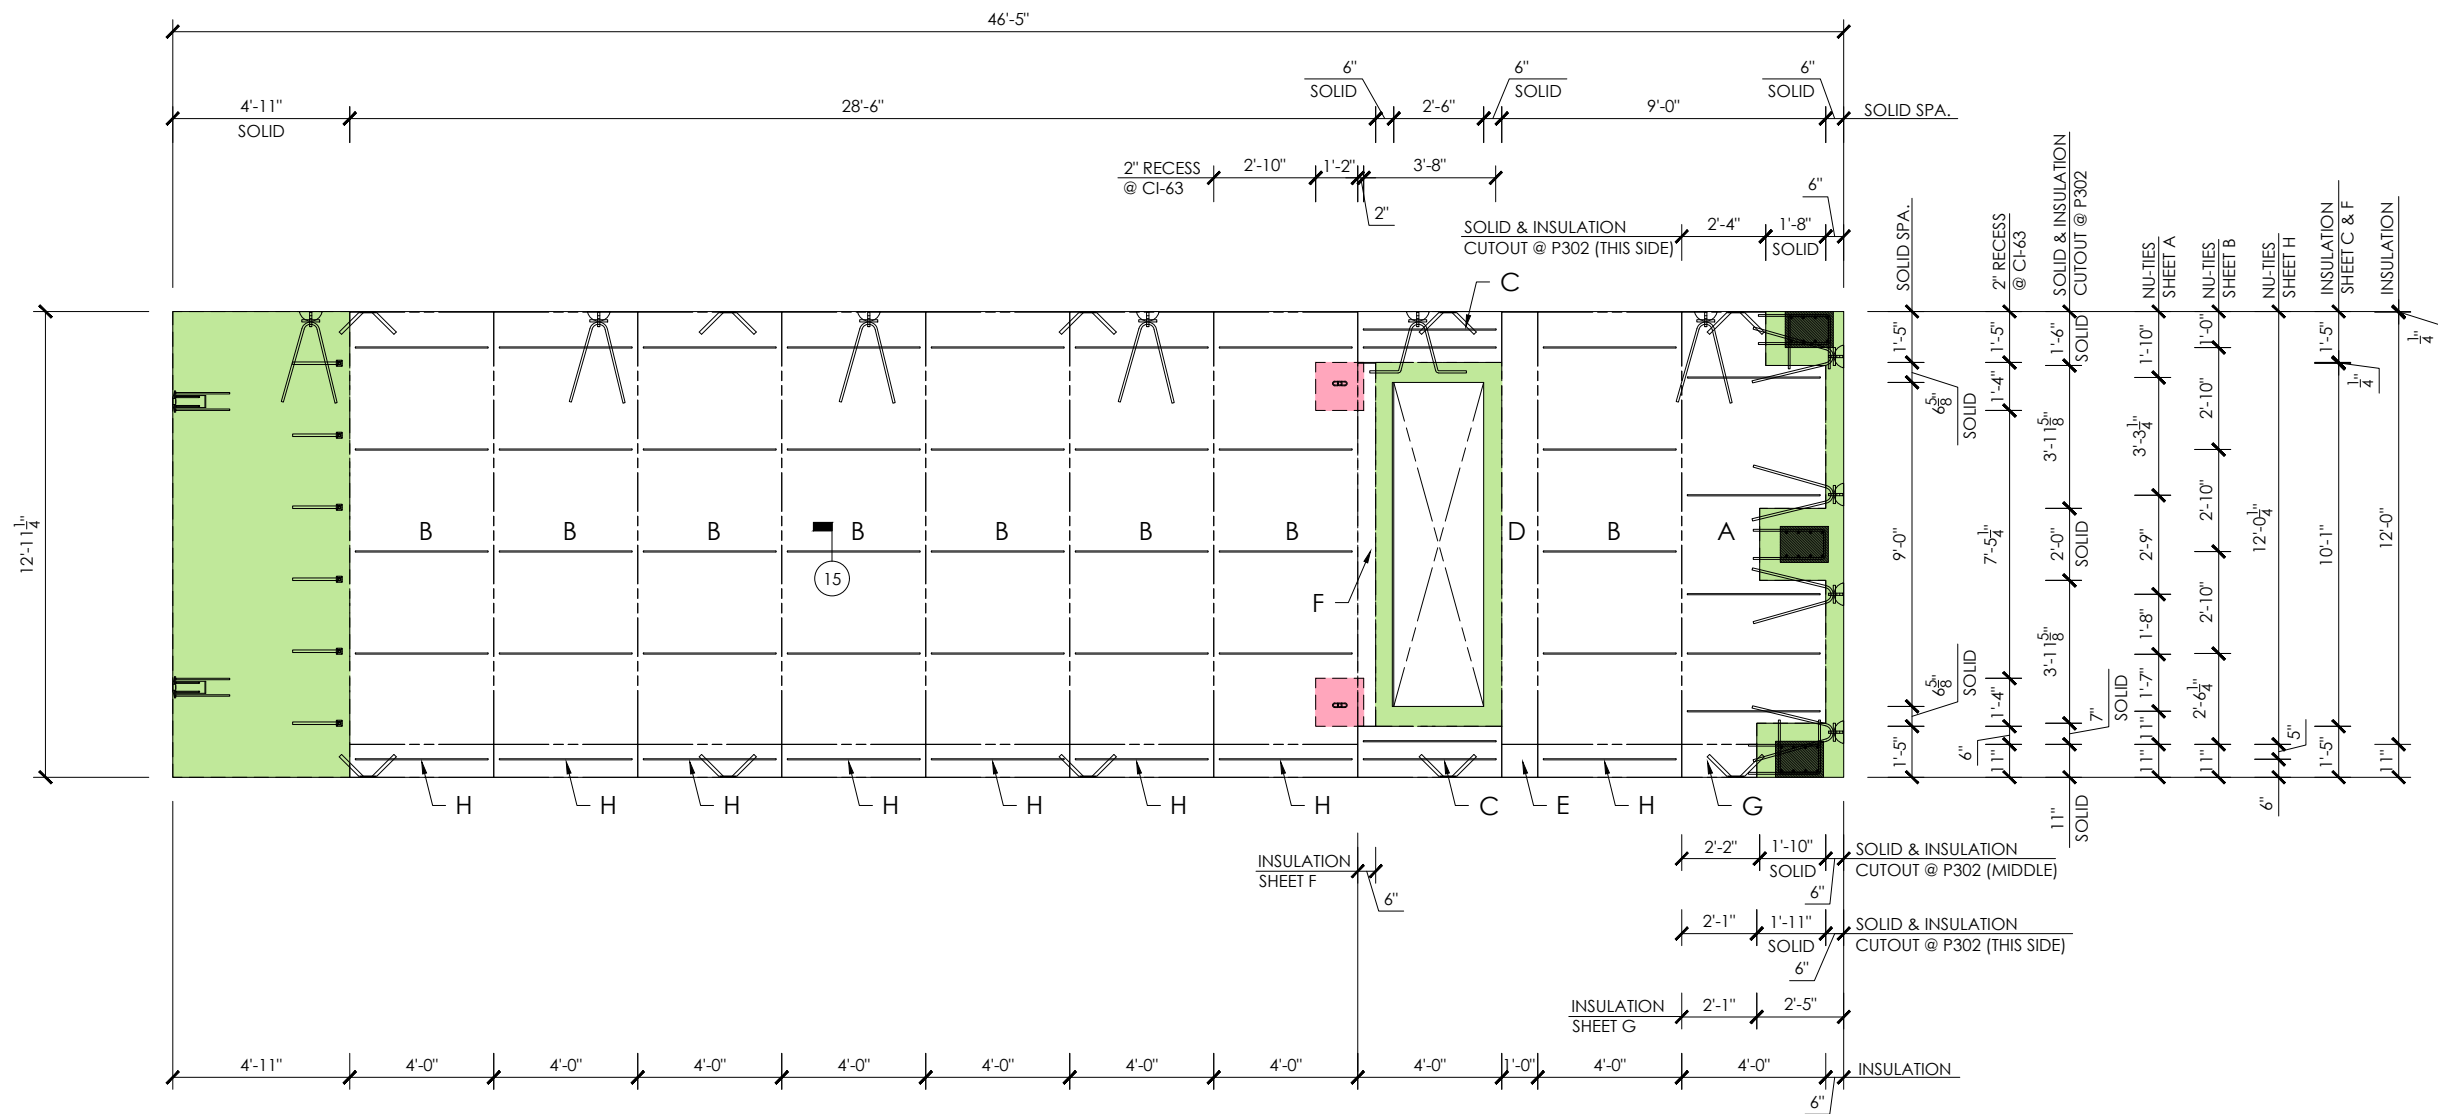

FOAM DRAWING

PIECES OF 1" EPS (1.25 PCF):
CI-63: (2) 1'-4" X 1'-4"

PIECES OF 3" EPS (1.25 PCF):
A/B: (9) PIECES @ 4'-0" X 12'-0"
C: (2) PIECES @ 4'-0" X 1'-5"
D: (1) PIECE @ 1'-0" X 12'-0"
E: (1) PIECE @ 1'-0" X 0'-11"
F: (1) PIECE @ 0'-6" X 10'-1"
G: (1) PIECE @ 2'-1" X 0'-11"
H: (8) PIECES @ 4'-0" X 0'-11"

- NOTES:
1. ALL REBAR IS TO BE 1" CLR. UNO
 2. ALL DIMENSIONS ARE TO CENTERLINE UNO
 3. SPLIT STRONGBACK C.Y. 50/50 FACE MIX / BACK MIX
 4. PLACE REBAR 2" FROM EDGE OF ROUGH OPENINGS

SYMBOLS

S.I.F. = SIDE IN FORM
B.I.F. = BOTTOM IN FORM
T.I.F. = TOP IN FORM
E.O.P. = EDGE OF PLATE

ST = STEEL TROWEL
FM = FORM FINISH

REL.	DESCRIPTION	DATE	BY
1	FOR PRODUCTION	06/02/25	PS

DRAWN: AK	CHECKED: SP	ENGR: PP	PLOTTED: 6/2/2025 6:47 PM
-----------	-------------	----------	---------------------------


PRECAST ENGINEER:




NORTHEAST PRECAST

4081 S. LINCOLN AVE.
VINELAND, NJ 08361
OFFICE: 866-699-2557 FAX: 856-765-9087
www.northeastprecast.com


PROJECT:	LINK - HYATT
JOB NO.	25-NE1204
PIECE MARK	W034
SHEET NO.	2 of 3

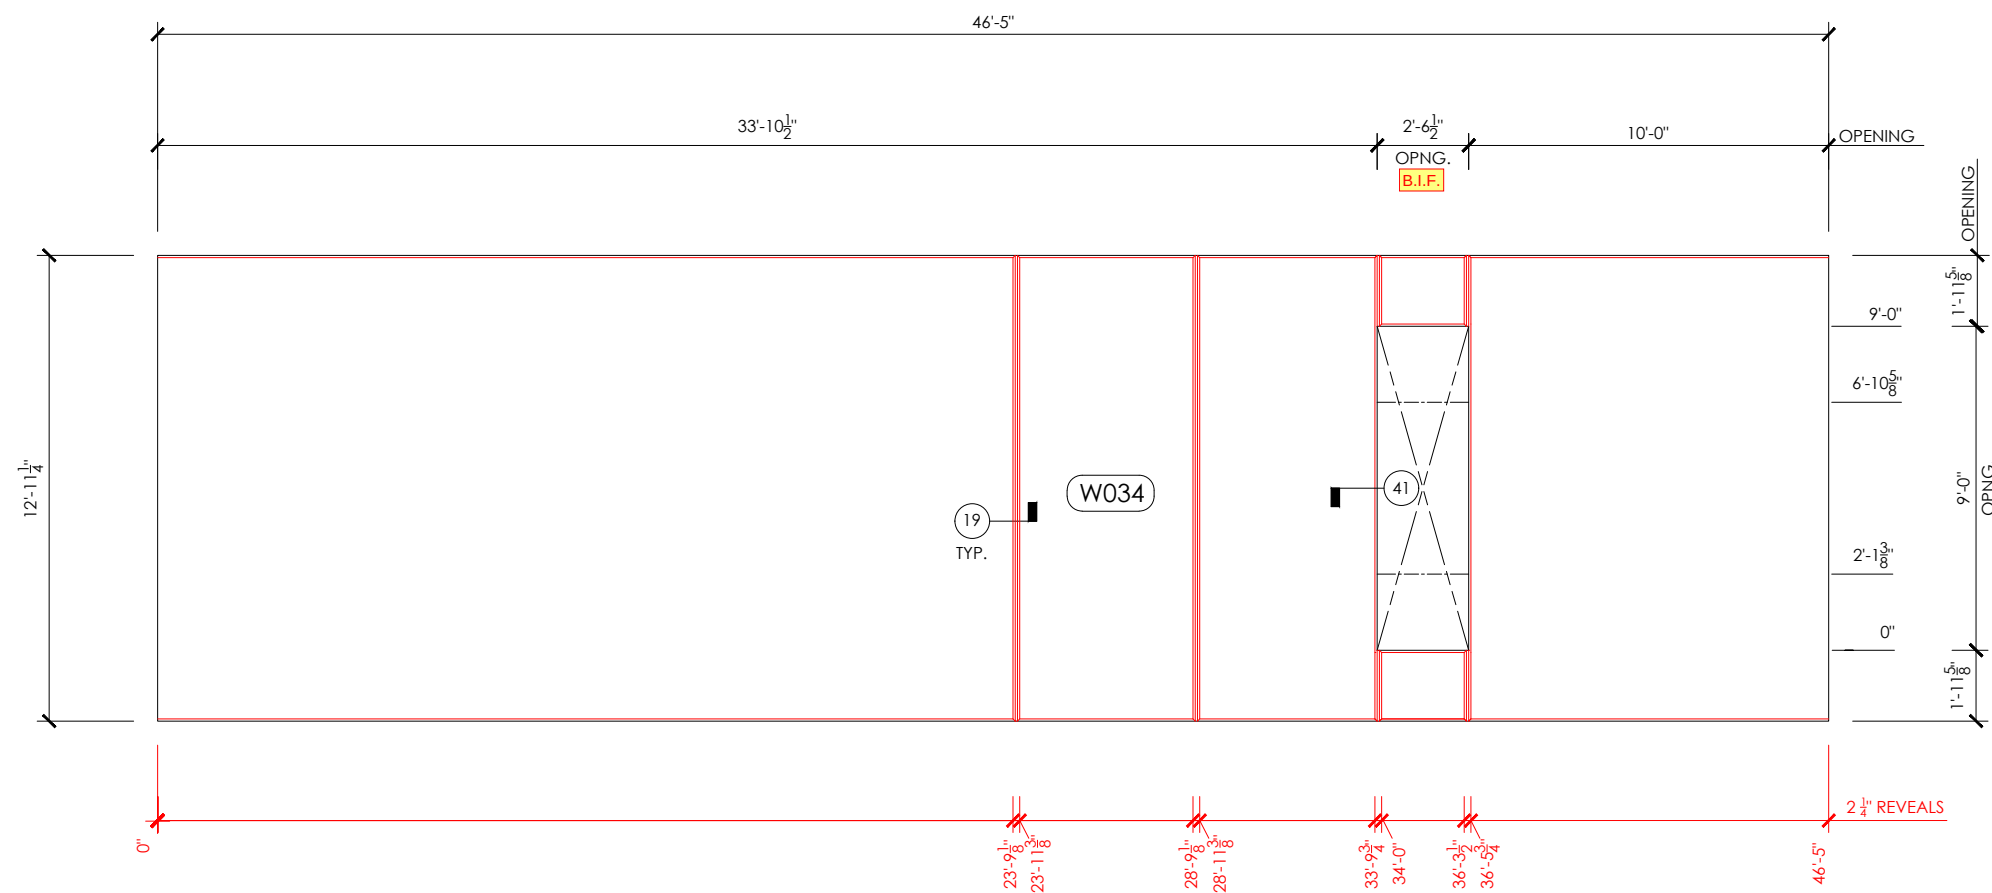

REVEAL DRAWING

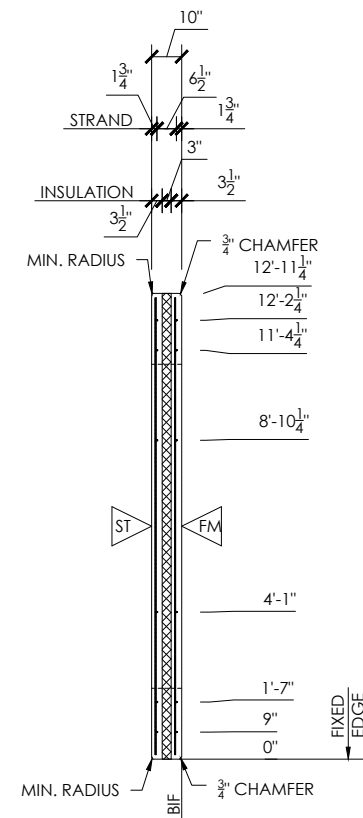

SECTION VIEW

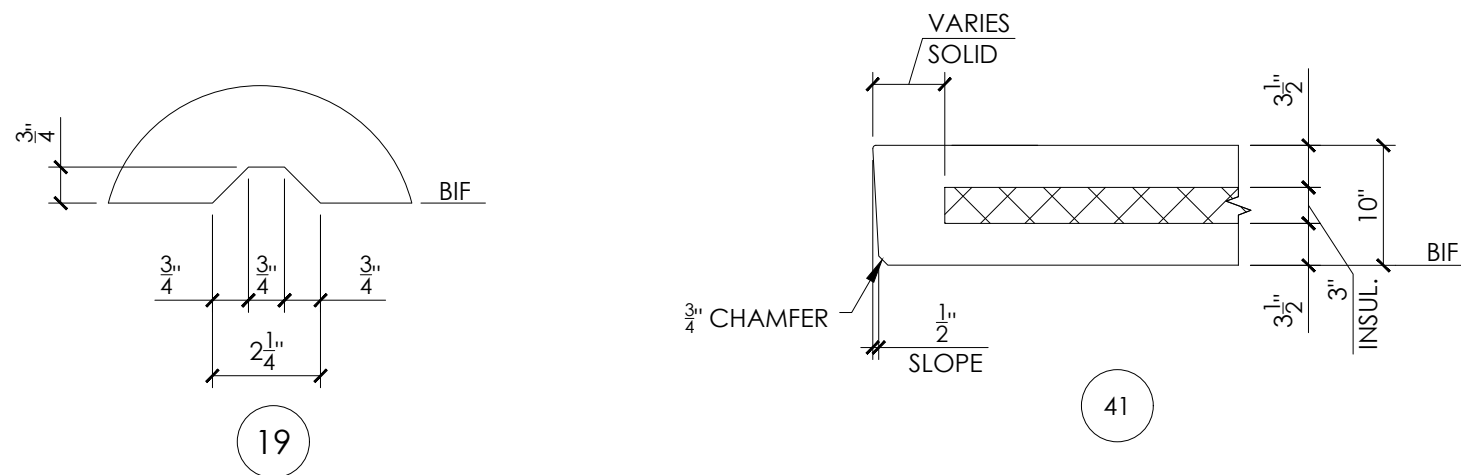

- NOTES:
1. ALL REBAR IS TO BE 1" CLR. UNO
 2. ALL DIMENSIONS ARE TO CENTERLINE UNO
 3. SPLIT STRONGBACK C.Y. 50/50 FACE MIX / BACK MIX
 4. PLACE REBAR 2" FROM EDGE OF ROUGH OPENINGS

SYMBOLS

- S.I.F. = SIDE IN FORM
B.I.F. = BOTTOM IN FORM
T.I.F. = TOP IN FORM
E.O.P. = EDGE OF PLATE

ST = STEEL TROWEL

FM = FORM FINISH

REL.	DESCRIPTION	DATE	BY
1	FOR PRODUCTION	06/02/25	PS

DRAWN: AK	CHECKED: SP	ENGR: PP	PLOTTED: 6/2/2025 6:47 PM
-----------	-------------	----------	---------------------------

PRECAST ENGINEER:



NORTHEAST PRECAST

4081 S. LINCOLN AVE.
VINELAND, NJ 08361
OFFICE: 866-699-2557 FAX: 856-765-9087
www.northeastprecast.com

PROJECT:	LINK - HYATT
JOB NO.	25-NE1204
PIECE MARK	W034
SHEET NO.	3 of 3