


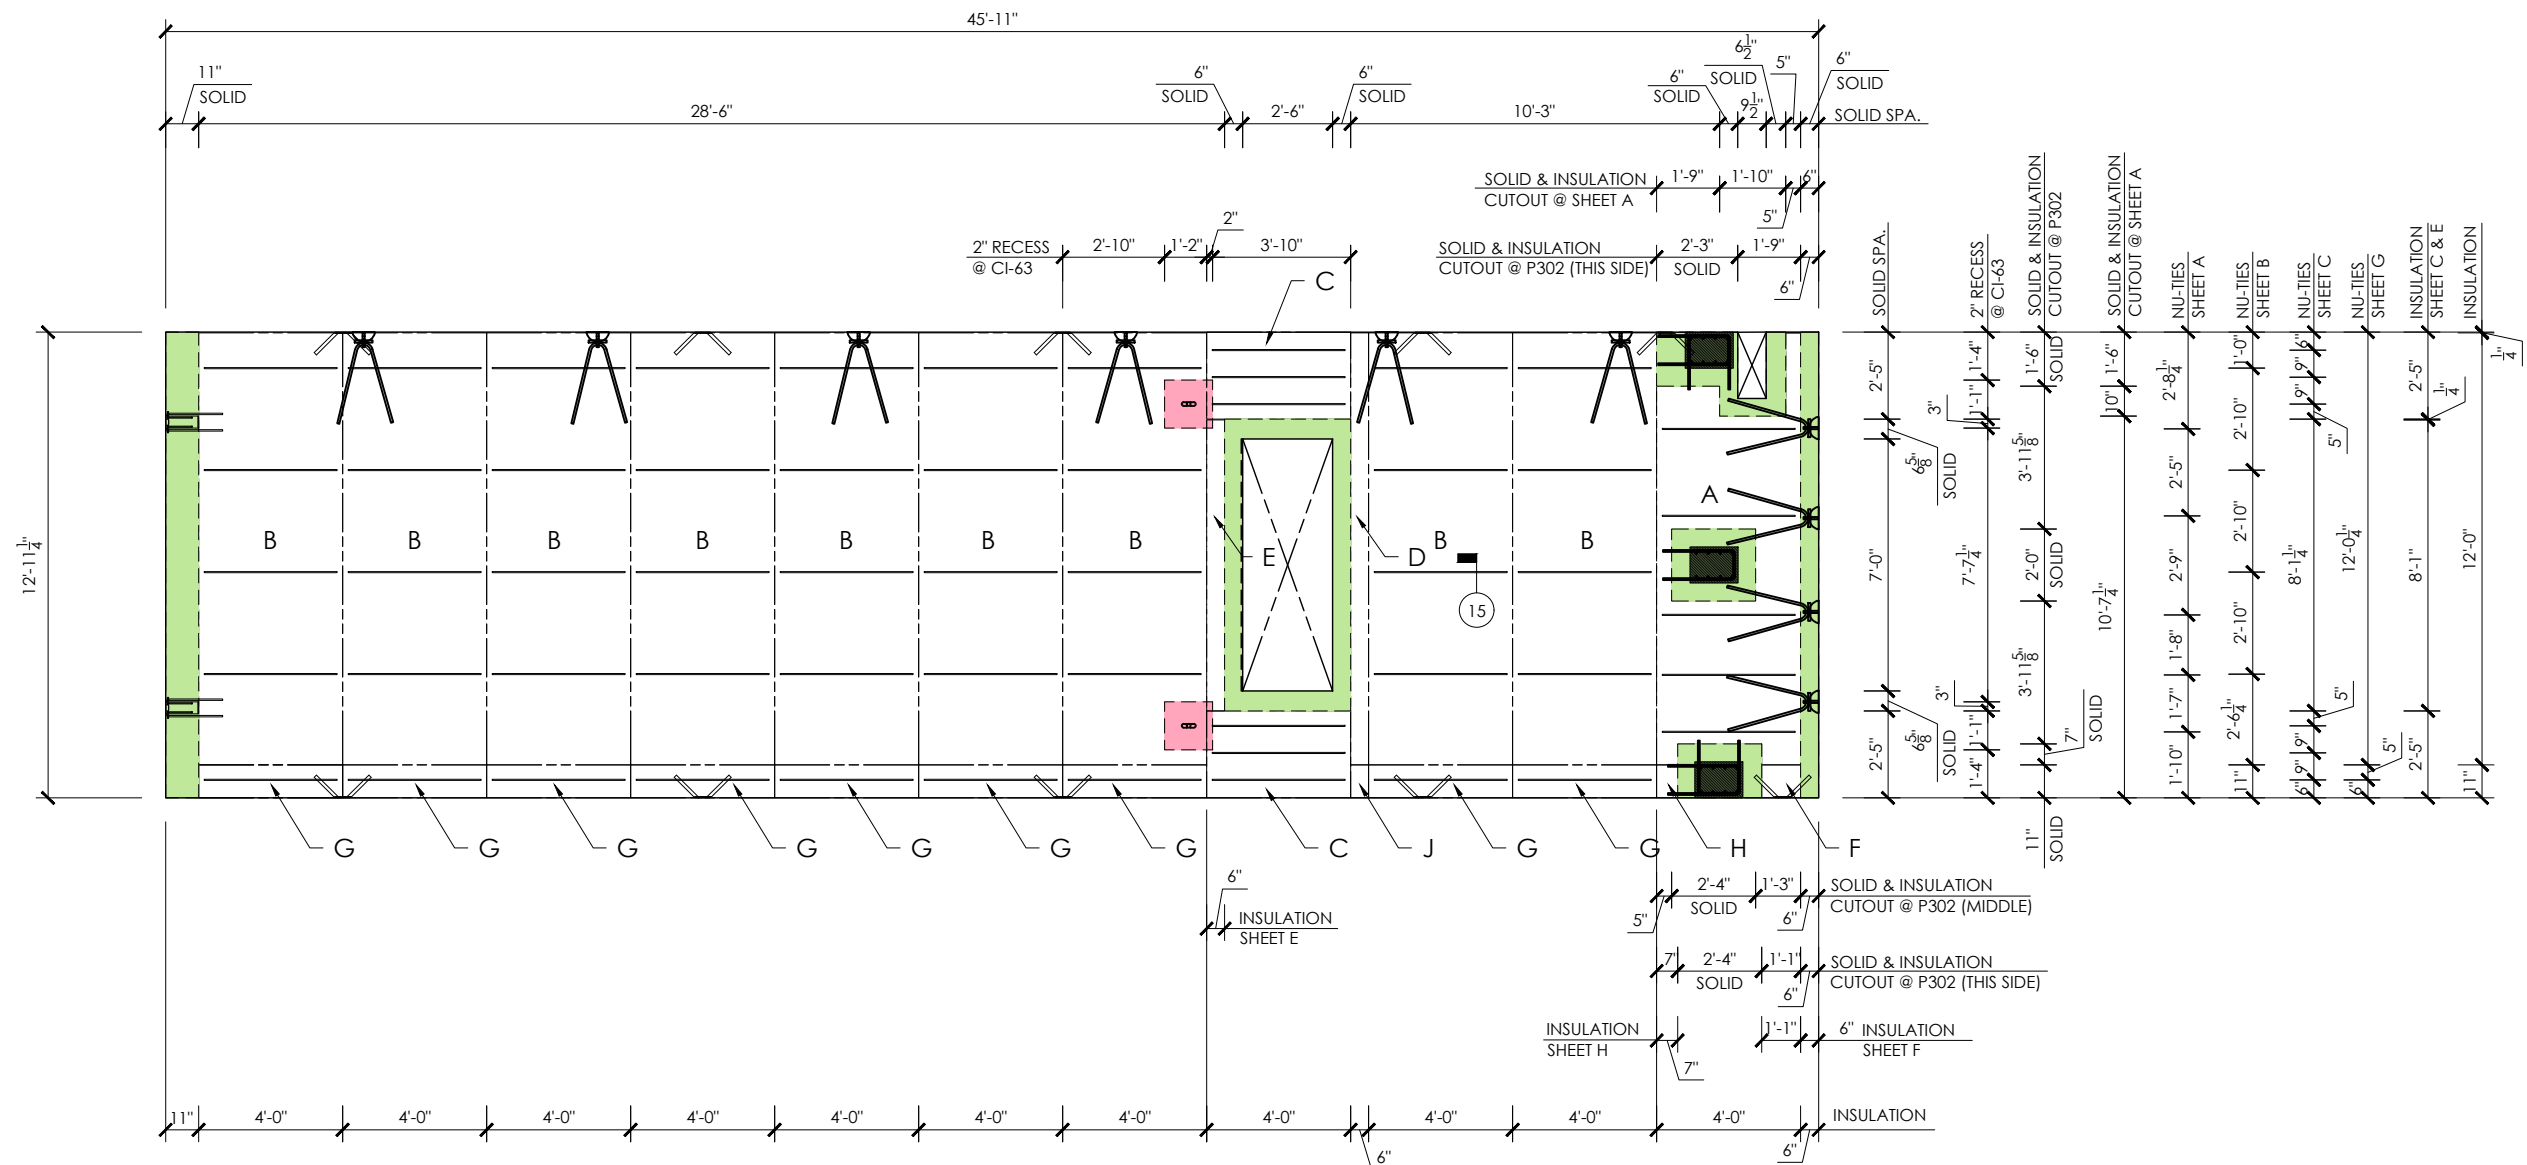

FOAM DRAWING

PIECES OF 1" EPS (1.25 PCF):
CI-63: (2) 1'-4" X 1'-4"

PIECES OF 3" EPS (1.25 PCF):
A/B: (10) PIECES @ 4'-0" X 12'-0"
C: (2) PIECES @ 4'-0" X 2'-5"
D: (1) PIECE @ 0'-6" X 12'-0"
E: (1) PIECE @ 0'-6" X 8'-1"
F: (1) PIECE @ 1'-1" X 0'-11"
G: (9) PIECES @ 4'-0" X 0'-11"
H: (1) PIECE @ 0'-7" X 0'-11"
J: (1) PIECE @ 0'-6" X 0'-11"

- NOTES:
1. ALL REBAR IS TO BE 1" CLR. UNO
 2. ALL DIMENSIONS ARE TO CENTERLINE UNO
 3. SPLIT STRONGBACK C.Y. 50/50 FACE MIX / BACK MIX
 4. PLACE REBAR 2" FROM EDGE OF ROUGH OPENINGS

SYMBOLS
S.I.F. = SIDE IN FORM
B.I.F. = BOTTOM IN FORM
T.I.F. = TOP IN FORM
E.O.P. = EDGE OF PLATE
ST = STEEL TROWEL
FM = FORM FINISH

REL.	DESCRIPTION	DATE	BY
1	FOR PRODUCTION	05/27/25	PS

DRAWN: SUS	CHECKED: SP	ENGR: BK	PLOTTED: 5/27/2025 6:41 PM
------------	-------------	----------	----------------------------

PRECAST ENGINEER:



BUILDING THEORY

18 KING ST. EAST SUITE 1400,
TORONTO ON M5C 1C4, CANADA
WWW.BUILDINGTHEORY.COM
TEL: +1-647-906-7812


NORTHEAST PRECAST

4081 S. LINCOLN AVE.
VINELAND, NJ 08361
OFFICE: 866-699-2557 FAX: 856-765-9087
www.northeastprecast.com

PROJECT:	LINK - HYATT
JOB NO.	25-NE1204
PIECE MARK	W225
SHEET NO.	2 of 3

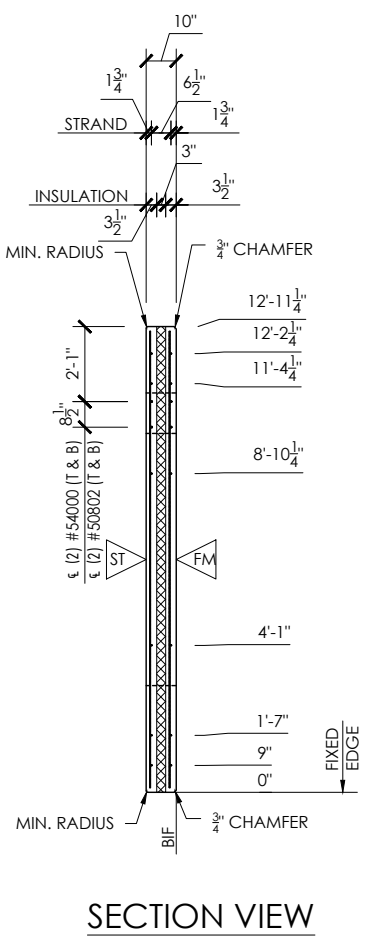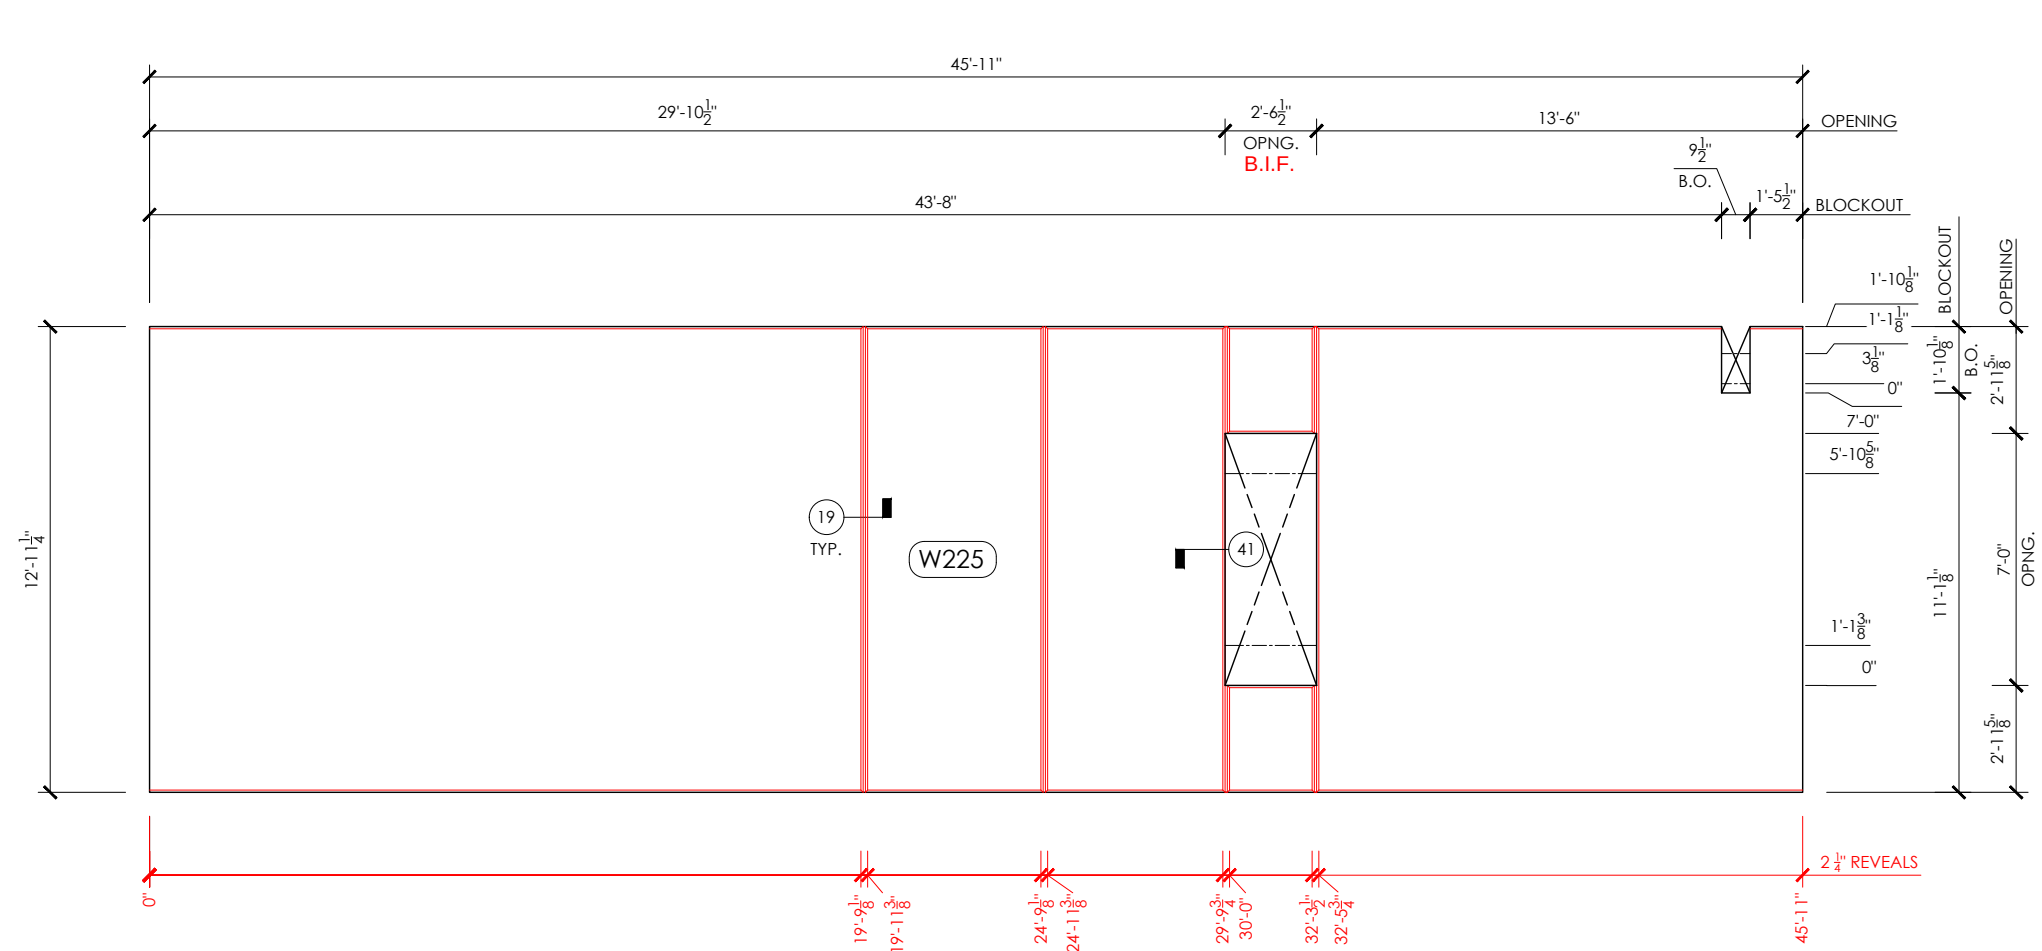

REVEAL DRAWING

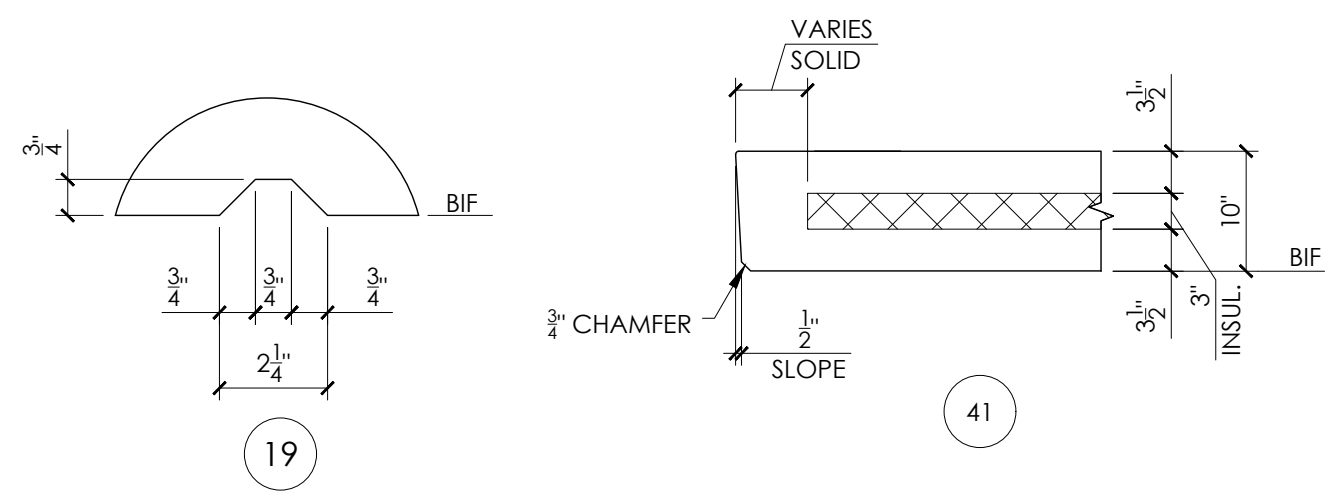

NOTES:
1. ALL REBAR IS TO BE 1" CLR. UNO
2. ALL DIMENSIONS ARE TO CENTERLINE UNO
3. SPLIT STRONGBACK C.Y. 50/50 FACE MIX / BACK MIX
4. PLACE REBAR 2" FROM EDGE OF ROUGH OPENINGS

SYMBOLS
S.I.F. = SIDE IN FORM
B.I.F. = BOTTOM IN FORM
T.I.F. = TOP IN FORM
E.O.P. = EDGE OF PLATE

ST = STEEL TROWEL
FM = FORM FINISH

REL.	DESCRIPTION	DATE	BY
1	FOR PRODUCTION	05/27/25	PS

DRAWN: SUS	CHECKED: SP	ENGR: BK	PLOTTED: 5/27/2025 6:41 PM
------------	-------------	----------	----------------------------

PRECAST ENGINEER:

BUILDING THEORY
18 KING ST. EAST SUITE 1400,
TORONTO ON M5C 1C4, CANADA
WWW.BUILDINGTHEORY.COM
TEL: +1-647-906-7812

NORTHEAST PRECAST
4081 S. LINCOLN AVE.
VINELAND, NJ 08361
OFFICE: 866-699-2557 FAX: 856-765-9087
www.northeastprecast.com

PROJECT:	LINK - HYATT
JOB NO.	25-NE1204
PIECE MARK	W225
SHEET NO.	3 of 3