



SECTION VIEW



NOTES:

1. ALL REBAR IS TO BE 1" CLR. UNO
2. ALL DIMENSIONS ARE TO CENTERLINE UNO
3. SPLIT STRONGBACK C.Y. 50/50 FACE MIX / BACK MIX
4. PLACE REBAR 2" FROM EDGE OF ROUGH OPENINGS

SYMBOLS

S.I.F. = SIDE IN FORM
B.I.F. = BOTTOM IN FORM
T.I.F. = TOP IN FORM
E.O.P. = EDGE OF PLATE

 = STEEL TROWEL

 = FORM FINISH

BUILDING THEORY	
CHECKER SP	ENGINEER PP
<u>AUG. 11, 2025</u>	<u>AUG. 11, 2025</u>

PRECAST ENGINEER:



18 KING ST. EAST SUITE 1400,
TORONTO ON M5C 1C4, CANADA
WWW.BUILDINGTHEORY.COM
TEL: +1-647-906-7812

**NORTHEAST
PRECAST**
4081 S. LINCOLN AVE.
VINELAND, NJ 08361
OFFICE: 866-699-2557 FAX: 856-765-9087
www.northeastprecast.com

PROJECT: PROJECT AERIE		
JOB NO. 25-NE1209	PIECE MARK W016	SHEET NO. 1 of 3

STEALTH 100	FLANGE CONNECTOR	6	EA
CI-63	3/4" DIA. x 3 1/2" CI-6334312P COIL INSERT	2	EA
NU-TIE	7" NU-TIE	51	EA
P041	PL 3/4" x 4" x 7" W/[2] #4 x 1'-6" BAR & [2] #3 x 1'-3" BAR	2	EA
P305	PL 3/8" x 1'-0" x 2'-1" W/[10] 5/8" DIA. x 4 1/8" HCA	3	EA
QLFIP127G	12T SAND PANEL ANCHOR	8	EA
LPA2T512G	LIFTING PIN ANCHOR	1	EA
MARK	DESCRIPTION	QTY.	UOM

#30200		23	EA
#30206		23	EA
#31302		42	EA
#3BB500		3	EA
#50300		4	EA
#51302		2	EA
#5BB001		14	EA
#5BB002		2	EA
MARK		QTY:	UOM

#5BB302		6	EA
#5BB303		2	EA
#61302		4	EA
#61502		6	EA
#80006		16	EA
1/2 STRAND	1/2 DIAMETER STRAND 31 KIPS	12	EA
MARK	DESCRIPTION		

MIX	CY	B/F
725N	4.31	B
700A	3.89	F

Fc (28 DAYS) 6,000 PSI
Fc (SHIPPING) 4,000 PSI
Fci (RELEASE) 3,500 PSI

PIECES REQ'D:
1


WEIGHT:
33200 LB

DESIGN:
IWP3.00

P.C. FOUND ON
E-DRAWING:
E-3.01

REL.	DESCRIPTION	DATE	BY
1	FOR PRODUCTION	08/11/25	PS

DRAWN: NC	CHECKED: SP	ENGR: PP	PLOTTED: 8/11/2025 2:44 PM
--------------	----------------	-------------	-------------------------------

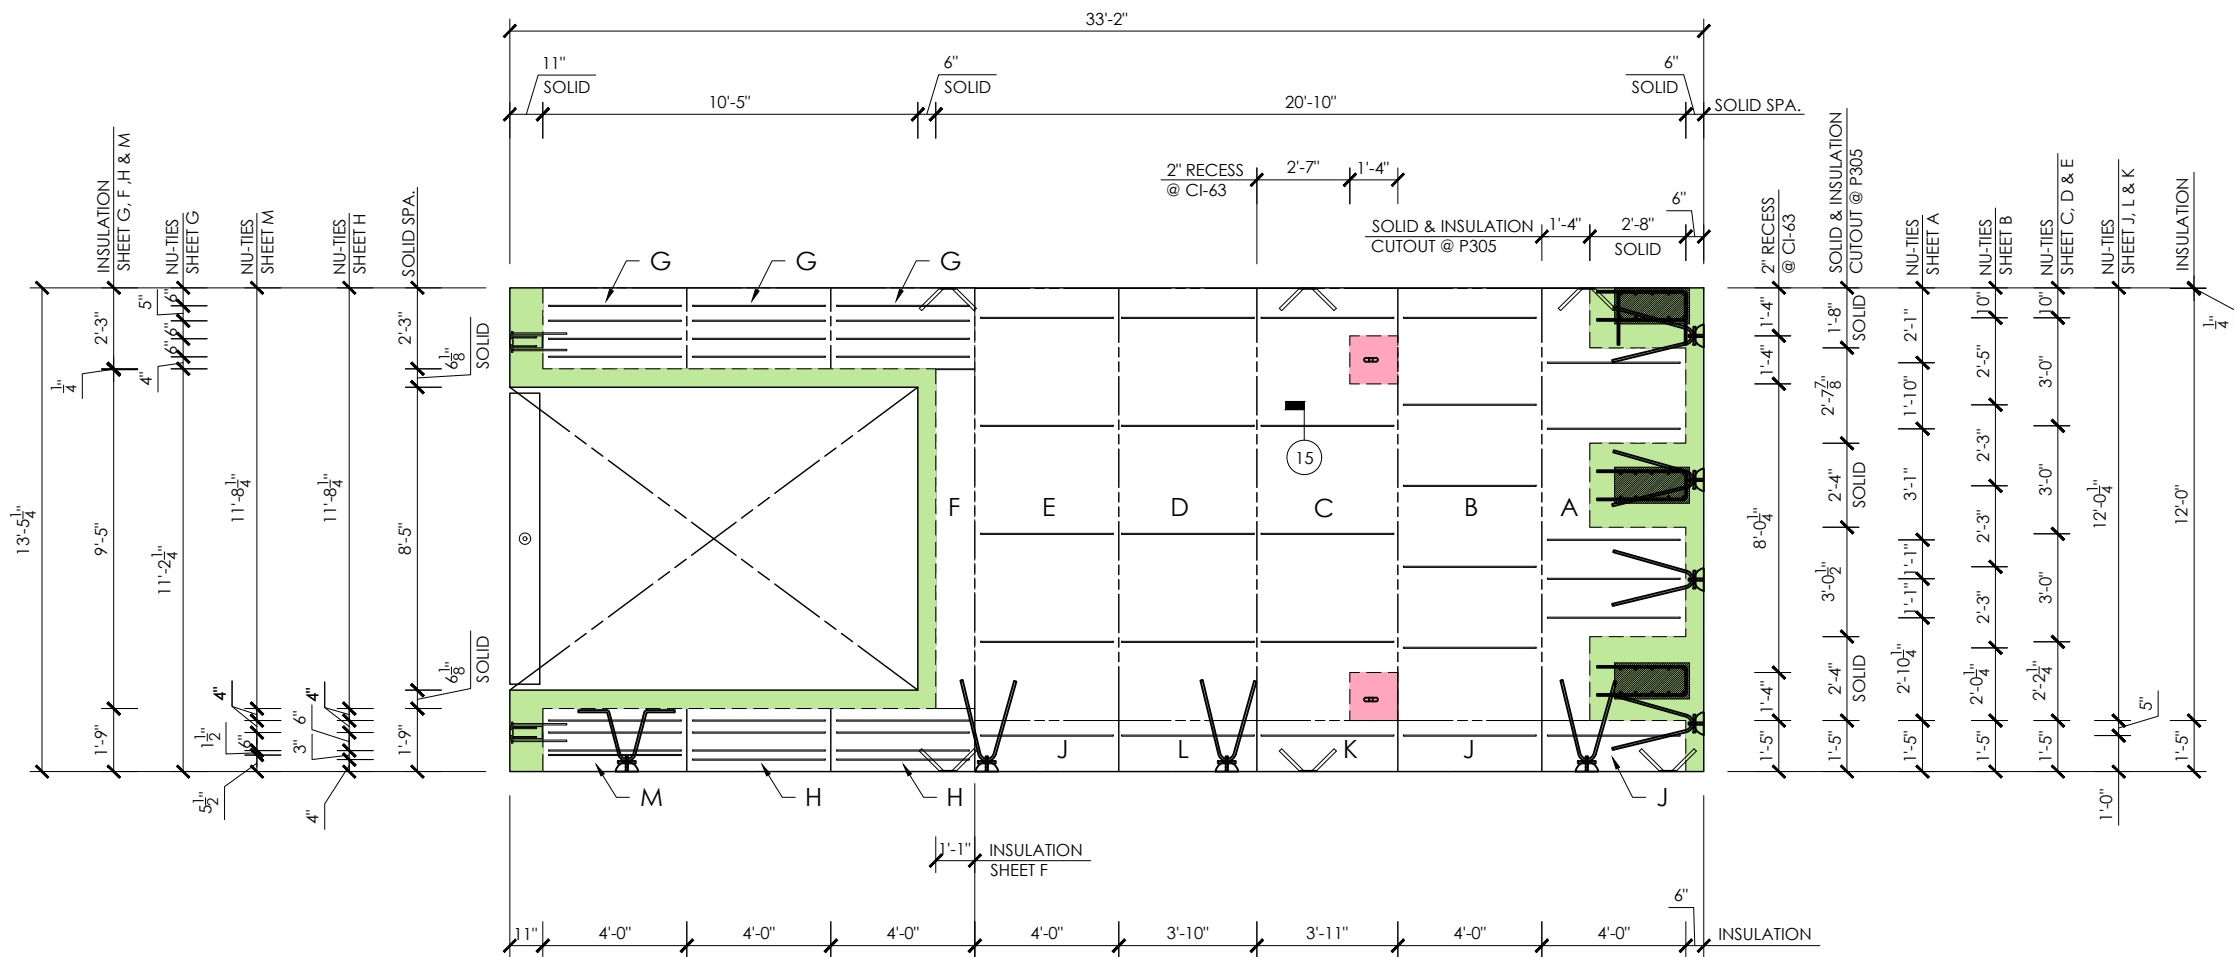

FOAM DRAWING

PIECES OF 1" XPS:
CI-63: (2) 1'-4" X 1'-4"

PIECES OF 3" XPS:
A/B/E: (3) PIECES @ 4'-0" X 12'-0"
C: (1) PIECE @ 3'-11" X 12'-0"
D: (1) PIECE @ 3'-10" X 12'-0"
F: (1) PIECE @ 1'-1" X 9'-5"
G: (3) PIECES @ 4'-0" X 2'-3"
H/M: (3) PIECES @ 4'-0" X 1'-9"
J: (3) PIECES @ 4'-0" X 1'-5"
K: (1) PIECE @ 3'-11" X 1'-5"
L: (1) PIECE @ 3'-10" X 1'-5"

- NOTES:
1. ALL REBAR IS TO BE 1" CLR. UNO
2. ALL DIMENSIONS ARE TO CENTERLINE UNO
3. SPLIT STRONGBACK C.Y. 50/50 FACE MIX / BACK MIX
4. PLACE REBAR 2" FROM EDGE OF ROUGH OPENINGS

SYMBOLS
S.I.F. = SIDE IN FORM
B.I.F. = BOTTOM IN FORM
T.I.F. = TOP IN FORM
E.O.P. = EDGE OF PLATE
ST = STEEL TROWEL
FM = FORM FINISH

REL.	DESCRIPTION	DATE	BY
1	FOR PRODUCTION	08/11/25	PS

DRAWN: NC	CHECKED: SP	ENGR: PP	PLOTTED: 8/11/2025 2:44 PM
-----------	-------------	----------	----------------------------

PRECAST ENGINEER:


BUILDING THEORY

18 KING ST. EAST SUITE 1400,
TORONTO ON M5C 1C4, CANADA
WWW.BUILDINGTHEORY.COM
TEL: +1-647-906-7812

NORTHEAST PRECAST


4081 S. LINCOLN AVE.
VINELAND, NJ 08361
OFFICE: 866-699-2557 FAX: 856-765-9087
www.northeastprecast.com

PROJECT:	PROJECT AERIE
JOB NO.	25-NE1209
PIECE MARK	W016
SHEET NO.	2 of 3

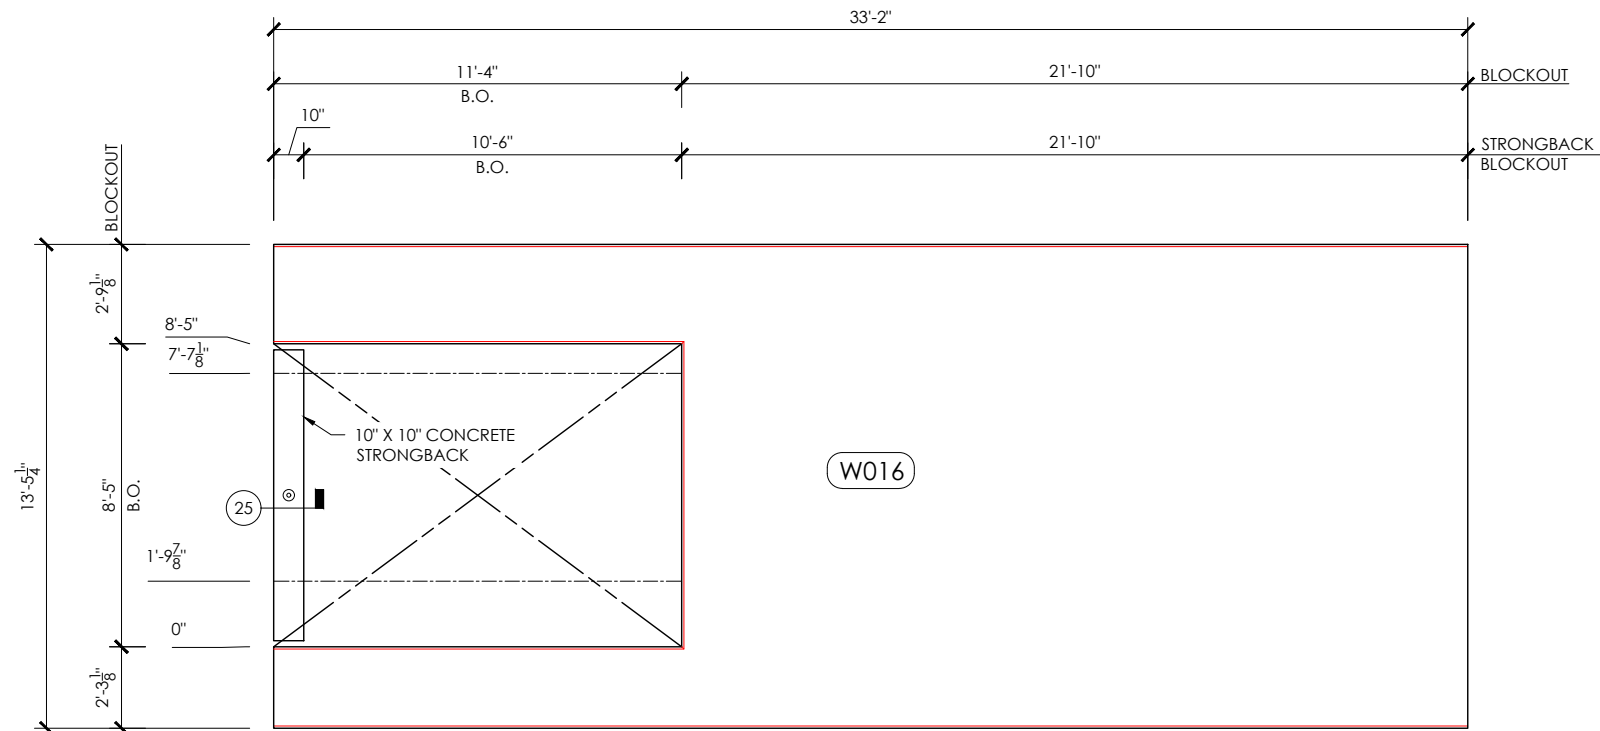


REVEAL DRAWING

SHOP NOTE:
NO REVEALS

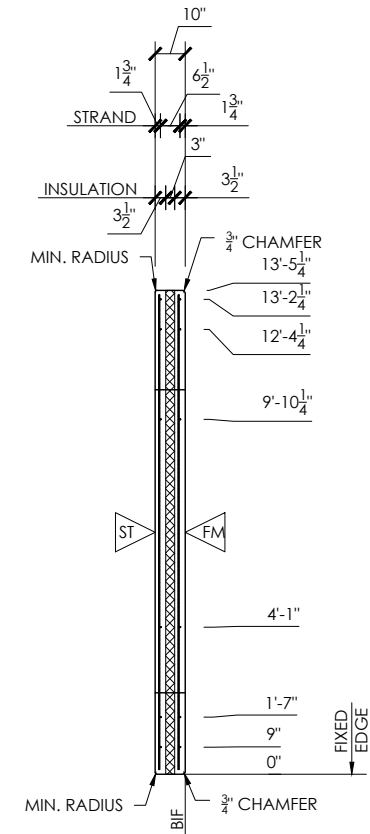

SECTION VIEW

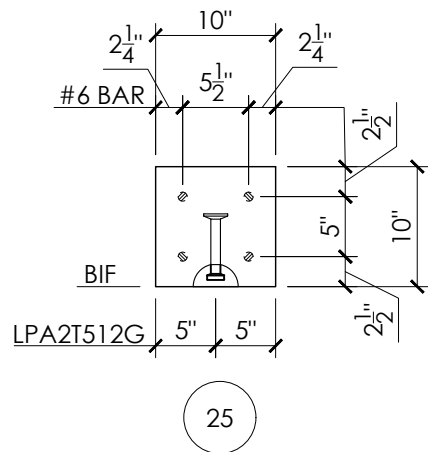

- NOTES:
1. ALL REBAR IS TO BE 1" CLR. UNO
 2. ALL DIMENSIONS ARE TO CENTERLINE UNO
 3. SPLIT STRONGBACK C.Y. 50/50 FACE MIX / BACK MIX
 4. PLACE REBAR 2" FROM EDGE OF ROUGH OPENINGS

SYMBOLS

- S.I.F. = SIDE IN FORM
B.I.F. = BOTTOM IN FORM
T.I.F. = TOP IN FORM
E.O.P. = EDGE OF PLATE

ST = STEEL TROWEL

FM = FORM FINISH

REL.	DESCRIPTION	DATE	BY
1	FOR PRODUCTION	08/11/25	PS

DRAWN: NC	CHECKED: SP	ENGR: PP	PLOTTED: 8/11/2025 2:44 PM
-----------	-------------	----------	----------------------------

PRECAST ENGINEER:



NORTHEAST PRECAST

4081 S. LINCOLN AVE.
VINELAND, NJ 08361
OFFICE: 866-699-2557 FAX: 856-765-9087
www.northeastprecast.com

PROJECT:	PROJECT AERIE
JOB NO.	25-NE1209
PIECE MARK	W016
SHEET NO.	3 of 3