




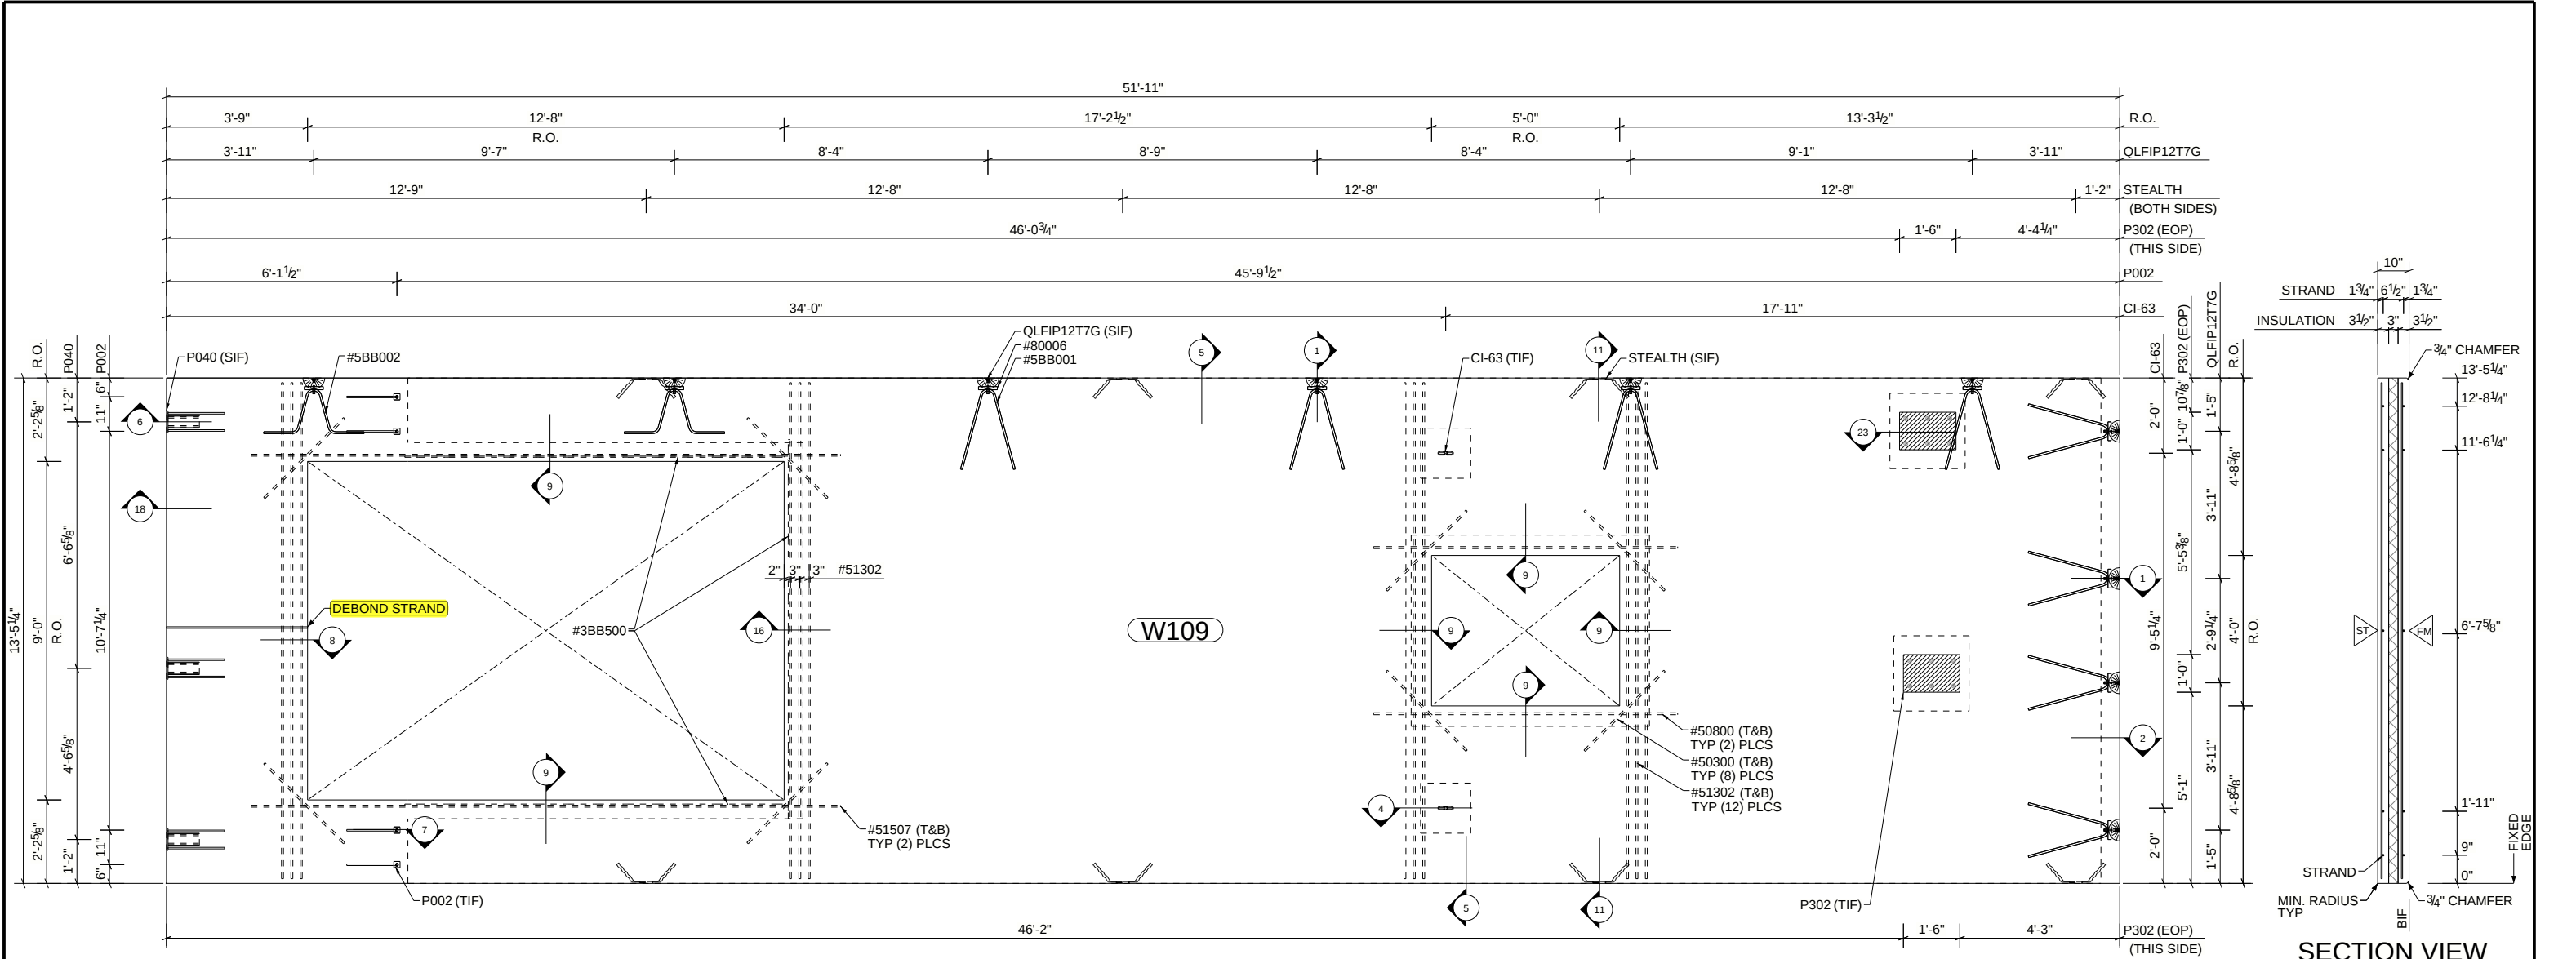

FORM VIEW

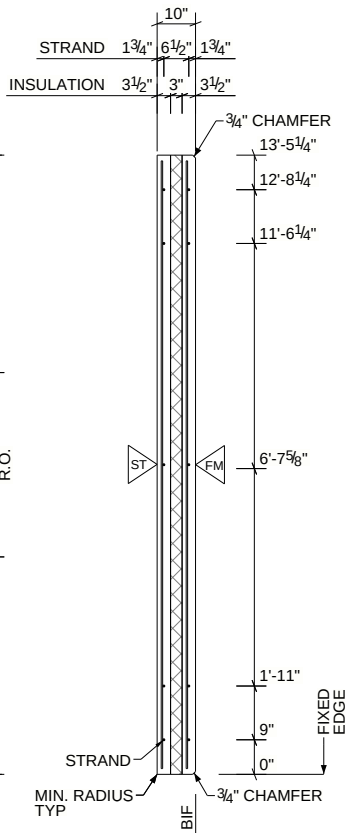

SECTION VIEW

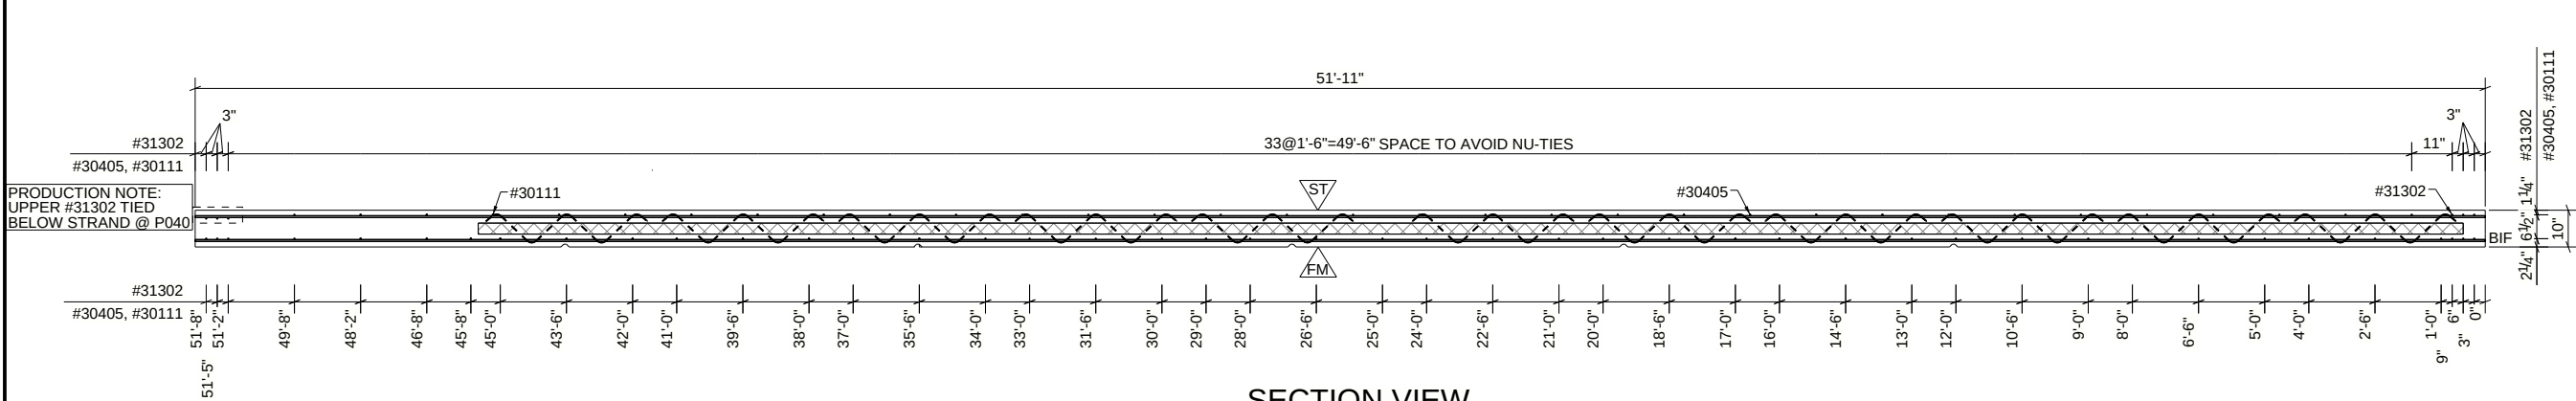

SECTION VIEW

DIAGONAL = 53'-7 9/16"


PRODUCTION NOTE:
BOTTOM WYTHE MUST BE RAKED AT ALL SOLID ZONE LOCATIONS

NOTES:
1. ALL REBAR IS TO BE 1 1/2" CLR. UNO
2. ALL DIMENSIONS ARE TO CENTERLINE UNO
3. ALL TRIM BARS TO BE 2" CLEAR FROM EDGE OF OPENING UNO

SYMBOLS
SIF = SIDE IN FORM
BIF = BOTTOM IN FORM
TIF = TOP IN FORM
EOP = EDGE OF PLATE

ST = STEEL TROWEL
FM = FORM FINISH
SPX = STRAND PATTERN

CI-63	CI6334312P FLARE COIL INS 3/4 DIA X 3 1/2"	2	EA	#31302	#3 REBAR X 13'-2" LONG	56	EA	1/2 STRAND	1/2 DIAMETER STRAND 28.90 Kips	10	EA	CONCRETE MIX		PIECES REQ'D: 1	REV.	DESCRIPTION	DATE	BY	 4081 S. LINCOLN AVE VINELAND, NJ 08361 OFFICE: 866-699-2557 FAX: 856-765-9087 www.northeastprecast.com PROJECT: NEWBURGH SOUTH LOGISTICS CENTER JOB NO. 25-NE1212 PIECE MARK W109 SHEET NO. 1 OF 3
NU-TIE	7" NU-TIE	50	EA	#3BB500	#3 BENT REBAR, SEE TABLE	3	EA					MIX	CY	B/F	0	ISSUED FOR PRODUCTION	07/01/2025	JOM	
P002	#4 X 1'-10" FORMSAVER	4	EA	#50300	#5 REBAR X 3'-0" LONG	16	EA					725N	7.06	B	1				
P040	PL3/4X4X0'-7" W/ (2) #4 X 1'-6"	3	EA	#50800	#5 REBAR X 8'-0" LONG	4	EA					700A	6.09	F	2				
P302	PL1/2X1'-0"X1'-6" W/ (6) 5/8" DIA X 4 1/8 LONG HCA	2	EA	#51302	#5 REBAR X 13'-2" LONG	24	EA					F _c (28 DAYS) 6000 PSI		DESIGN: SP1	3				
QLFIP127TG	12T SAND PANEL ANCHOR	10	EA	#51507	#5 REBAR X 15'-7" LONG	4	EA					F _c (SHIPPING) 5000 PSI			4				
STEALTH	STEALTH 100 FLANGE CONNECTOR	8	EA	#5BB001	#5 BENT REBAR, SEE TABLE	16	EA					F _c (RELEASE) 3500 PSI		CONTROL NO.: 109	5				
#30111	#3 REBAR X 1'-11" LONG	40	EA	#5BB002	#5 BENT REBAR, SEE TABLE	4	EA								5				
#30405	#3 REBAR X 4'-5" LONG	14	EA	#80006	#8 REBAR X 0'-6" LONG	20	EA												
MARK	DESCRIPTION	QTY.	UOM	MARK	DESCRIPTION	QTY.	UOM	MARK	DESCRIPTION	QTY.	UOM				DRAWN: JOM	CHECKED: AMC	ENGR: AJC	PLOTTED: 07/24/2025	

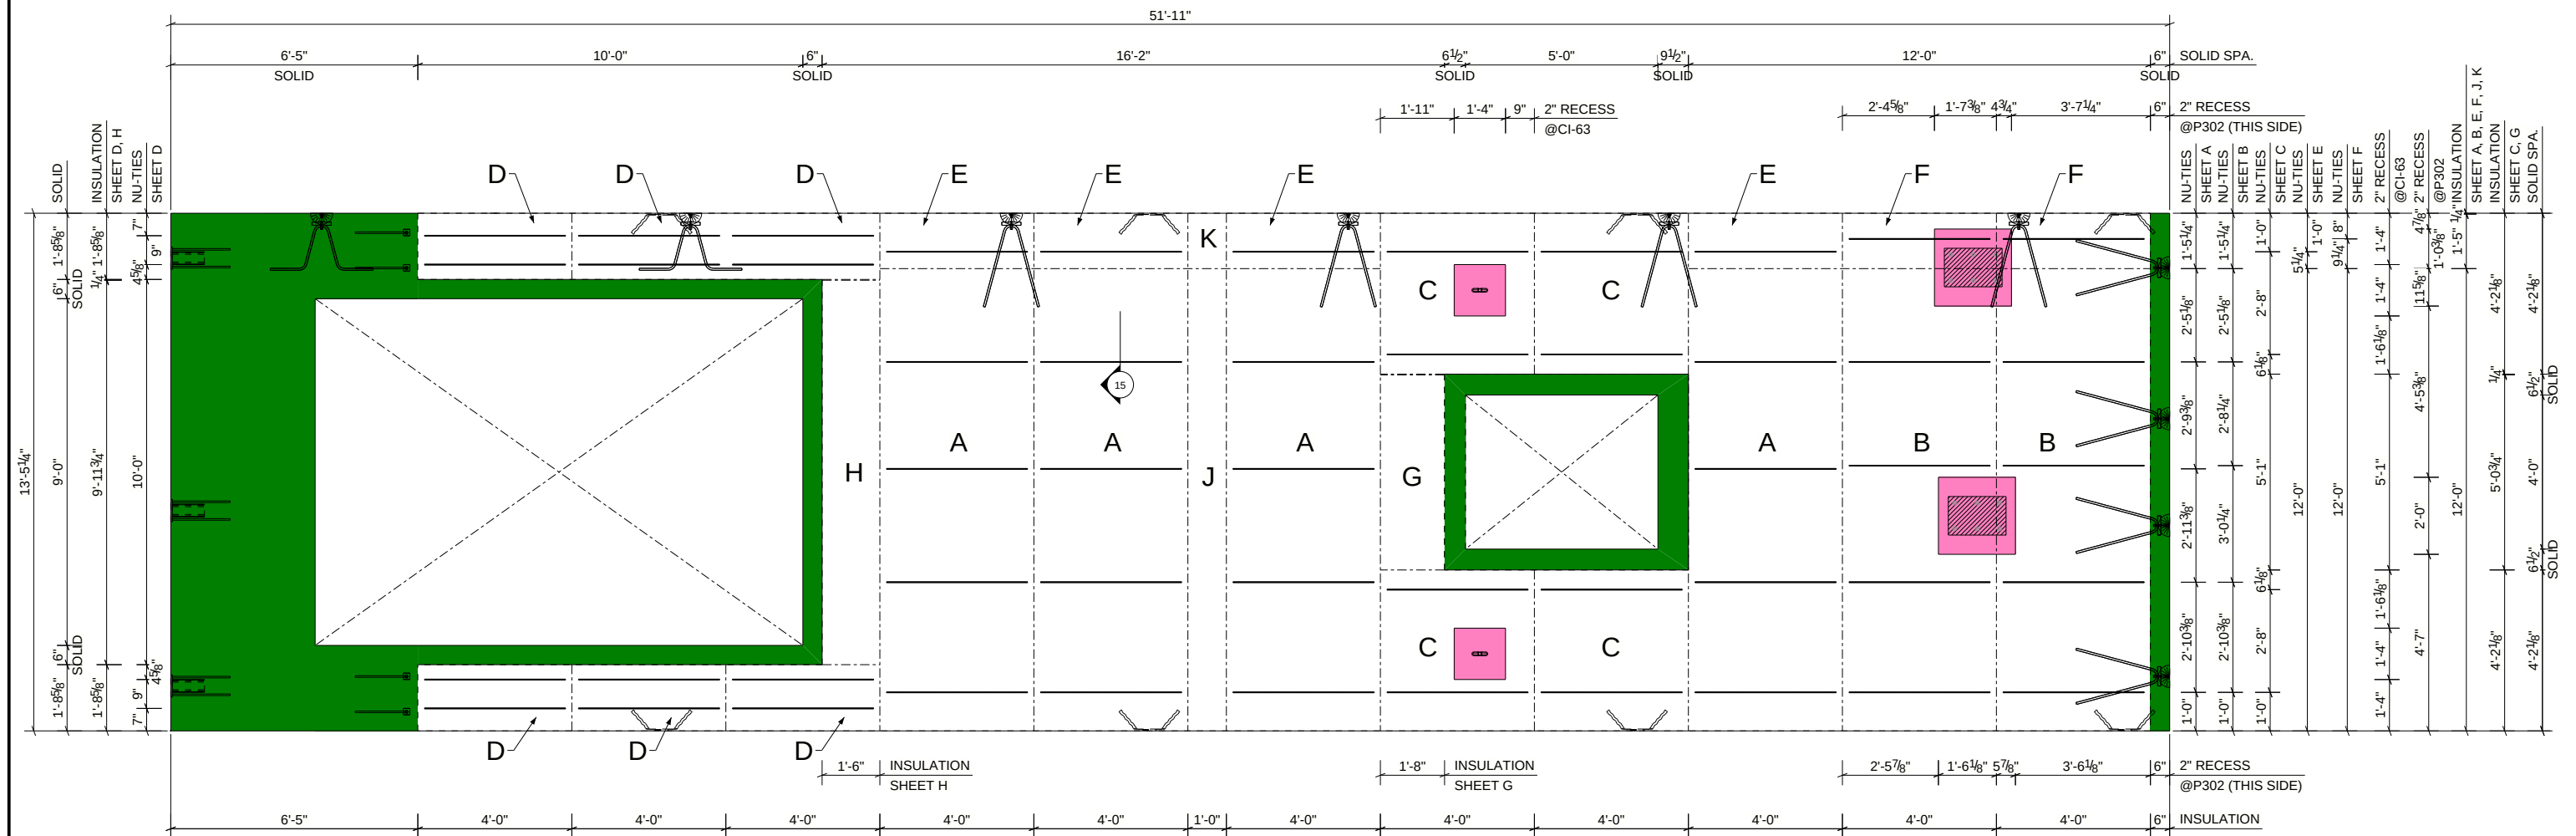

FOAM DRAWING

PIECES OF 3" 1.25# EPS:
A/B: (6) PIECES @ 4'-0" X 12'-0"
C: (4) PIECES @ 4'-0" X 4'-2 1/8"
D: (6) PIECES @ 4'-0" X 1'-8 5/8"
E/F: (6) PIECES @ 4'-0" X 1'-5"
G: (1) PIECE @ 1'-8" X 5'-0 3/4"
H: (1) PIECE @ 1'-6" X 9'-11 3/4"
J: (1) PIECE @ 1'-0" X 12'-0"
K: (1) PIECE @ 1'-0" X 1'-5"

PIECES OF 1" 1.25# EPS:
CI-63: (2) 1'-4" X 1'-4"
P302: (2) 2'-0" X 2'-0"


NOTES:
1. ALL REBAR IS TO BE 1 1/2" CLR. UNO
2. ALL DIMENSIONS ARE TO CENTERLINE UNO
SYMBOLS
SIF = SIDE IN FORM
BIF = BOTTOM IN FORM
TIF = TOP IN FORM

REV.	DESCRIPTION	DATE	BY
0	ISSUED FOR PRODUCTION	07/01/2025	JOM
1			
2			
3			
4			
5			

DRAWN: JOM	CHECKED: AMC	ENGR: AJC	PLOTTED: 07/24/2025
---------------	-----------------	--------------	------------------------

**NORTHEAST
PRECAST**
4081 S. LINCOLN AVE
VINELAND, NJ 08361
OFFICE: 866-699-2557 FAX: 856-765-9087
www.northeastprecast.com

PROJECT: NEWBURGH SOUTH LOGISTICS CENTER	PIECE MARK: W109	SHEET NO.: 2 OF 3
---	---------------------	----------------------

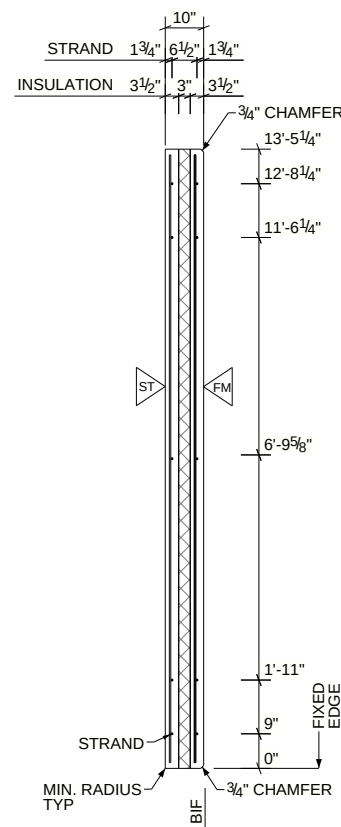

REVEAL DRAWING



REV.	DESCRIPTION	DATE	BY
0	ISSUED FOR PRODUCTION	07/01/2025	JOM
1			
2			
3			
4			
5			

DRAWN: JOM	CHECKED: AMC	ENGR: AJC	PLOTTED: 07/24/2025
---------------	-----------------	--------------	------------------------

PROJECT: NEWBURGH SOUTH LOGISTICS CENTER		
JOB NO. 25-NE1212	PIECE MARK W109	SHEET NO. 3 OF 3