




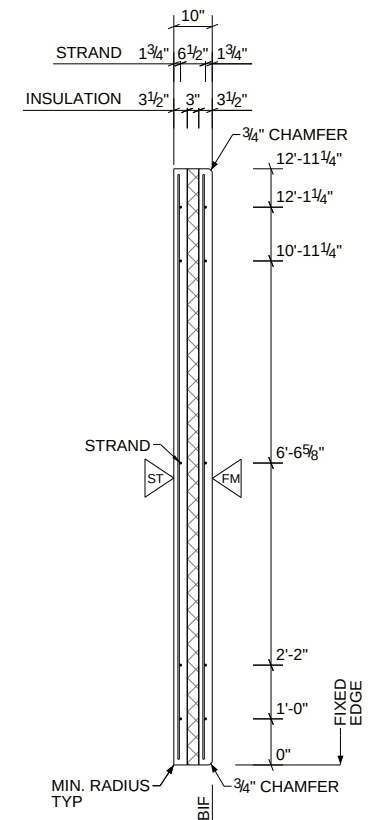

SECTION VIEW

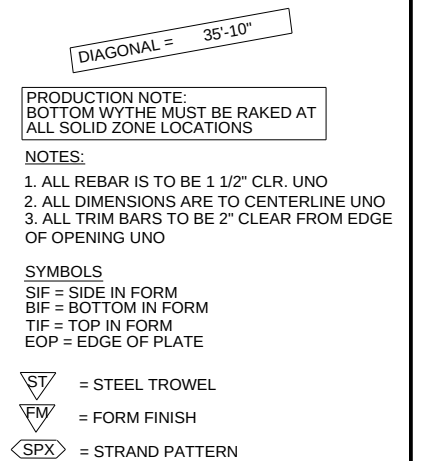

SECTION VIEW

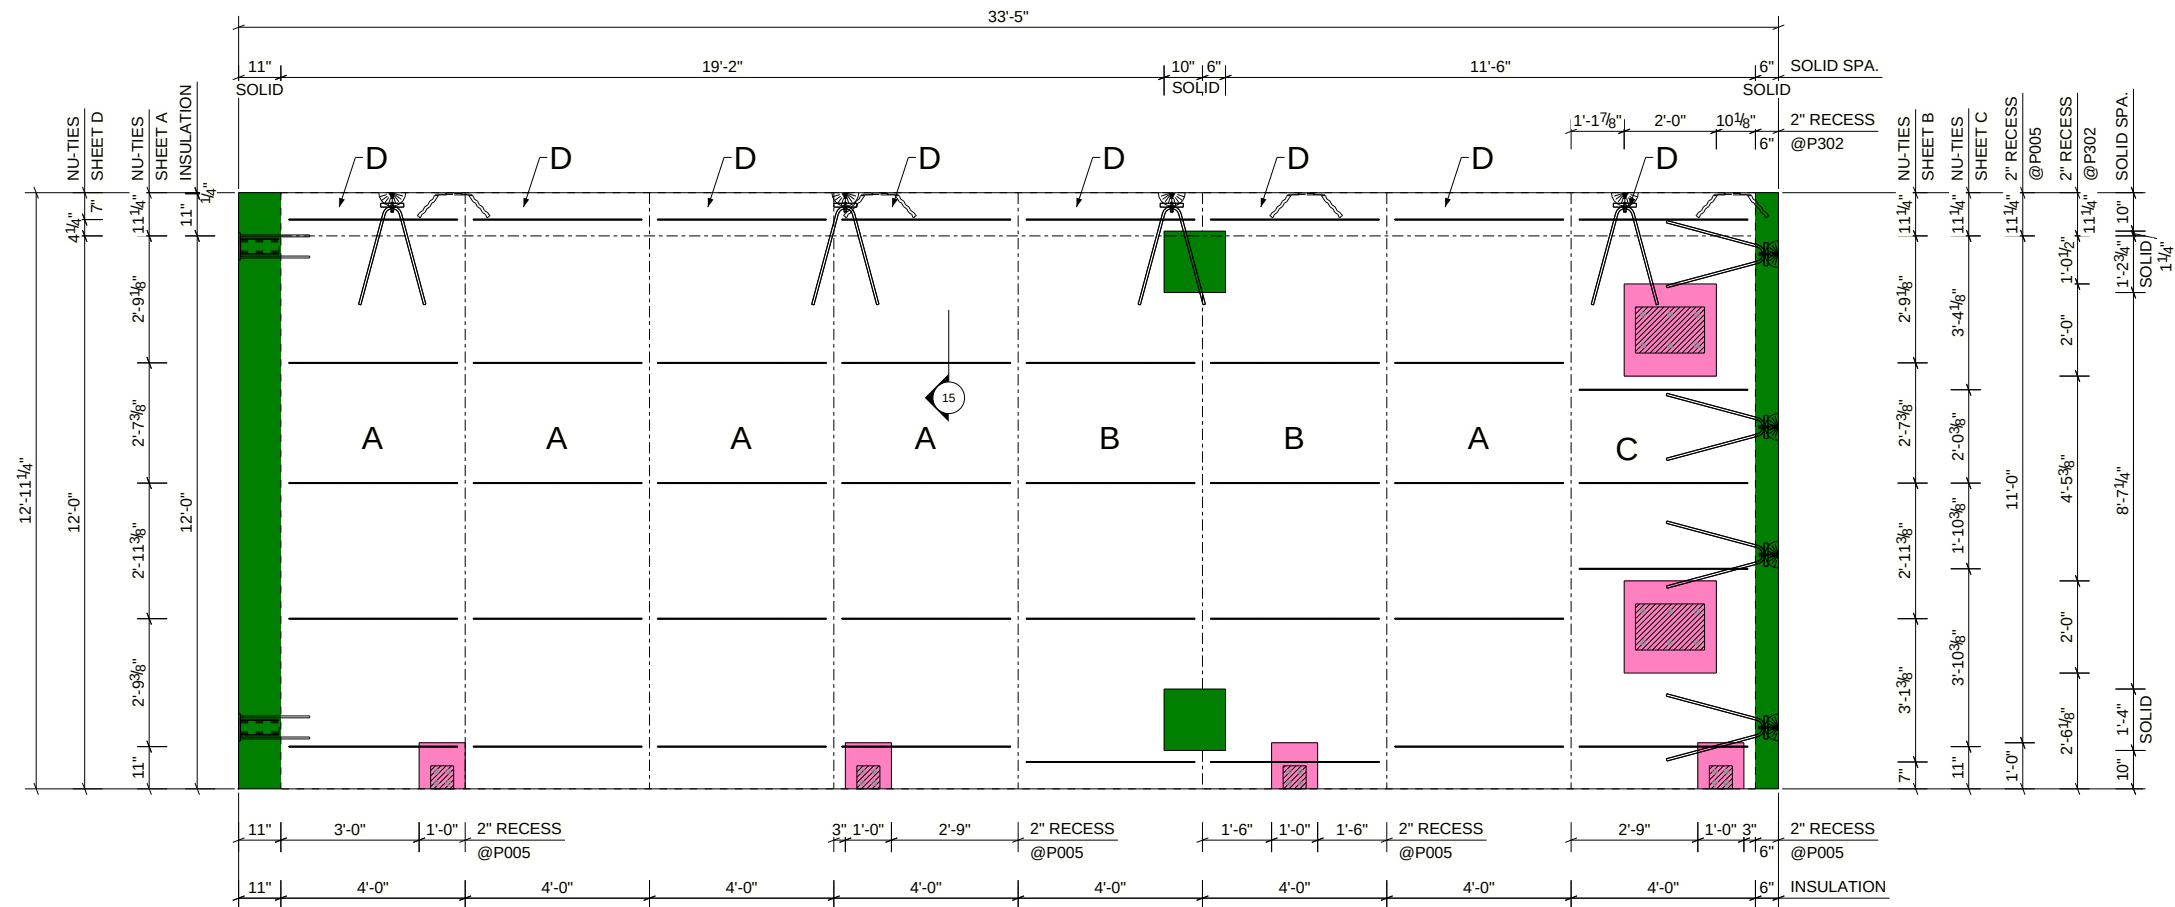

FOAM DRAWING

PIECES OF 3" 1.25# EPS:
A/B/C: (8) PIECES @ 4'-0" X 12'-0"
D: (8) PIECES @ 4'-0" X 0'-11"

PIECES OF 1" 1.25# EPS:
P005: (4) 1'-0" X 1'-0"
P302: (2) 2'-0" X 2'-0"

NOTES:

1. ALL REBAR IS TO BE 1 1/2" CLR. UNO
 2. ALL DIMENSIONS ARE TO CENTERLINE UNO
- SYMBOLS
SIF = SIDE IN FORM
BIF = BOTTOM IN FORM
TIF = TOP IN FORM


REV.	DESCRIPTION	DATE	BY
0	ISSUED FOR PRODUCTION	07/01/2025	JOM
1			
2			
3			
4			
5			

DRAWN: JOM	CHECKED: AMC	ENGR: AJC	PLOTTED: 08/05/2025
---------------	-----------------	--------------	------------------------


**NORTHEAST
PRECAST**
4081 S. LINCOLN AVE
VINELAND, NJ 08361
OFFICE: 866-699-2557 FAX: 856-765-9087
www.northeastprecast.com

PROJECT:
NEWBURGH SOUTH LOGISTICS CE***


JOB NO. 25-NE1212	PIECE MARK W218	SHEET NO. 2 OF 3
----------------------	---------------------------	---------------------

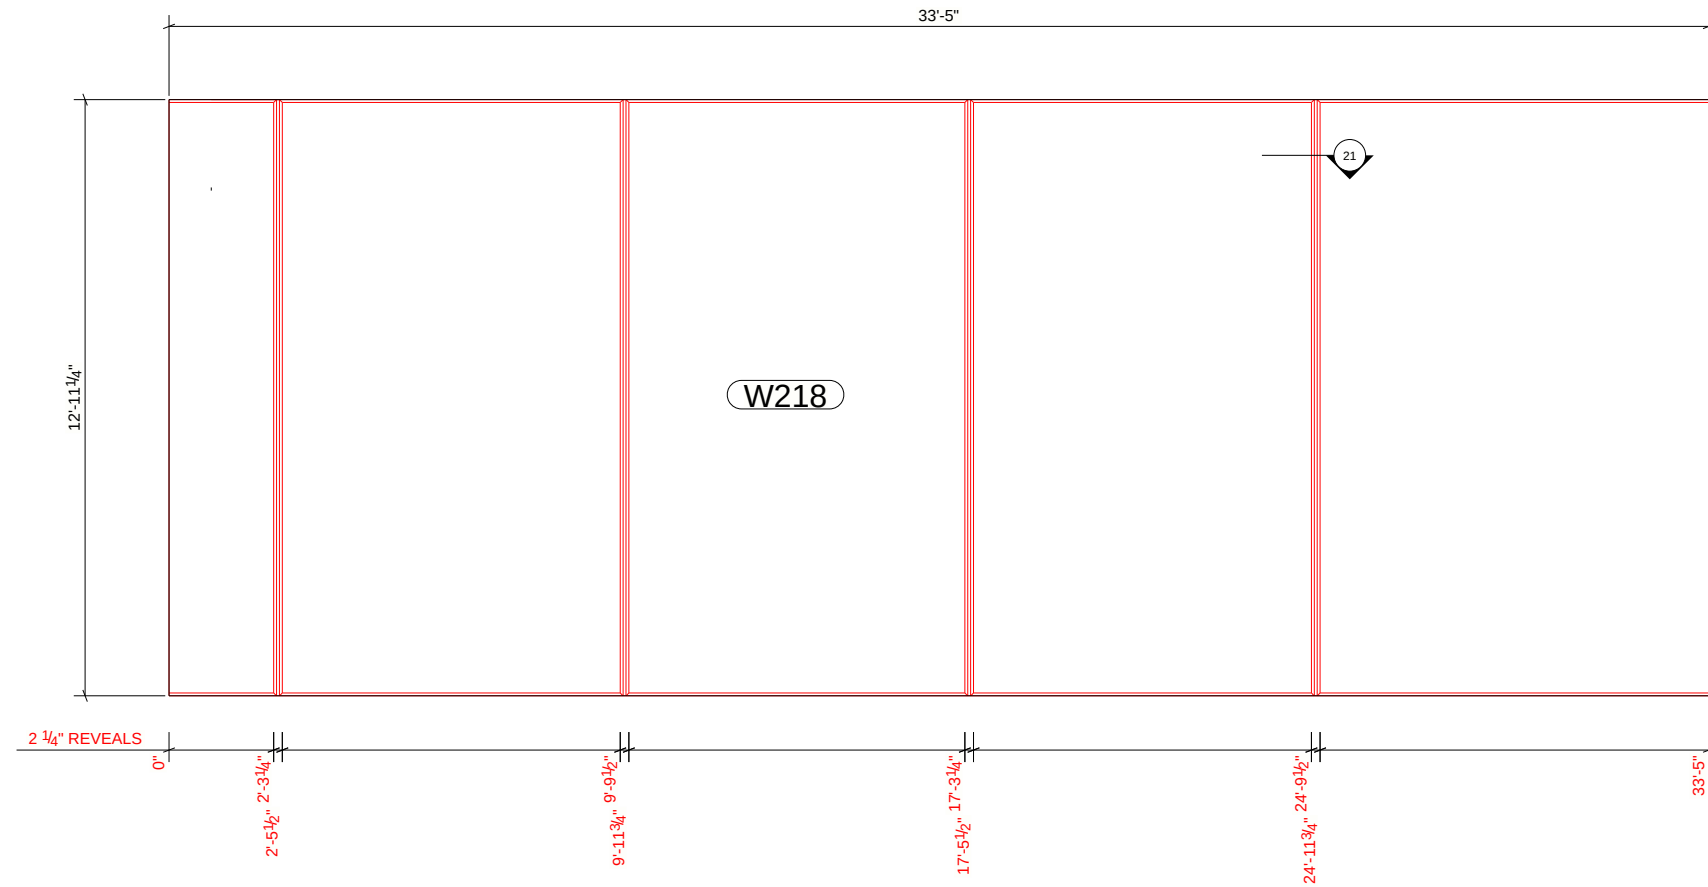

REVEAL DRAWING

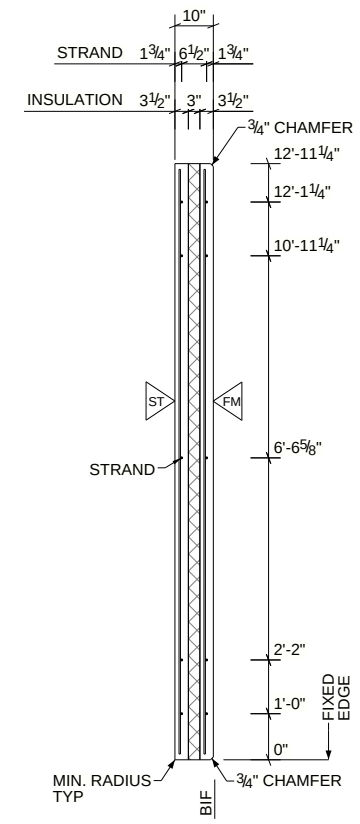

SECTION VIEW

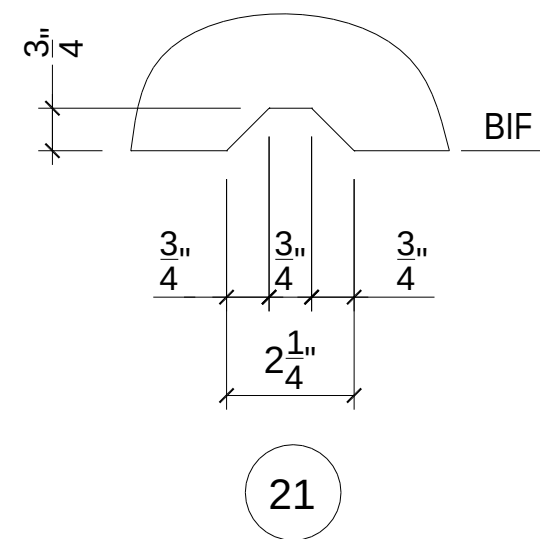

- NOTES:
- 1. ALL REBAR IS TO BE 1 1/2" CLR. UNO
 - 2. ALL DIMENSIONS ARE TO CENTERLINE UNO
- SYMBOLS
- SIF = SIDE IN FORM
 - BIF = BOTTOM IN FORM
 - TIF = TOP IN FORM

REV.	DESCRIPTION	DATE	BY
0	ISSUED FOR PRODUCTION	07/01/2025	JOM
1			
2			
3			
4			
5			

DRAWN: JOM	CHECKED: AMC	ENGR: AJC	PLOTTED: 08/05/2025
---------------	-----------------	--------------	------------------------

**NORTHEAST
PRECAST**

4081 S. LINCOLN AVE
VINELAND, NJ 08361
OFFICE: 866-699-2557 FAX: 856-765-9087
www.northeastprecast.com

PROJECT:
NEWBURGH SOUTH LOGISTICS CE***

JOB NO. 25-NE1212	PIECE MARK W218	SHEET NO. 3 OF 3
----------------------	--------------------	---------------------