




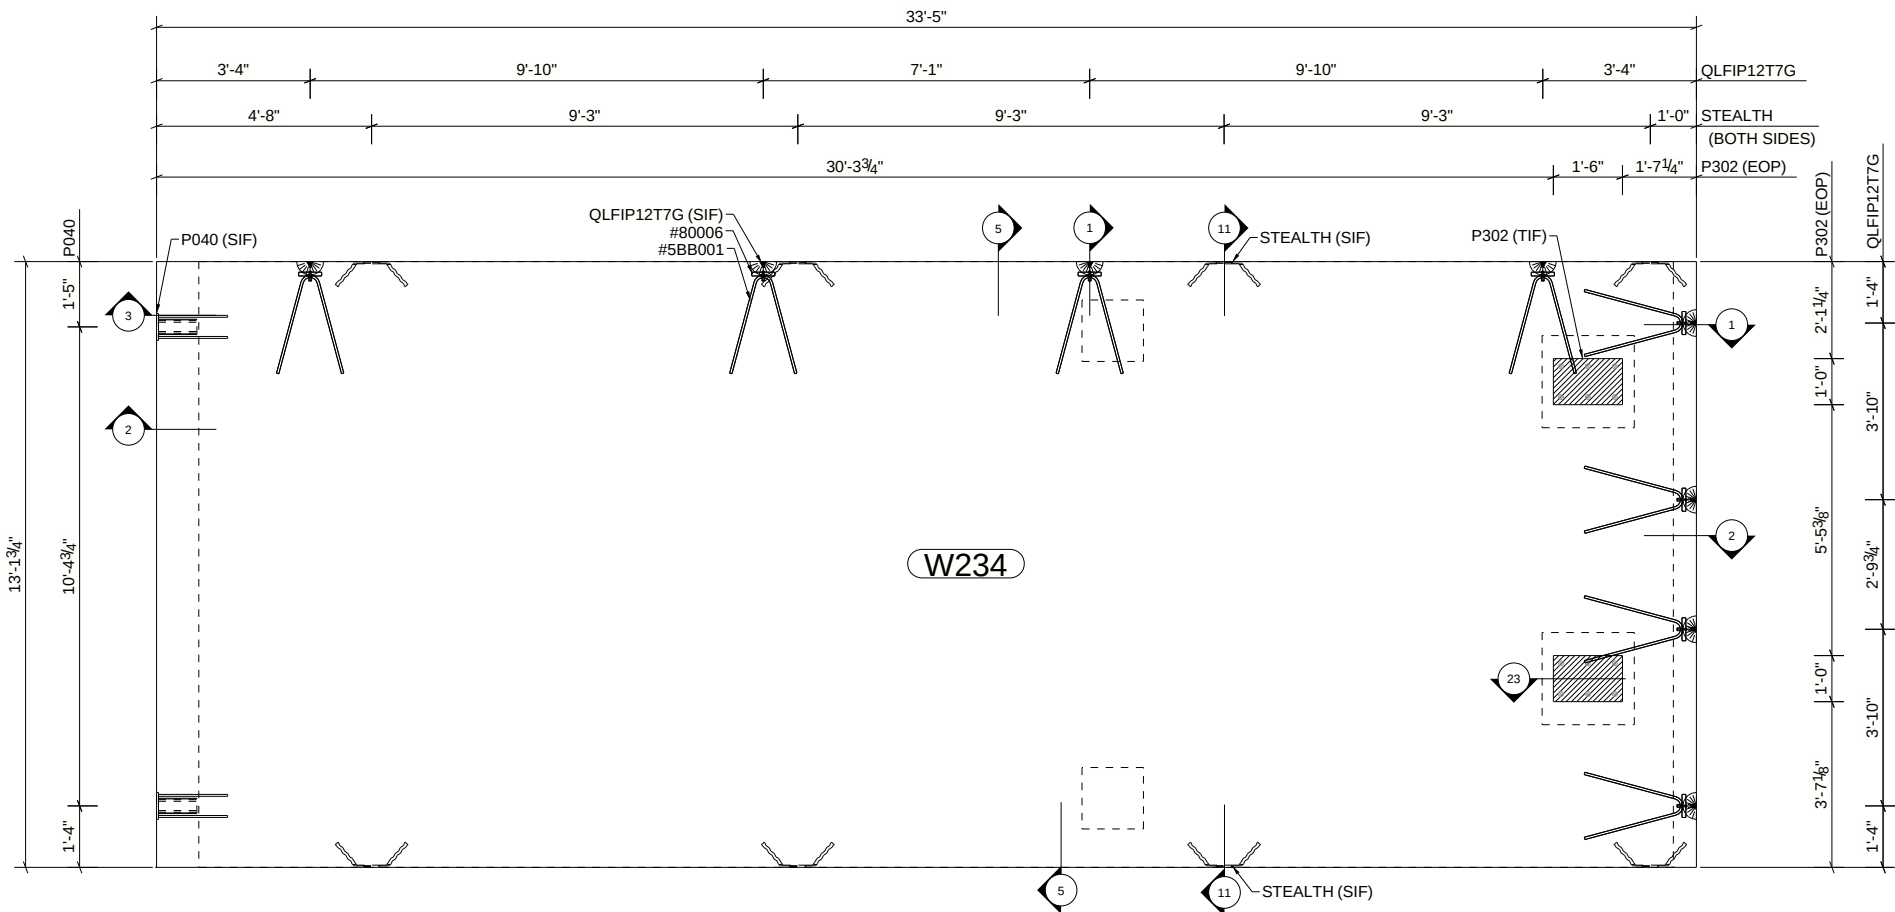

FORM VIEW

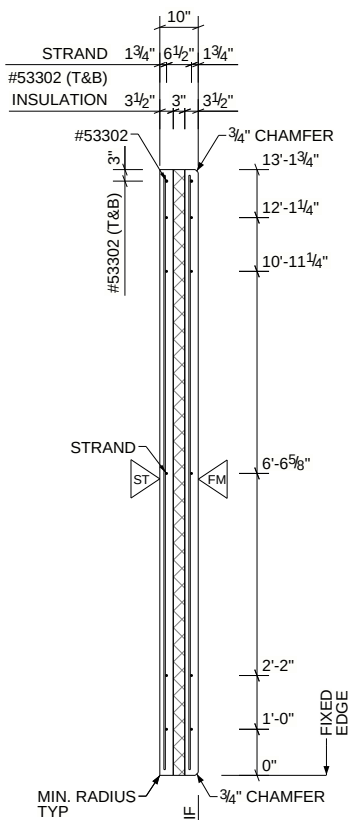

SECTION VIEW

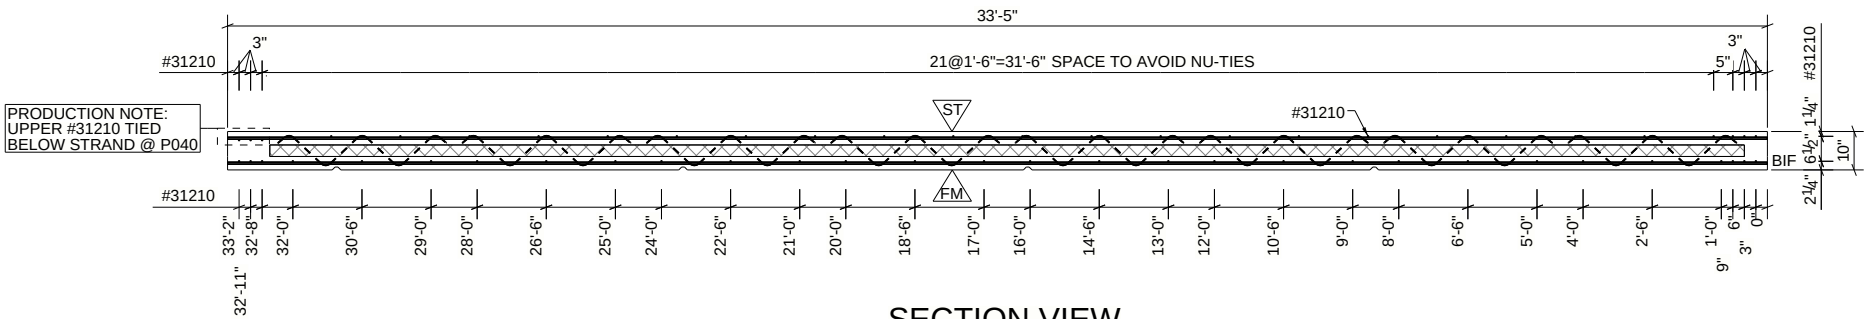

SECTION VIEW

DIAGONAL = 35'-10 15/16"

PRODUCTION NOTE:
BOTTOM WYTIE MUST BE RAKED AT
ALL SOLID ZONE LOCATIONS

- NOTES:
1. ALL REBAR IS TO BE 1 1/2" CLR. UNO
 2. ALL DIMENSIONS ARE TO CENTERLINE UNO
 3. ALL TRIM BARS TO BE 2" CLEAR FROM EDGE OF OPENING UNO

SYMBOLS
SIF = SIDE IN FORM
BIF = BOTTOM IN FORM
TIF = TOP IN FORM
EOP = EDGE OF PLATE

ST = STEEL TROWEL
FM = FORM FINISH
SPX = STRAND PATTERN

MARK	DESCRIPTION	QTY.	UOM
NU-TIE	7" NU-TIE	40	EA
P040	PL3/4X4X0'-7" W/ (2) #4 X 1'-6"	2	EA
P302	PL1/2X1'-0"X1'-6" W/ (6) 5/8" DIA X 4 1/8 LONG HCA	2	EA
QLFI12T7G	12T SAND PANEL ANCHOR	8	EA
STEALTH	STEALTH 100 FLANGE CONNECTOR	8	EA
#31210	#3 REBAR X 12'-10" LONG	57	EA
#53302	#5 REBAR X 33'-2" LONG	2	EA
#5BB001	#5 BENT REBAR, SEE TABLE	16	EA
#80006	#8 REBAR X 0'-6" LONG	16	EA

MARK	DESCRIPTION	QTY.	UOM
1/2 STRAND	1/2 DIAMETER STRAND 28.90 Kips	10	EA


MARK	DESCRIPTION	QTY.	UOM
------	-------------	------	-----

MIX	CY	B/F
725N	5.00	B
700A	4.75	F

PIECES REQ'D: 1
WEIGHT: 39613 LBS
DESIGN: <SP2>
CONTROL NO.: 234

REV.	DESCRIPTION	DATE	BY
0	ISSUED FOR PRODUCTION	07/01/2025	JOM
1			
2			
3			
4			
5			

NORTHEAST PRECAST		
4091 S. LINCOLN AVE VINELAND, NJ 08361 OFFICE: 866-699-2557 FAX: 856-765-9087 www.northeastprecast.com		
PROJECT: NEWBURGH SOUTH LOGISTICS CENTER	PIECE MARK: W234	SHEET NO.: 1 OF 3

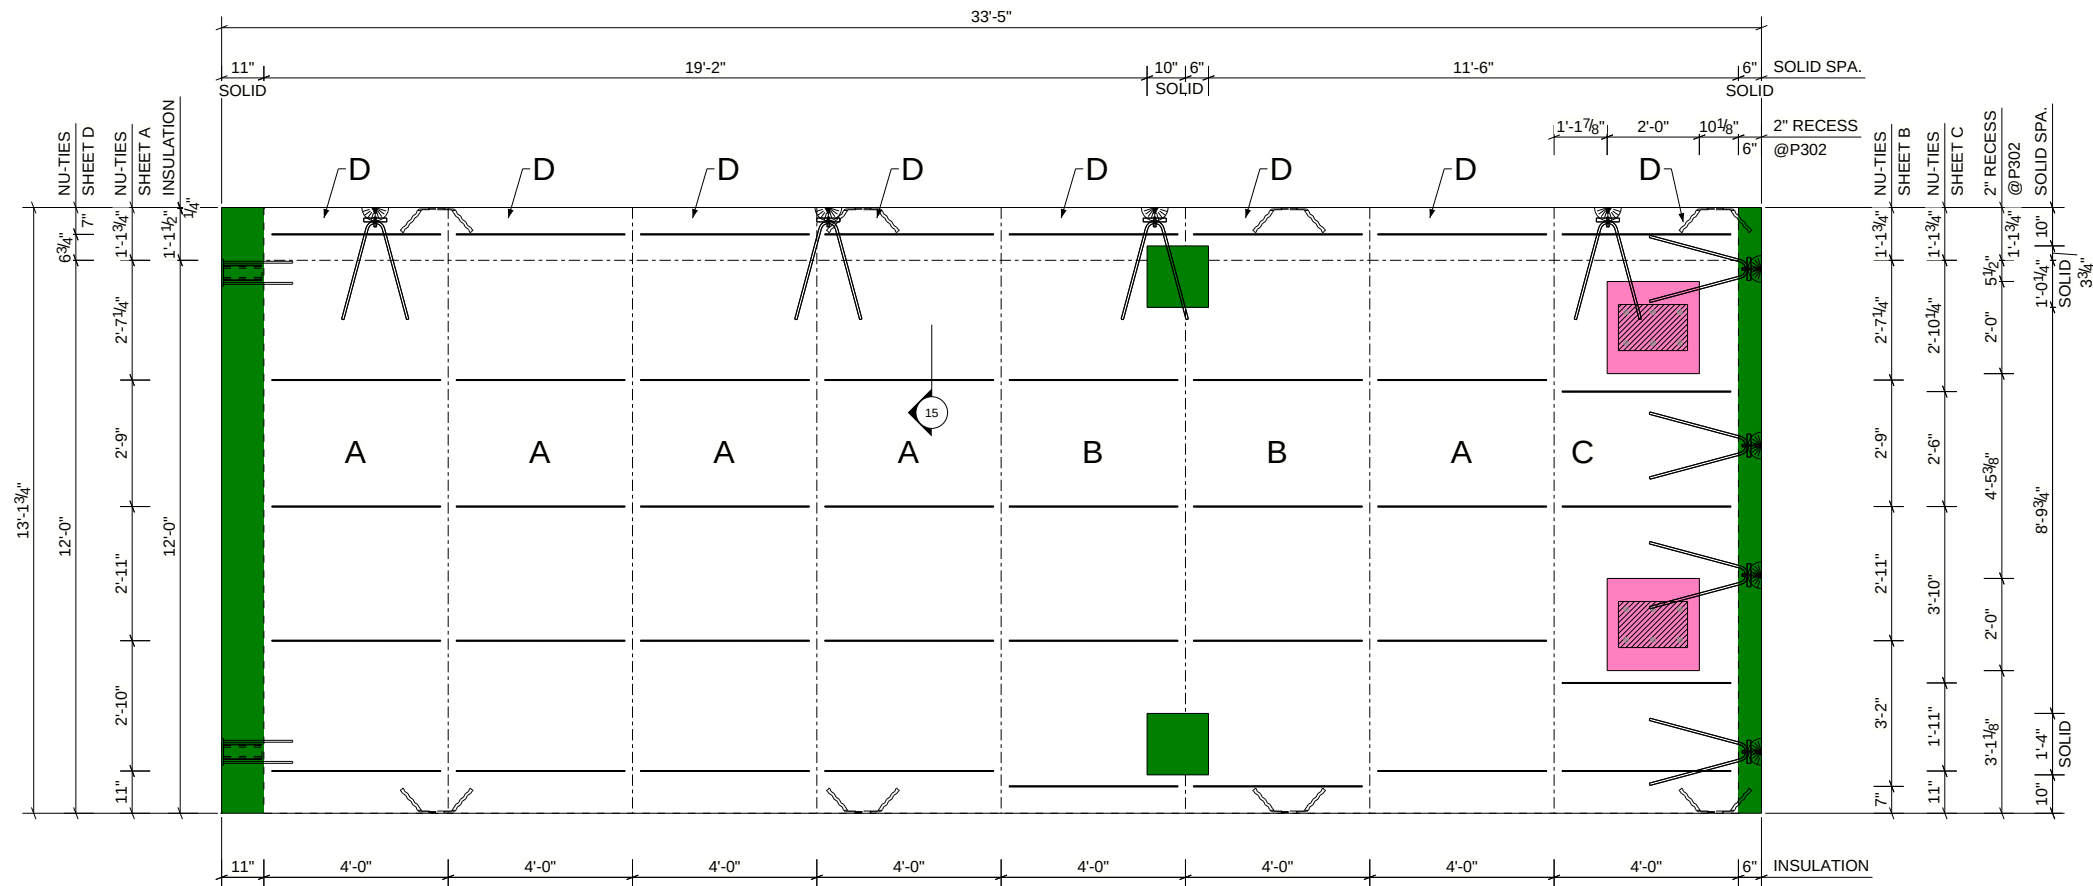

FOAM DRAWING

PIECES OF 3" 1.25# EPS:
A/B/C: (8) PIECES @ 4'-0" X 12'-0"
D: (8) PIECES @ 4'-0" X 1'-1 1/2"

PIECES OF 1" 1.25# EPS:
P302: (2) 2'-0" X 2'-0"


- NOTES:
- 1. ALL REBAR IS TO BE 1 1/2" CLR. UNO
 - 2. ALL DIMENSIONS ARE TO CENTERLINE UNO
- SYMBOLS
SIF = SIDE IN FORM
BIF = BOTTOM IN FORM
TIF = TOP IN FORM

REV.	DESCRIPTION	DATE	BY
0	ISSUED FOR PRODUCTION	07/01/2025	JOM
1			
2			
3			
4			
5			

DRAWN: JOM	CHECKED: AMC	ENGR: AJC	PLOTTED: 08/04/2025
---------------	-----------------	--------------	------------------------

**NORTHEAST
PRECAST**
4081 S. LINCOLN AVE
VINELAND, NJ 08361
OFFICE: 866-699-2557 FAX: 856-765-9087
www.northeastprecast.com

PROJECT: NEWBURGH SOUTH LOGISTICS CE***	PIECE MARK: W234	SHEET NO.: 2 OF 3
--	---------------------	----------------------

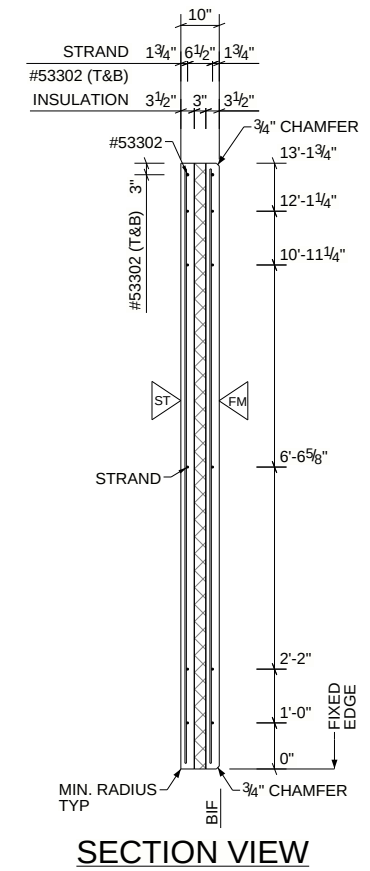

SECTION VIEW

