




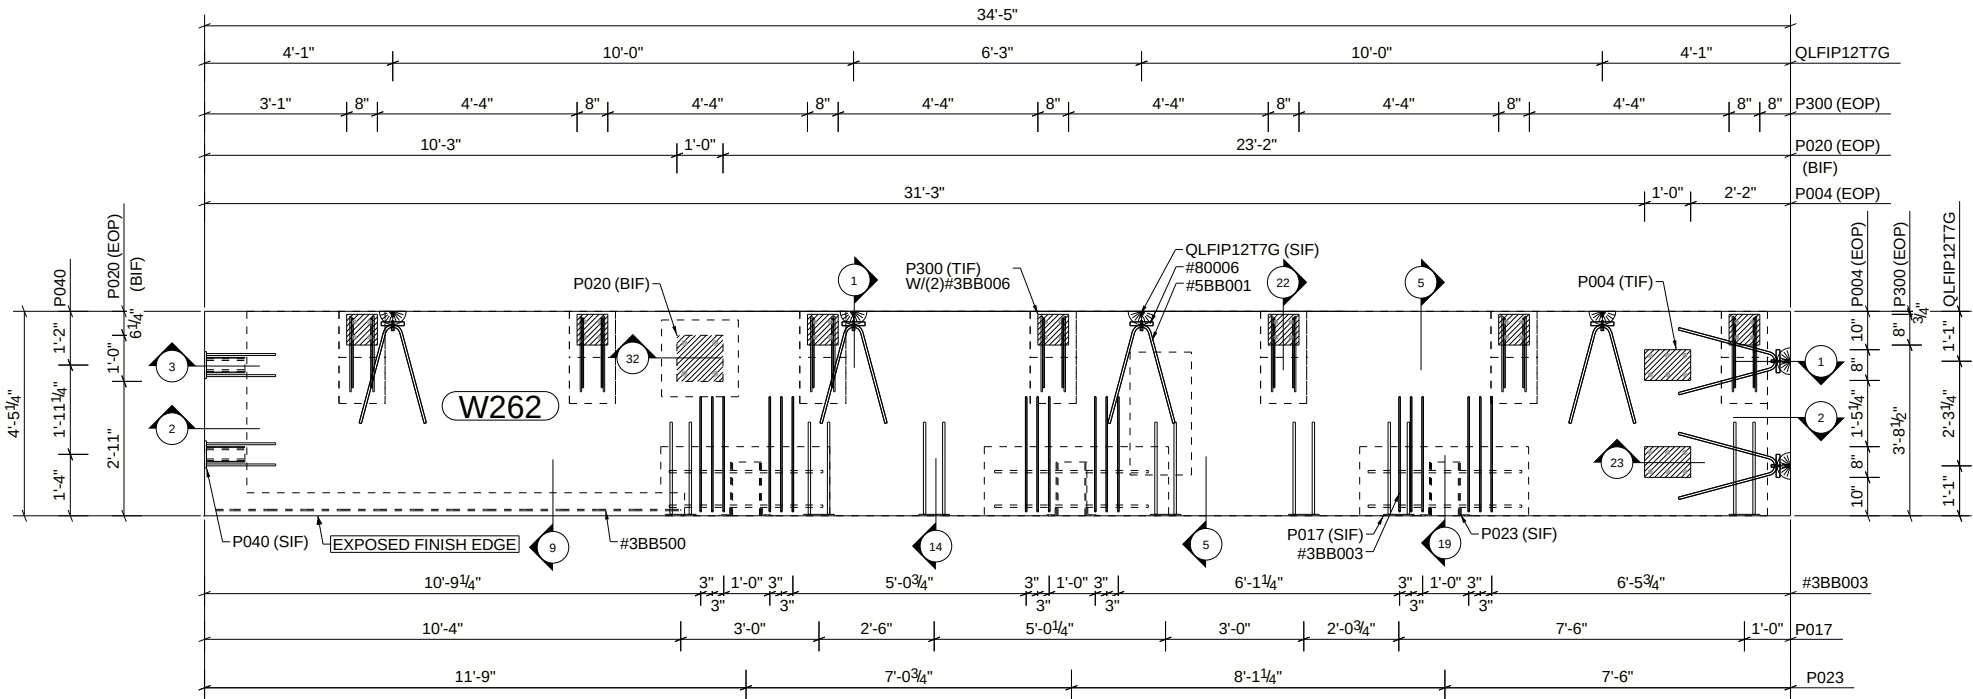

FORM VIEW

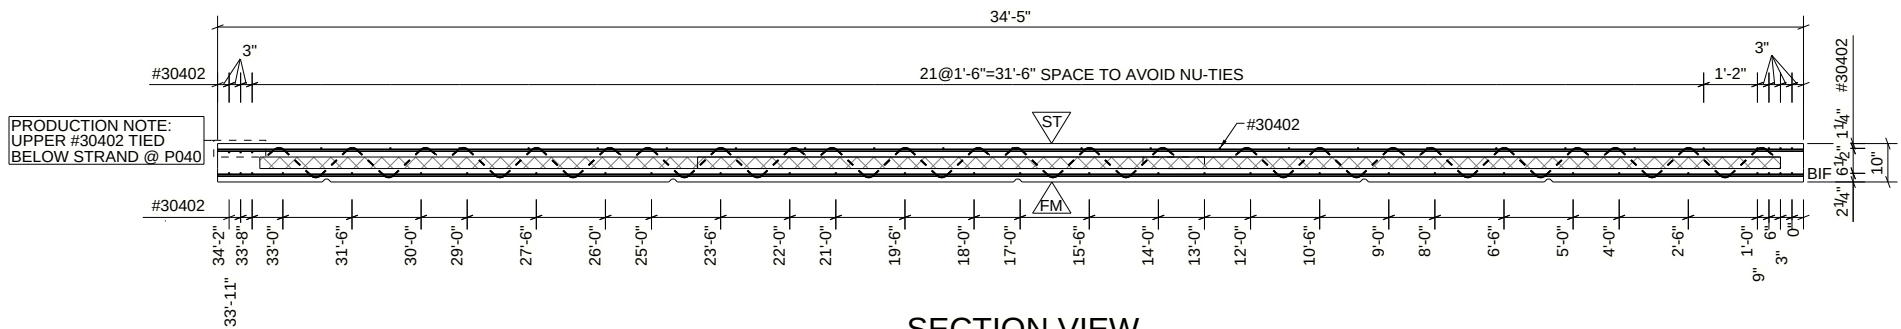

SECTION VIEW

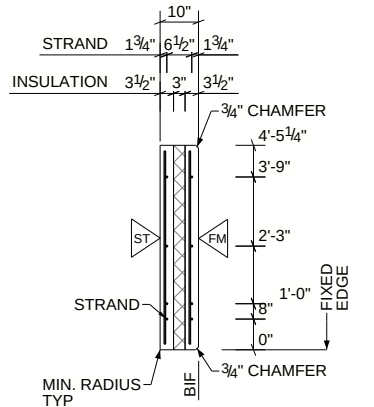

SECTION VIEW

DIAGONAL = 34'-8 7/16"

PRODUCTION NOTE:
BOTTOM WYTHE MUST BE RAKED AT
ALL SOLID ZONE LOCATIONS

- NOTES:
1. ALL REBAR IS TO BE 1 1/2" CLR. UNO
 2. ALL DIMENSIONS ARE TO CENTERLINE UNO
 3. ALL TRIM BARS TO BE 2" CLEAR FROM EDGE OF OPENING UNO

SYMBOLS
SIF = SIDE IN FORM
BIF = BOTTOM IN FORM
TIF = TOP IN FORM
EOP = EDGE OF PLATE

ST = STEEL TROWEL
FM = FORM FINISH
SPX = STRAND PATTERN

NU-TIE	7" NU-TIE	24	EA
P004	PL3/8X8X1'-0" W/ (6) 1/2" DIA X 2 5/8" HCA	2	EA
P017	PL3/8X3X0'-8" W/ (2) #5 X 2'-0"	7	EA
P020	PL3/8X12X1'-0" W/ (4) 5/8" DIA X 4 1/8" HCA	1	EA
P023	HSS 8"x4"x1/4"x1'-2" W/ END PL & (4) #4 BARS	3	EA
P040	PL3/4X4X0'-7" W/ (2) #4 X 1'-6"	2	EA
P300	PL3/8X8X8 W/ (4) 1/2" DIA X 6" LONG HCA & (2) #4 BARS	7	EA
QLFIP12T7G	12T SAND PANEL ANCHOR	6	EA
#30402	#3 REBAR X 4'-2" LONG	59	EA
MARK	DESCRIPTION	QTY.	UOM

#3BB003	#3 BENT REBAR, SEE TABLE	18	EA
#3BB006	#3 BENT REBAR, SEE TABLE	14	EA
#3BB500	#3 BENT REBAR, SEE TABLE	1	EA
#5BB001	#5 BENT REBAR, SEE TABLE	12	EA
#80006	#8 REBAR X 0'-6" LONG	12	EA
1/2 STRAND	1/2 DIAMETER STRAND 28.90 Kips	8	EA
MARK	DESCRIPTION	QTY.	UOM

MARK	DESCRIPTION	QTY.	UOM
------	-------------	------	-----

MIX	CY	B/F
725N	2.06	B
700A	1.65	F
F _c (28 DAYS)		
6000 PSI		
F _c (SHIPPING)		
4000 PSI		
F _t (RELEASE)		
3500 PSI		


PIECES REQ'D:	1
WEIGHT:	15263 LBS
DESIGN:	SP5
CONTROL NO.:	262

REV.	DESCRIPTION	DATE	BY
0	ISSUED FOR PRODUCTION	07/01/2025	JOM
1			
2			
3			
4			
5			
DRAWN:	CHECKED:	ENGR:	PLOTTED:
JOM	AMC	AJC	08/21/2025

**NORTHEAST
PRECAST**

4081 S. LINCOLN AVE
VINELAND, NJ 08361
OFFICE: 866-699-2557 FAX: 856-765-9087
www.northeastprecast.com

PROJECT:
NEWBURGH SOUTH LOGISTICS CENTER
JOB NO. 25-NE1212
PIECE MARK: W262
SHEET NO. 1 OF 3

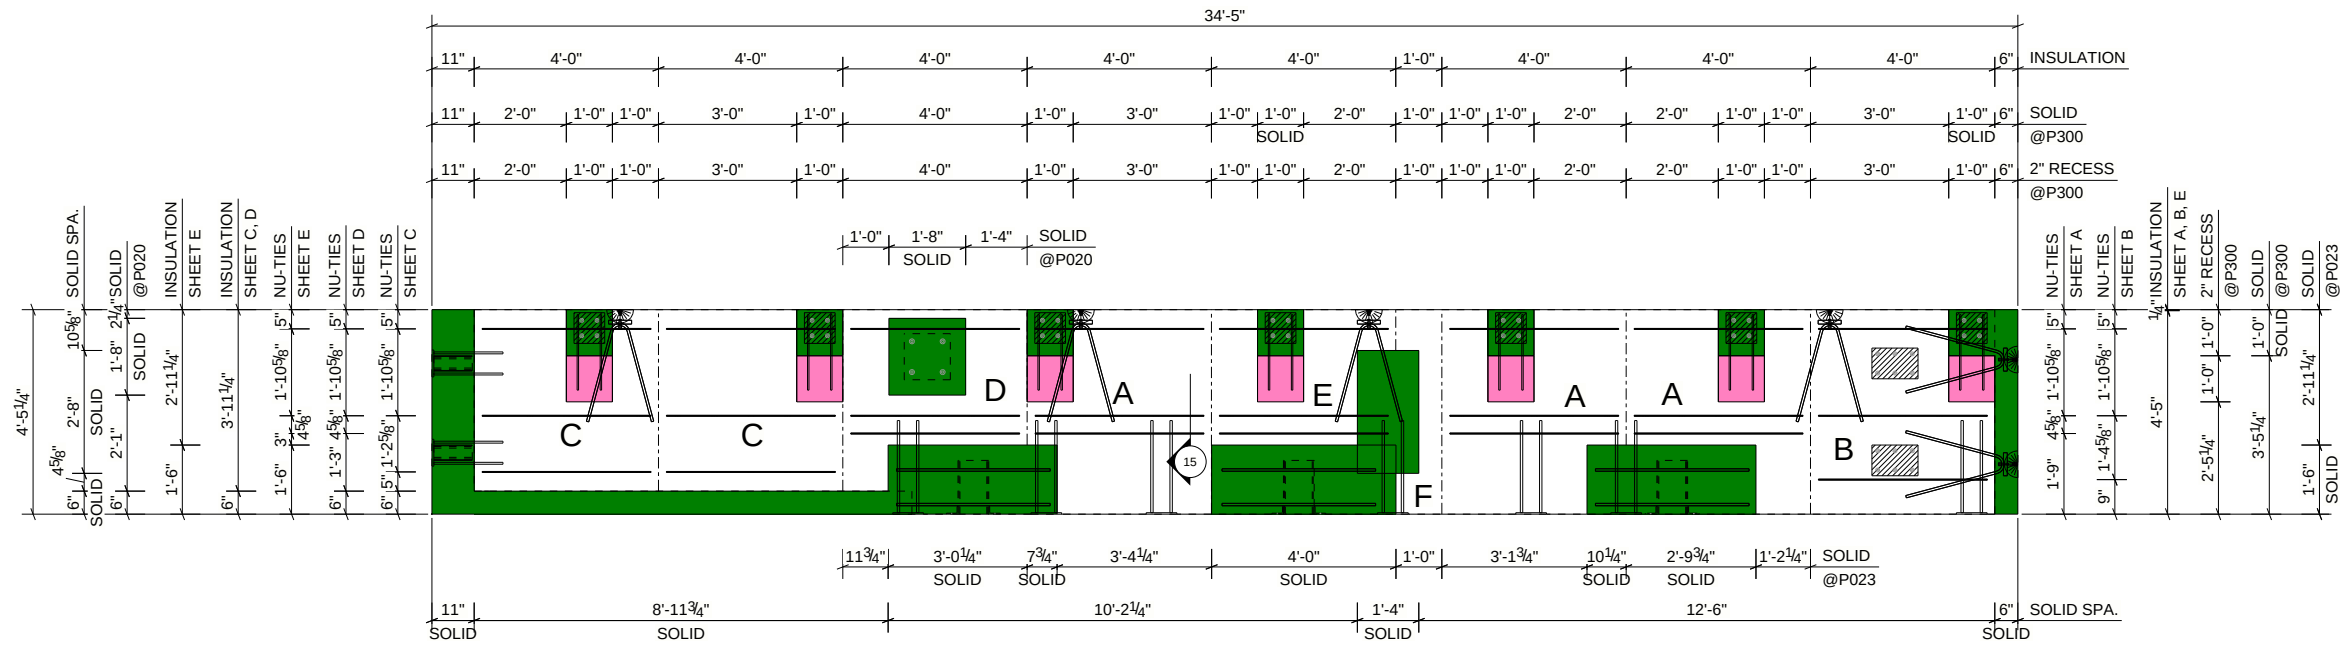

FOAM DRAWING

PIECES OF 3" 1.25# EPS:
A/B: (5) PIECES @ 4'-0" X 4'-5"
C/D: (3) PIECES @ 4'-0" X 3'-11 1/4"
E: (1) PIECE @ 4'-0" X 2'-11 1/4"
F: (1) PIECE @ 1'-0" X 4'-5"

PIECES OF 1" 1.25# EPS:
P300: (7) 1'-0" X 1'-0"


NOTES:
1. ALL REBAR IS TO BE 1 1/2" CLR. UNO
2. ALL DIMENSIONS ARE TO CENTERLINE UNO
SYMBOLS
SIF = SIDE IN FORM
BIF = BOTTOM IN FORM
TIF = TOP IN FORM

REV.	DESCRIPTION	DATE	BY
0	ISSUED FOR PRODUCTION	07/01/2025	JOM
1			
2			
3			
4			
5			


DRAWN: JOM	CHECKED: AMC	ENGR: AJC	PLOTTED: 08/21/2025
---------------	-----------------	--------------	------------------------

**NORTHEAST
PRECAST**
4081 S. LINCOLN AVE
VINELAND, NJ 08361
OFFICE: 866-699-2557 FAX: 856-765-9087
www.northeastprecast.com


PROJECT: NEWBURGH SOUTH LOGISTICS CE***	PIECE MARK: W262	SHEET NO.: 2 OF 3
--	---------------------	----------------------

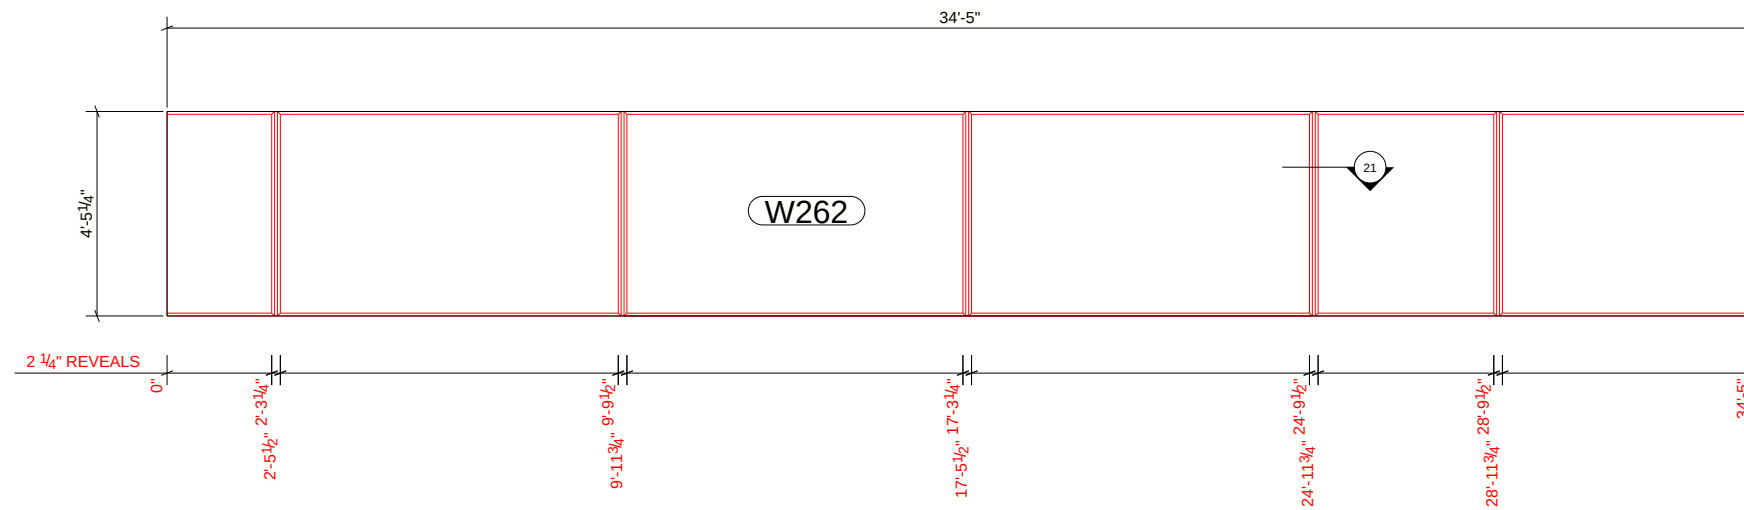

REVEAL DRAWING

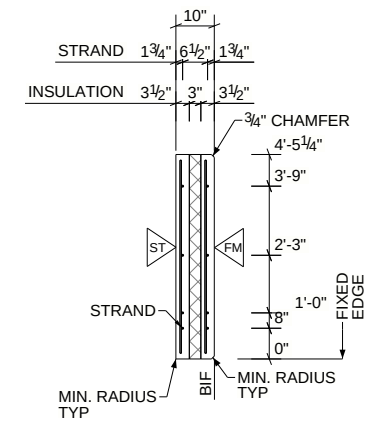

SECTION VIEW

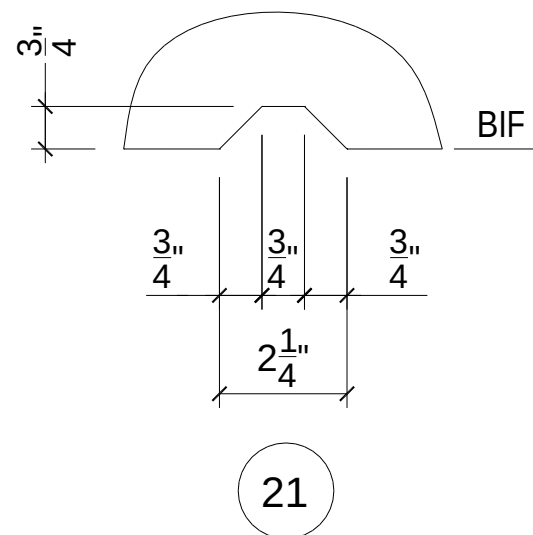

- NOTES:
1. ALL REBAR IS TO BE 1 1/2" CLR. UNO
 2. ALL DIMENSIONS ARE TO CENTERLINE UNO
- SYMBOLS
- SIF = SIDE IN FORM
- BIF = BOTTOM IN FORM
- TIF = TOP IN FORM

REV.	DESCRIPTION	DATE	BY
0	ISSUED FOR PRODUCTION	07/01/2025	JOM
1			
2			
3			
4			
5			

DRAWN: JOM	CHECKED: AMC	ENGR: AJC	PLOTTED: 08/21/2025
---------------	-----------------	--------------	------------------------

PROJECT: NEWBURGH SOUTH LOGISTICS CE***	
JOB NO. 25-NE1212	PIECE MARK W262
SHEET NO. 3 OF 3	

NORTHEAST PRECAST	
4081 S. LINCOLN AVE VINELAND, NJ 08361	
OFFICE: 866-699-2557 FAX: 856-765-9087	
www.northeastprecast.com	