



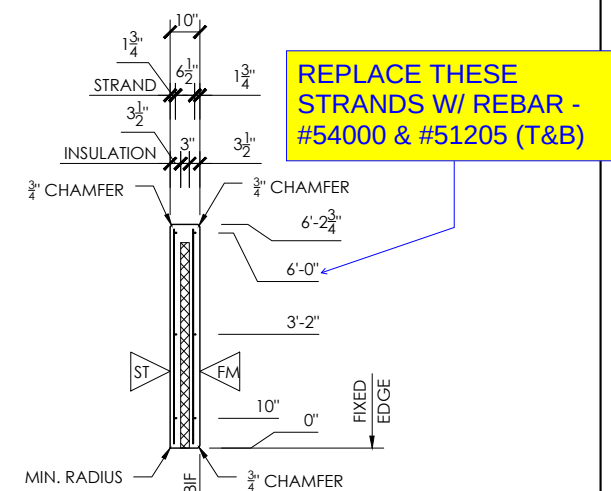

SECTION VIEW

FORM VIEW

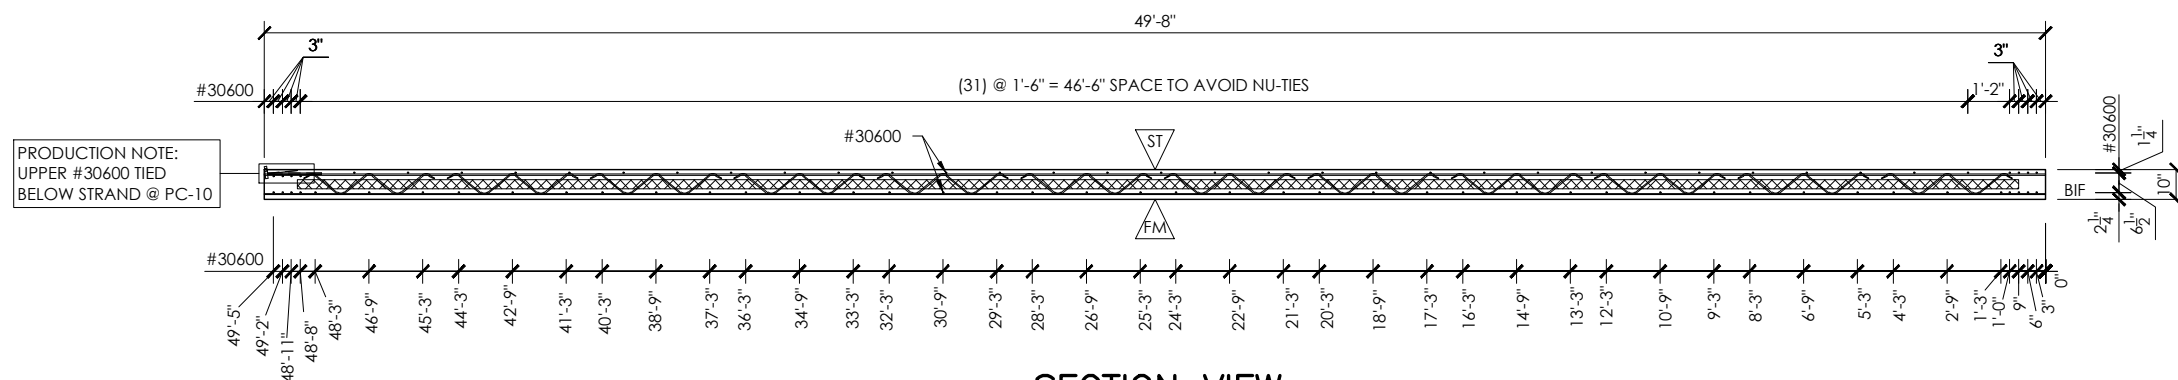

SECTION VIEW

NOTES:
1. ALL REBAR IS TO BE 1" CLR. UNO
2. ALL DIMENSIONS ARE TO CENTERLINE UNO

SYMBOLS
 S.I.F. = SIDE IN FORM
 B.I.F. = BOTTOM IN FORM
 T.I.F. = TOP IN FORM
 = STEEL TROWEL
 = FORM FINISH


92 REESE ROAD
MILLVILLE, NJ 08332
OFFICE: 866-699-2557 FAX: 856-765-9087
www.northeastprecast.com

PROJECT: HRP HUDSON BUILDING 1

JOB NO. 20-NE0881

PIECE MARK W001

SHEET NO. 1 of 3

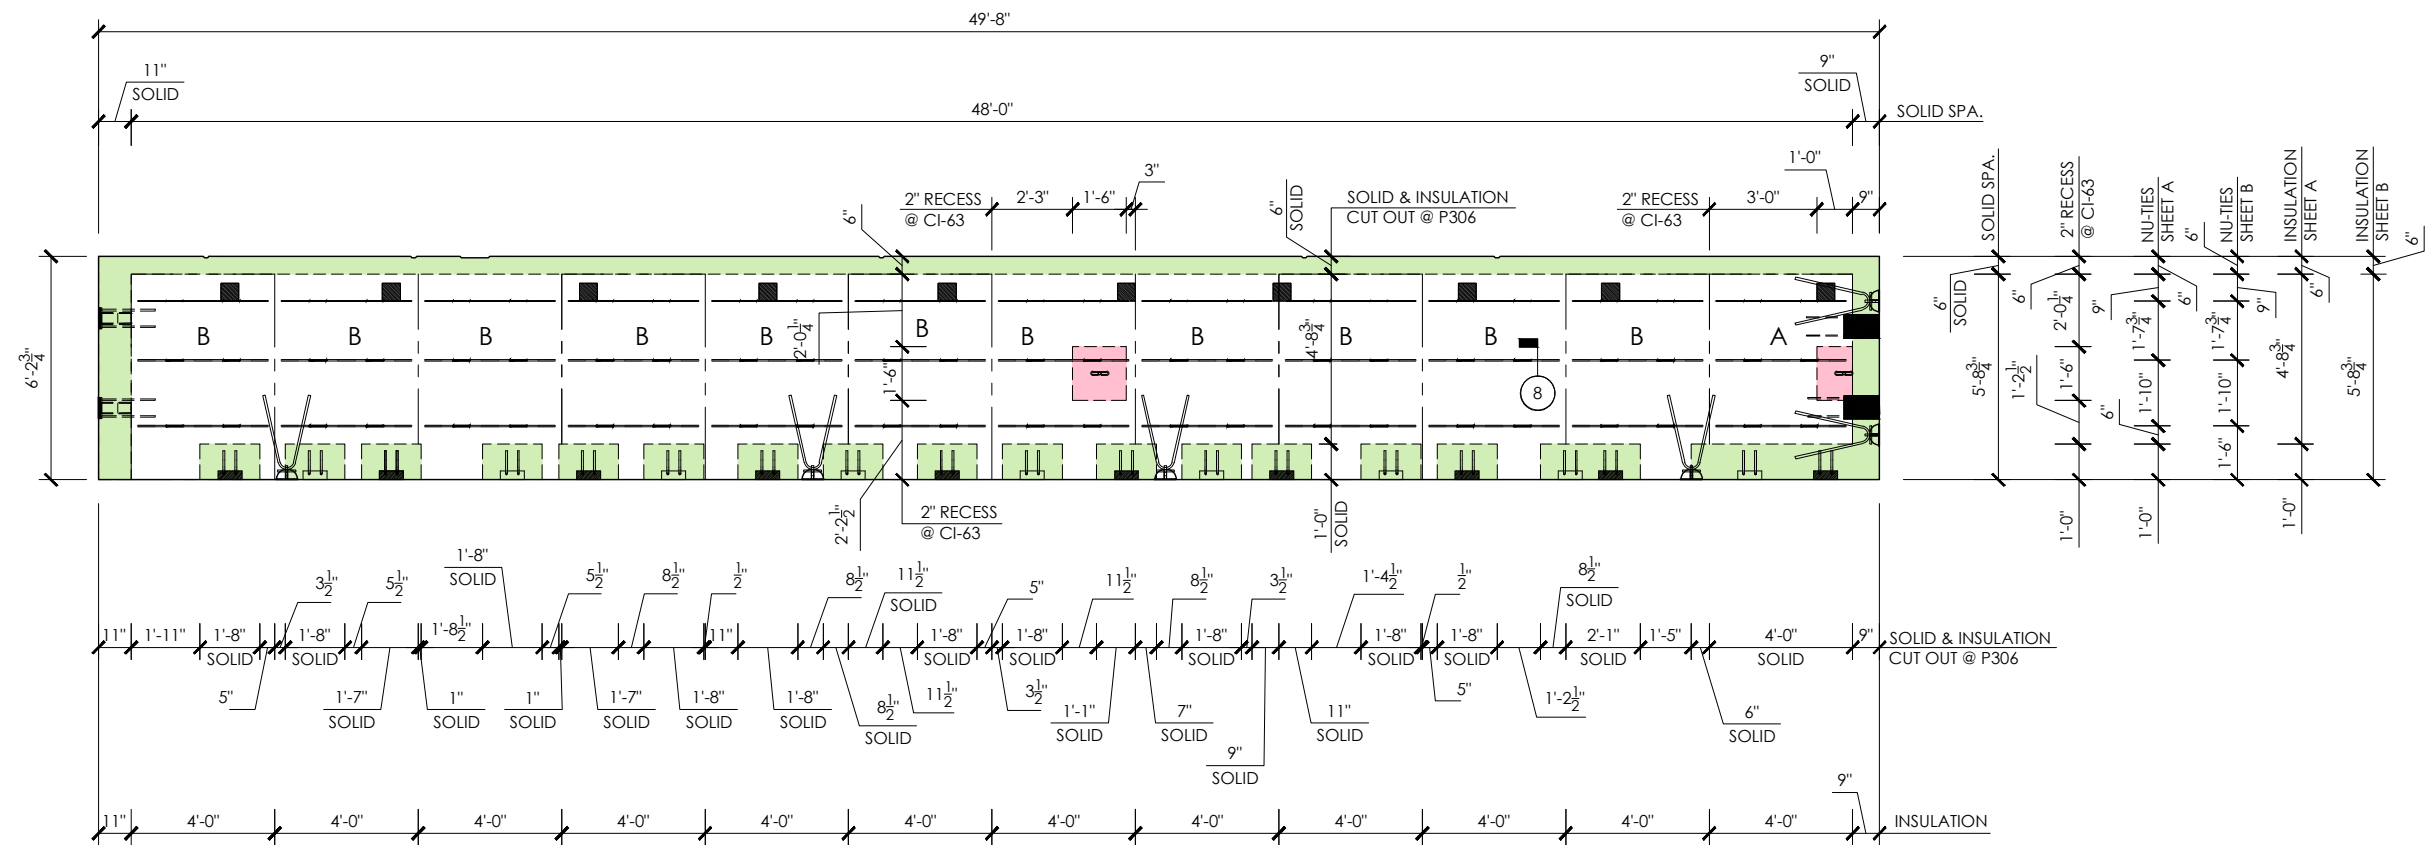

FOAM DRAWING

PIECES OF 3" XPS:

- A: (1) PIECES @ 4'-0" X 4'-8 ³/₄"
B: (11) PIECES @ 4'-0" X 5'-8 ³/₄"

- NOTES:
1. ALL REBAR IS TO BE 1" CLR. UNO
2. ALL DIMENSIONS ARE TO CENTERLINE UNO SYMBOLS
S.I.F. = SIDE IN FORM
B.I.F. = BOTTOM IN FORM
T.I.F. = TOP IN FORM

REL.	DESCRIPTION	DATE	BY
1	FOR PRODUCTION	09/28/2021	BM

DRAWN: OSJ	CHECKED: BM	ENGR: LMB	PLOTTED: 09/24/2021
------------	-------------	-----------	---------------------



NORTHEAST PRECAST
92 REESE ROAD
MILLVILLE, NJ 08332
OFFICE: 866-699-2557 FAX: 856-765-9087
www.northeastprecast.com

PROJECT: HRP HUDSON BUILDING 1

JOB NO. 20-NE0881

PIECE MARK: W001

SHEET NO. 2 of 3

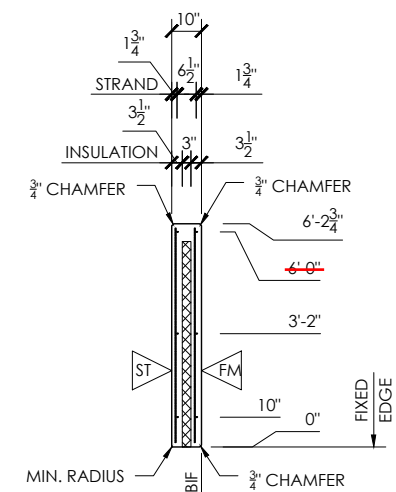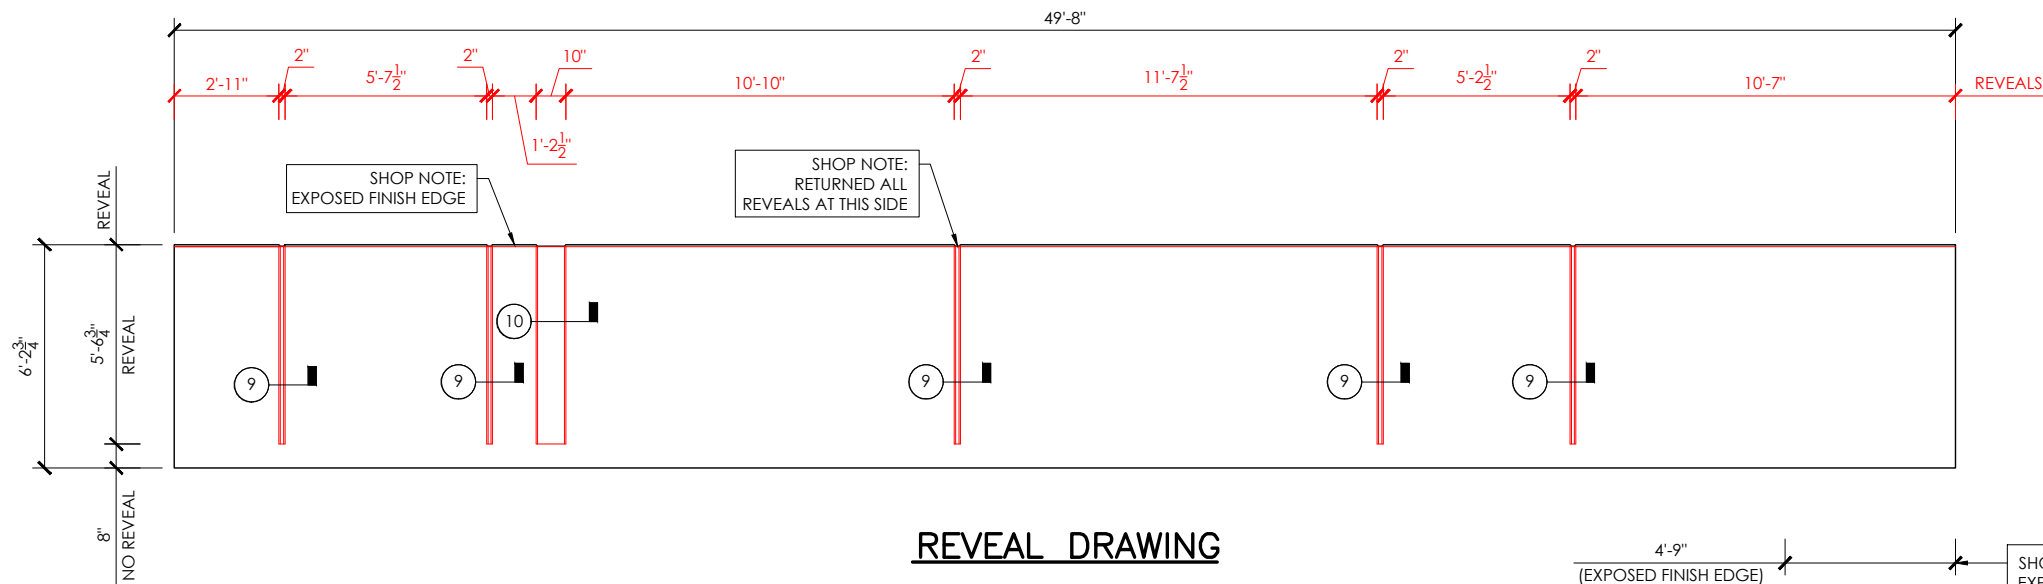

NOTES:

1. ALL REBAR IS TO BE 1" CLR. UNO

2. ALL DIMENSIONS ARE TO CENTERLINE UNO SYMBOLS

S.I.F. = SIDE IN FORM

B.I.F. = BOTTOM IN FORM

T.I.F. = TOP IN FORM

REL.	DESCRIPTION	DATE	BY
1	FOR PRODUCTION	09/28/2021	BM

DRAWN: OSJ	CHECKED: BM	ENGR: LMB	PLOTTED: 09/24/2021
------------	-------------	-----------	---------------------

NORTHEAST PRECAST

92 REESE ROAD
MILLVILLE, NJ 08332
OFFICE: 866-699-2557 FAX: 856-765-9087
www.northeastprecast.com

PROJECT: HRP HUDSON BUILDING 1

JOB NO. 20-NE0881

PIECE MARK: W001

SHEET NO. 3 of 3