


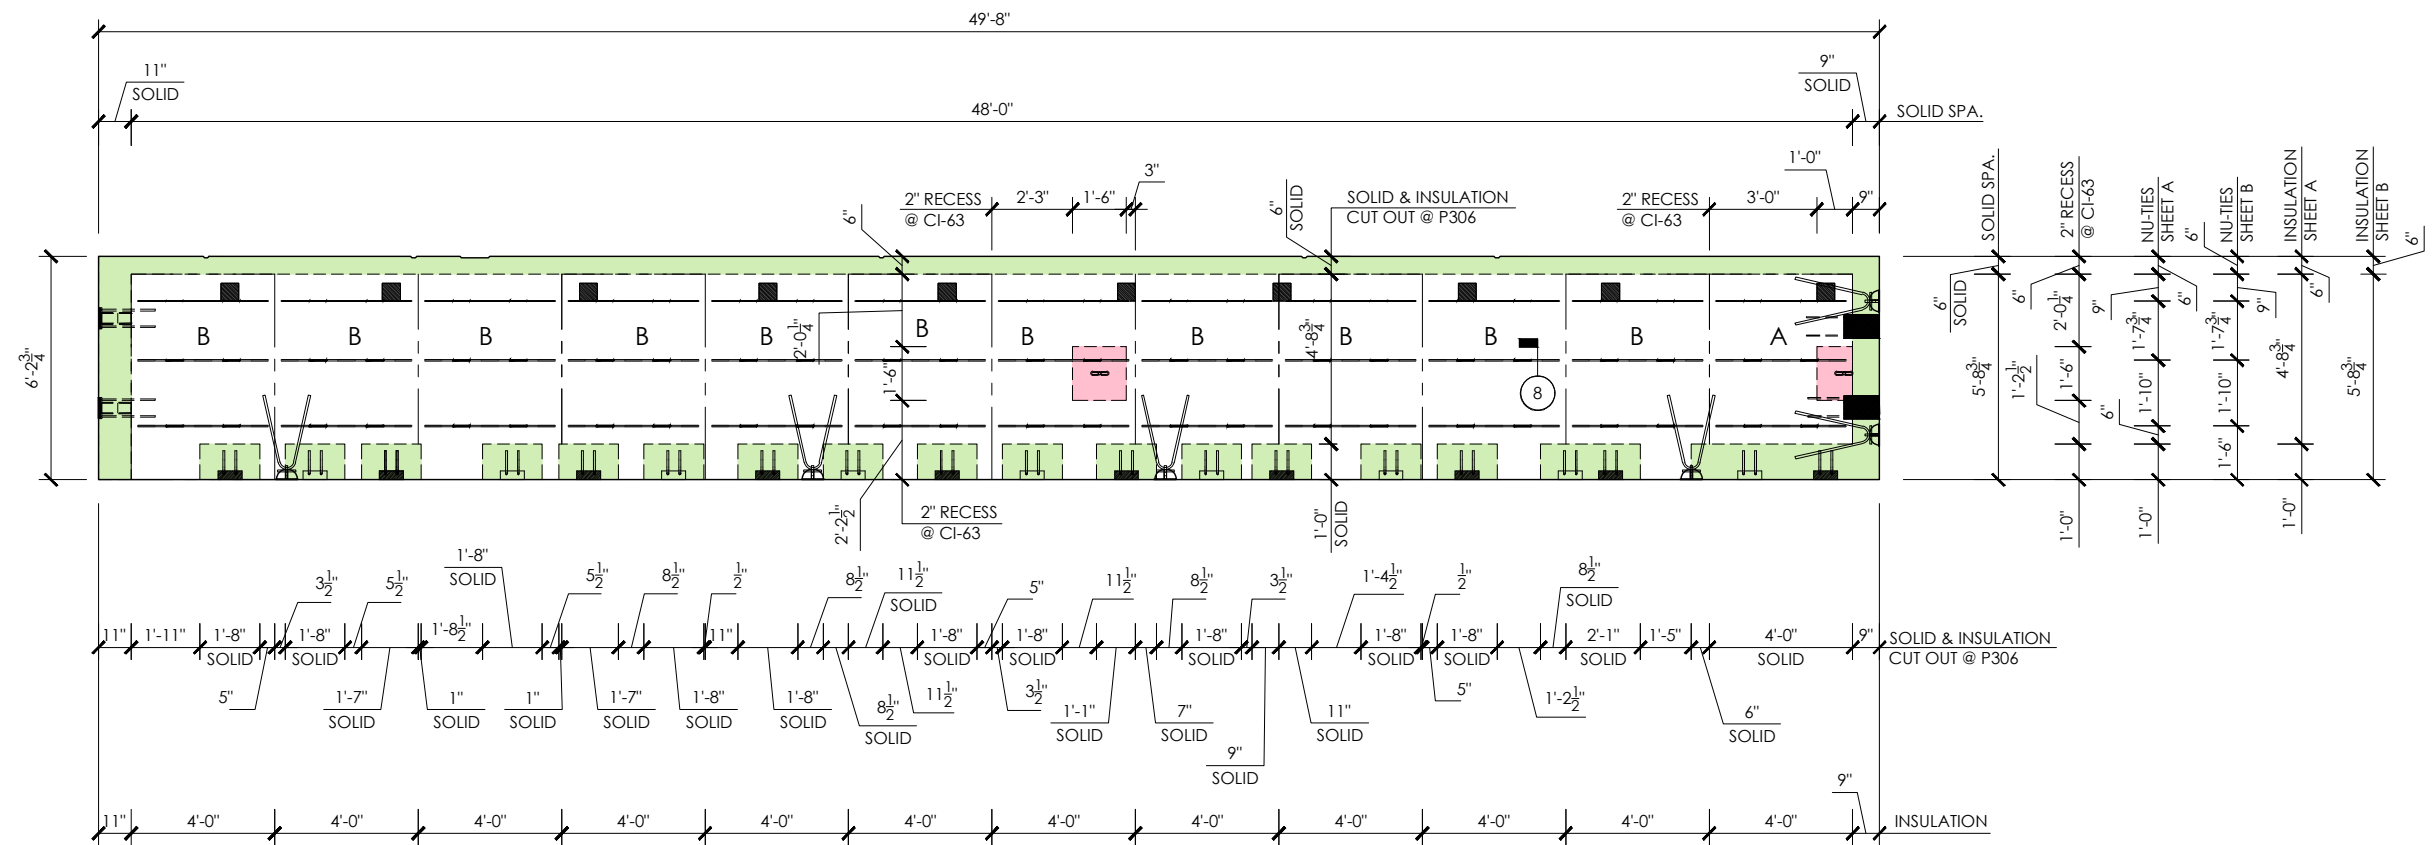

FOAM DRAWING

PIECES OF 3" XPS:

- A: (1) PIECES @ 4'-0" X 4'-8 ³/₄"
B: (11) PIECES @ 4'-0" X 5'-8 ³/₄"



- NOTES:
1. ALL REBAR IS TO BE 1" CLR. UNO
2. ALL DIMENSIONS ARE TO CENTERLINE UNO SYMBOLS
S.I.F. = SIDE IN FORM
B.I.F. = BOTTOM IN FORM
T.I.F. = TOP IN FORM

REL.	DESCRIPTION	DATE	BY
1	FOR PRODUCTION	09/28/2021	BM

DRAWN: OSJ	CHECKED: BM	ENGR: LMB	PLOTTED: 09/24/2021
------------	-------------	-----------	---------------------

NORTHEAST PRECAST
92 REESE ROAD
MILLVILLE, NJ 08332
OFFICE: 866-699-2557 FAX: 856-765-9087
www.northeastprecast.com

PROJECT: HRP HUDSON BUILDING 1	
PIECE MARK: 20-NE0881	SHEET NO.: W001
2 of 3	

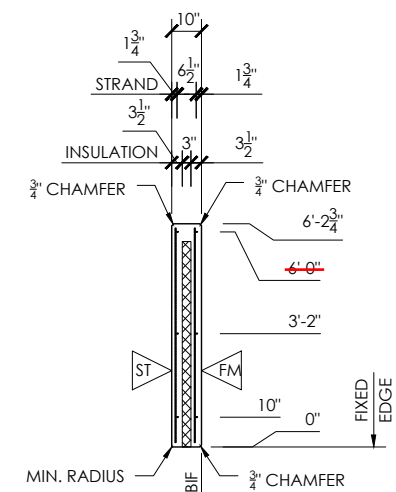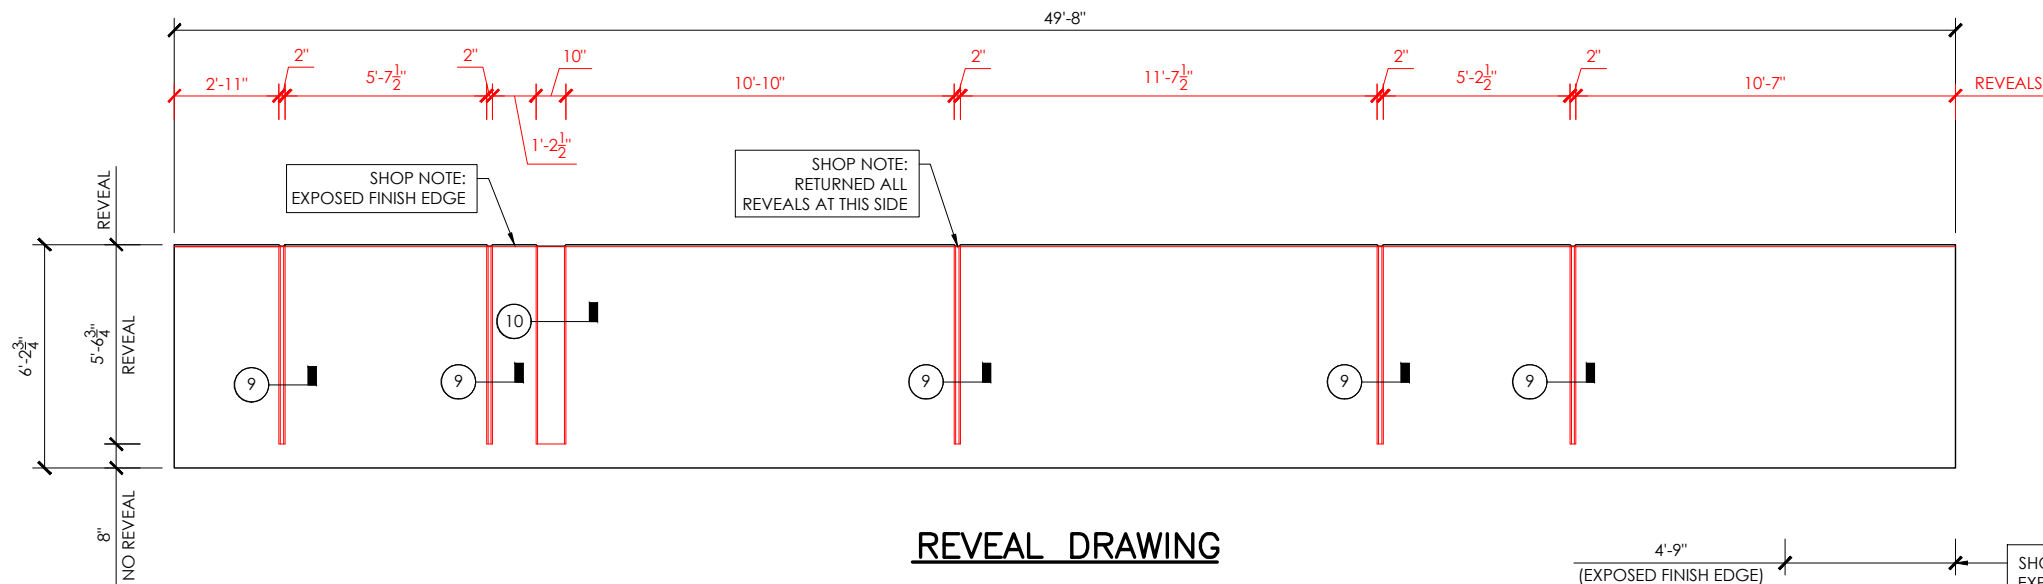

SECTION VIEW

NOTES:
1. ALL REBAR IS TO BE 1" CLR. UNO
2. ALL DIMENSIONS ARE TO CENTERLINE UNO SYMBOLS
S.I.F. = SIDE IN FORM
B.I.F. = BOTTOM IN FORM
T.I.F. = TOP IN FORM

REL.	DESCRIPTION	DATE	BY
1	FOR PRODUCTION	09/28/2021	BM

DRAWN: OSJ	CHECKED: BM	ENGR: LMB	PLOTTED: 09/24/2021
------------	-------------	-----------	---------------------

NORTHEAST PRECAST
92 REESE ROAD
MILLVILLE, NJ 08332
OFFICE: 866-699-2557 FAX: 856-765-9087
www.northeastprecast.com

PROJECT: HRP HUDSON BUILDING 1	
PIECE MARK: 20-NE0881	SHEET NO: W001 3 of 3