



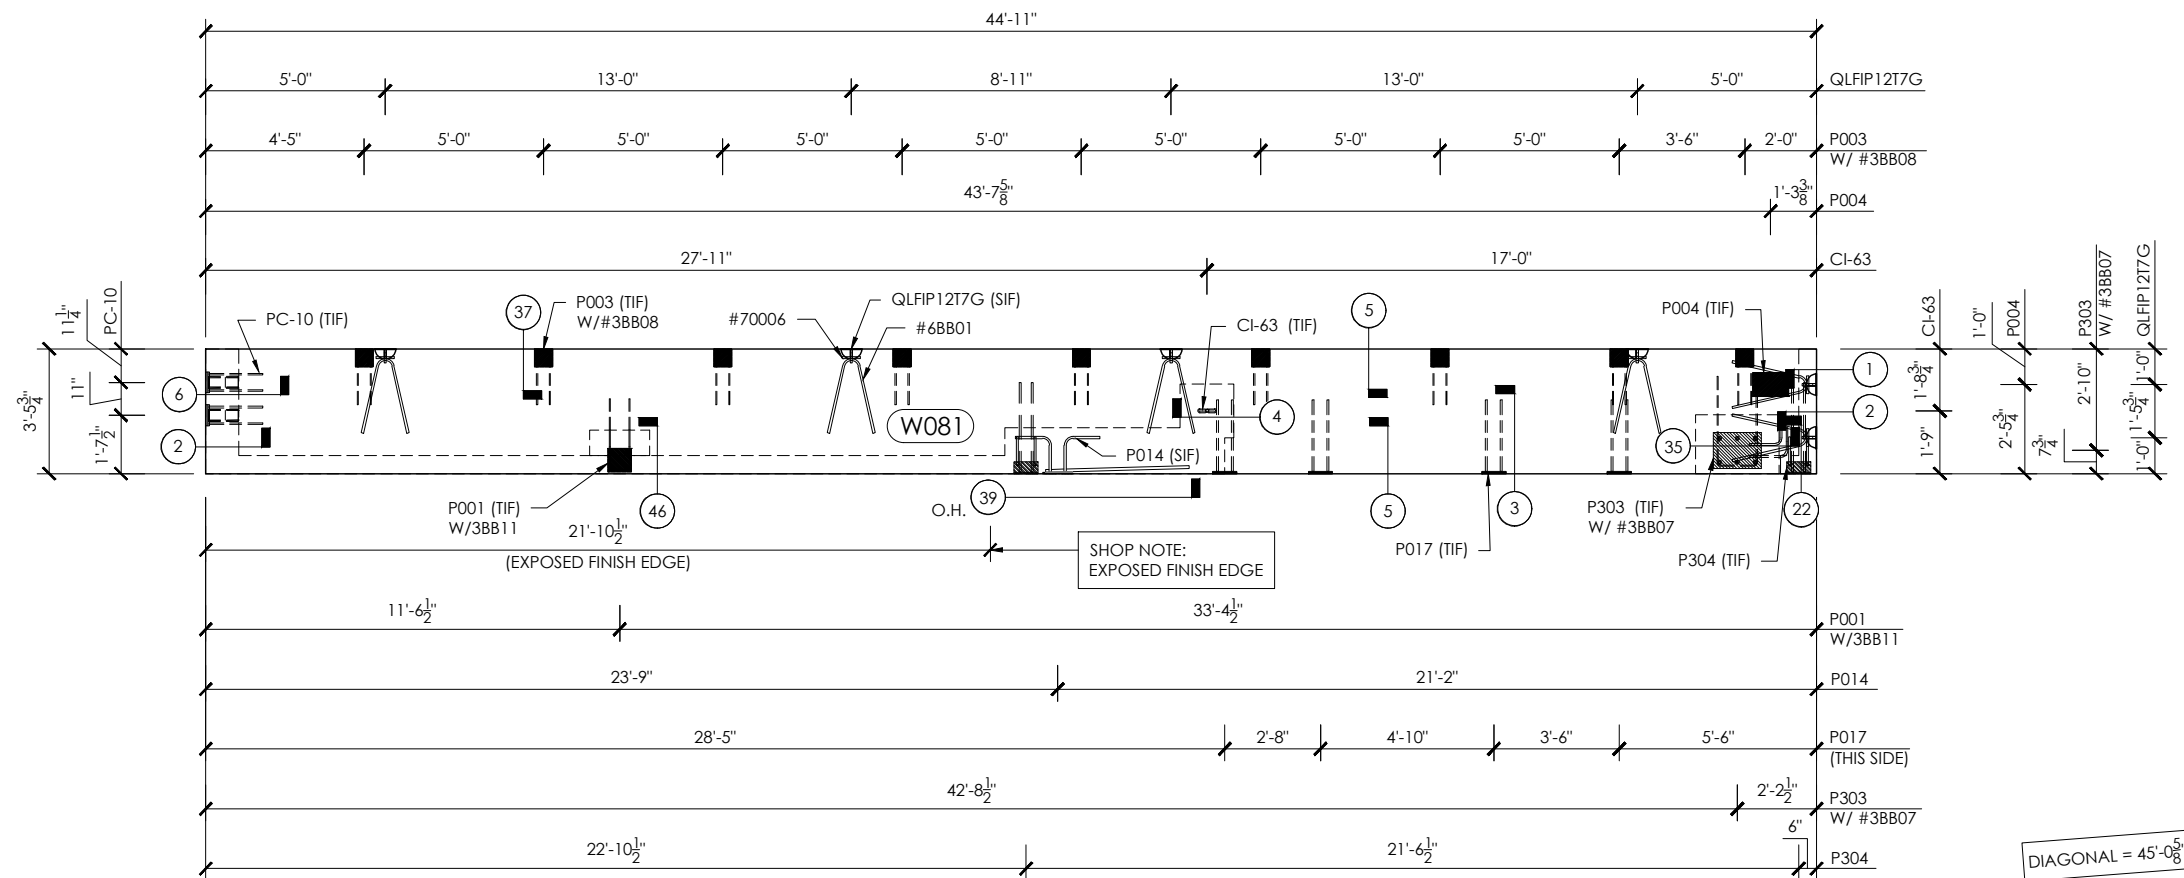

SECTION VIEW

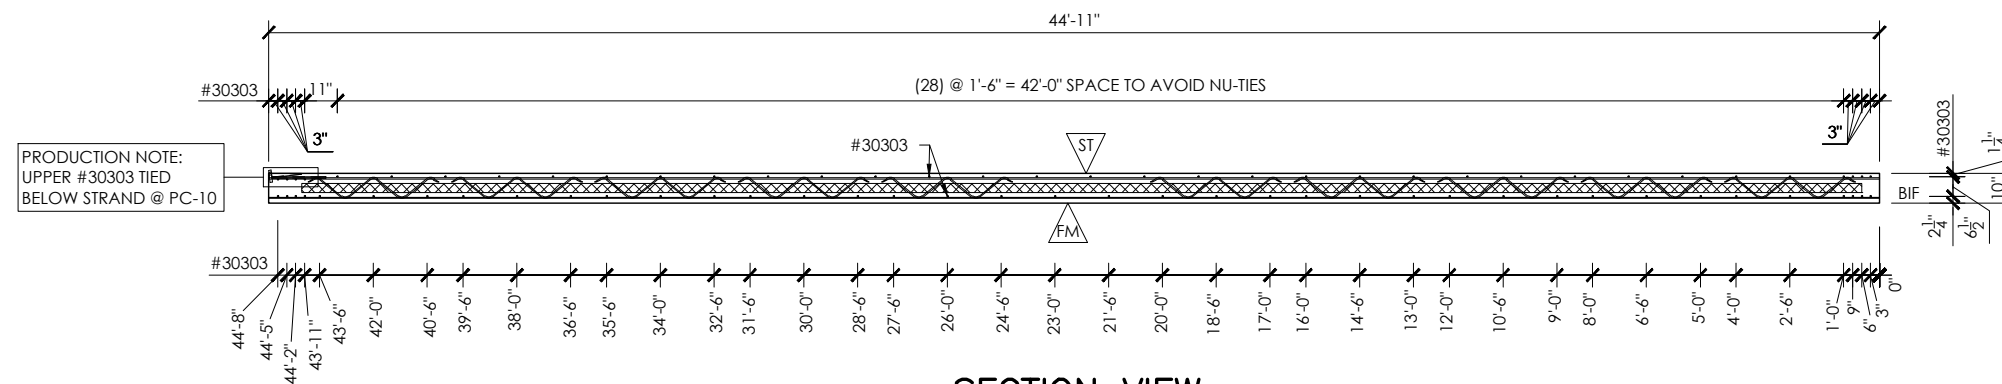

CI-63	3/4" DIA. x 3 1/2" CI-6334312P COIL INSERT	1	EA
NU-TIE	7" NU-TIE	30	EA
PC-10	PL 3/4" x 4" x 0'-7" w/ (2) #4 X 1'-6" BAR & STEEL CHANNEL	2	EA
P001	PL 3/8" x 8" x 0'-8" w/ (4) 5/8" DIA. x 41/8" HCA	1	EA
P003	PL 3/8" x 6" x 0'-6" w/ (4) 1/2" DIA. x 2 5/8" HCA	9	EA
P004	PL 3/8" x 8" x 1'-0" w/ (6) 1/2" DIA. x 2 5/8" HCA	1	EA
P014	PL 3/8" x 8" x 0'-10" w/ (4) #6 x 2'-0 BENT BAR & (1) #8 x 4'-0" TAIL BAR	1	EA
P017	PL 3/8" x 3" x 0'-8" w/ (2) #5 x 2'-0"	4	EA
P303	PL 3/8" x 12" x 1'-4" w/ (6) 5/8" DIA. x 41/8" HCA & (2) #5 x 1'-7" BENT BARS	1	EA
MARK	DESCRIPTION	QTY.	UOM

P304	L 4' x 3' x 3/8" x 0'-8" w/ (2) #5 x 2'-6" & (2) #5 BENT BARS	2	EA
QLFIP127IG	12T SAND PANEL ANCHOR	6	EA
#30303	#3 REBAR X 3'-3" LONG	75	EA
#3BB07	#3 BENT BAR X 5'-11 1/2" LONG	1	EA
#3BB08	#3 BENT BAR X 3'-3" LONG	9	EA
#3BB11	#3 BENT BAR X 4'-5" LONG	1	EA
#6BB01	#6 BENT BAR X 4'-6" LONG	12	EA
#70006	#7 REBAR X 0'-6" LONG	12	EA
MARK		QTY.	UOM

1/2 STRAND	1/2 DIAMETER STRAND X 44'-11" LONG	30.9 KIPS	6	EA
MARK	DESCRIPTION			

CONCRETE MIX		
MIX	CY	B/F
NEP-SP	1.96	B
NEP-15	1.70	F

f _c (28 DAYS)	6,000 PSI
f _c (SHIPPING)	4,000 PSI
f _c (RELEASE)	3,500 PSI

PIECES REQ'D:
1

WEIGHT:
14900 LB

DESIGN:
IWP.2.00

P.C. FOUND ON
E-DRAWING:
E-3.07

REL.	DESCRIPTION	DATE	BY
1	FOR PRODUCTION	9/28/2021	BM

DRAWN: OSJ	CHECKED: BM	ENGINEER: LMB	PLOTTED: 09/17/2021
---------------	----------------	------------------	------------------------

**NORtheast
PRECAST**

92 REESE ROAD
MILLVILLE, NJ 08332
OFFICE: 866-699-2557 FAX: 856-765-9087
www.northeastprecast.com

PROJECT: HRP HUDSON BUILDING 1		
JOB NO. 20-NE0881	PIECE MARK: W081	SHEET NO. 1 of 3





NOTES:

1. ALL REBAR IS TO BE 1" CLR. UNO
2. ALL DIMENSIONS ARE TO CENTERLINE UNO

SYMBOLS

S.I.F. = SIDE IN FORM
B.I.F. = BOTTOM IN FORM
T.I.F. = TOP IN FORM

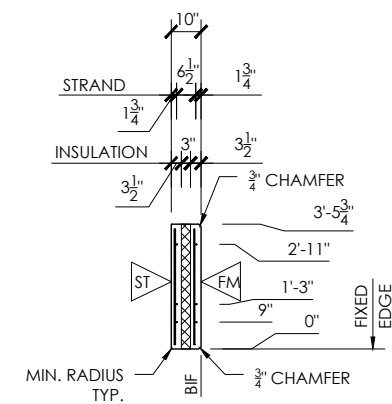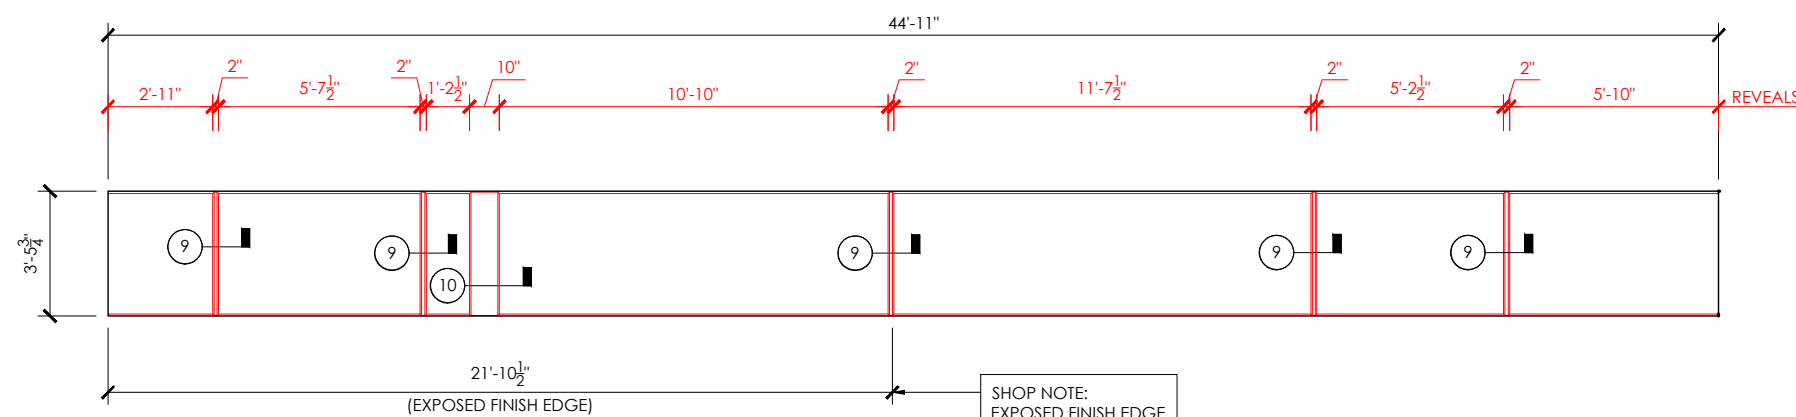

NOTES:
1. ALL REBAR IS TO BE 1" CLR. UNO
2. ALL DIMENSIONS ARE TO CENTERLINE UNO
SYMBOLS
S.I.F. = SIDE IN FORM
B.I.F. = BOTTOM IN FORM
T.I.F. = TOP IN FORM

REL.	DESCRIPTION	DATE	BY
1	FOR PRODUCTION	9/28/2021	BM

DRAWN: OSJ	CHECKED: BM	ENGR: LMB	PLOTTED: 09/17/2021
---------------	----------------	--------------	------------------------