



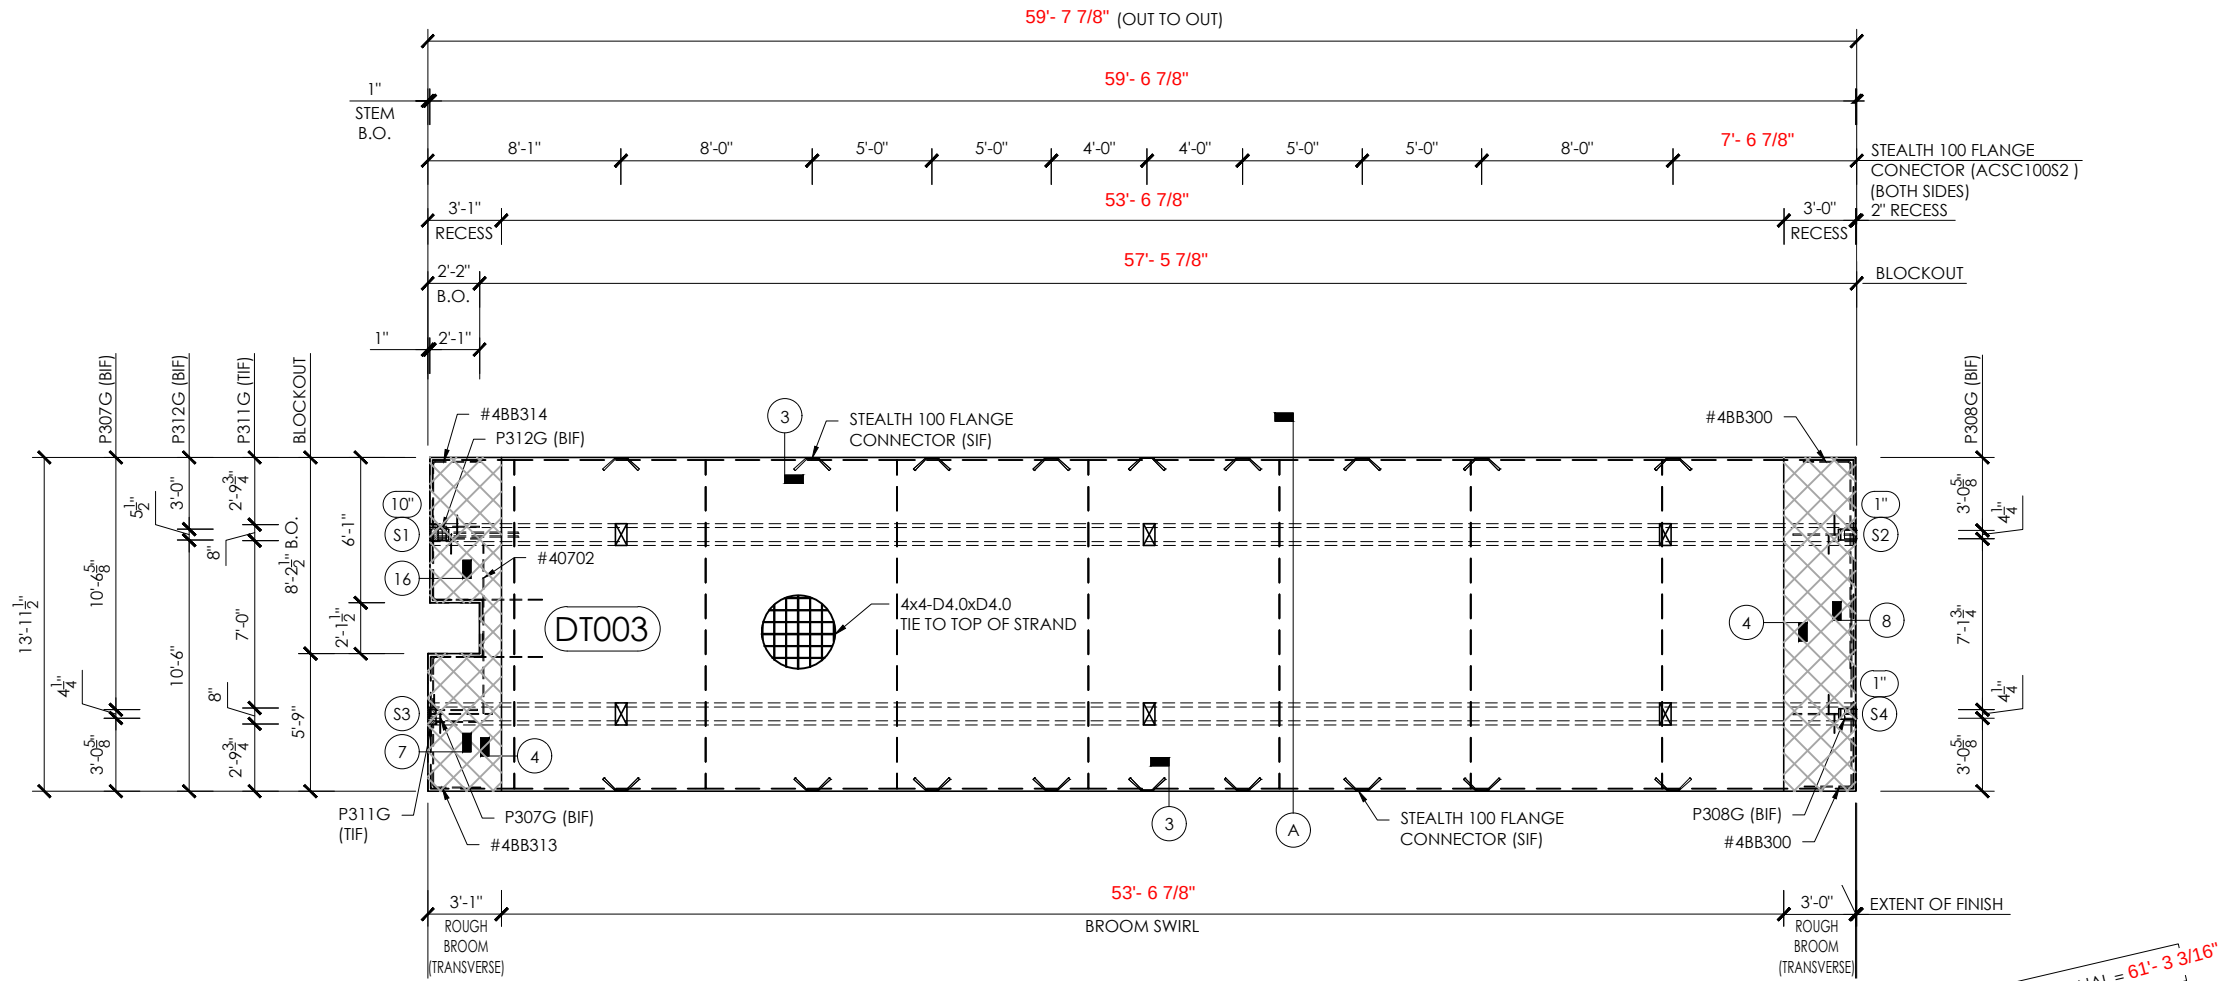


TOP - IN - FORM

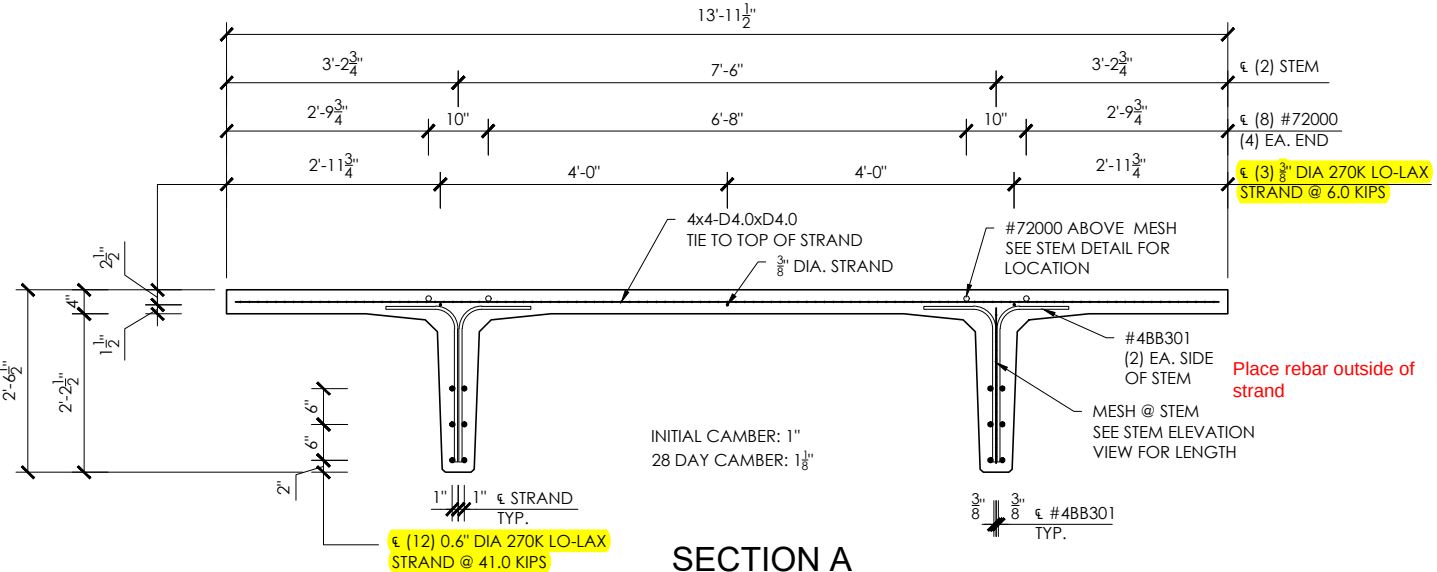

SECTION A

- NOTES:
- 1. ALL REBAR IS TO BE 1 1/2" CLR. CL OF FLANGE UNO.
 - 2. ALL DIMENSIONS ARE TO CENTERLINE UNO
- SYMBOLS
- S.I.F. = SIDE IN FORM
 - B.I.F. = BOTTOM IN FORM
 - T.I.F. = TOP IN FORM
- (S#) = STEM NO. (X") = DAP DIM.
- DECK = BROOM SWIRL
- RECESSES = ROUGH BROOM (TRANSVERSE)
- ALL STEM ENDS = AS CAST
- SIDE OF STEM = STEEL FORM
- BOTTOM OF STEM = STEEL FORM

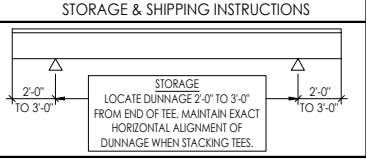

CONTROL NO.:
043,069,095,121,147

MARK	DESCRIPTION	QTY.	UOM
STEALTH 100	FLANGE CONNECTOR(STAINLESS)(ACSC100S2)	18	EA
P307G	PL 3/8" x 4 1/4" x 0'-6" w/ (1) #4 x 2'-0" & (1) #5 x 2'-6" BAR (GALV.)	1	EA
P308G	PL 3/8" x 4 1/4" x 0'-6" w/ (1) #4 x 2'-0" & (1) #5 x 2'-6" BAR (GALV.)	2	EA
P311G	PL 1/4" x 4" x 0'-8" w/ (2) #4 x 2'-0" BAR (GALV.)	2	EA
P312G	PL 3/8" x 5 1/2" x 0'-6" w/ (2) #4 x 1'-3" & (2) #5 x 3'-6" BAR (GALV.)	1	EA
QLSA912T23	ALP QLSA912T23 SPIRAL ANCHOR	4	EA
STEM BO	STEM BLOCKOUT	6	EA

MARK	DESCRIPTION	QTY.	UOM
#4BB301A		8	
#40702		1	EA
#4BB300		2	EA
#4BB301		24	EA
#4BB302		1	EA
#4BB313		1	EA
#4BB314		1	EA
#72000		8	EA
#6BB300		1	EA

MARK	DESCRIPTION		
#6BB301		1	EA
F MESH-C	4X4-D4.0xD4.0 13'-9" WIDE X 8'-0" LONG	7	EA
F MESH-D	4X4-D4.0xD4.0 13'-9" WIDE X 3'-5" LONG	2	EA
S MESH-A	4X4-D2.9xD2.9 2'-0" WIDE X 15'-0" LONG	4	EA
3/8 STRAND	3/8 DIAMETER LO-LAX STRAND 6.0 KIPS	3	EA
0.6 STRAND	0.6 DIAMETER LO-LAX STRAND 41 KIPS	12	EA

MIX	CY
700A-CNI	15.38
Fc (28 DAYS)	6,000 PSI
Fc (SHIPPING)	6,000 PSI
Fci (RELEASE)	4,000 PSI

PIECES REQ'D:	5
WEIGHT:	62,500
DESIGN:	DT2.00

REL.	DESCRIPTION	DATE	BY
1	FOR PRODUCTION	07/22/2025	JMW

NORTHEAST PRECAST



4081 S. Lincoln Ave., Vineland, NJ 08361
OFFICE: 856-699-2557 FAX: 856-765-9087
www.northeastprecast.com

PROJECT: WOODBRIDGE METROPARK GARAGE

JOB NO. 24-NE1096

PIECE MARK: DT003

SHEET NO. 1 of 2

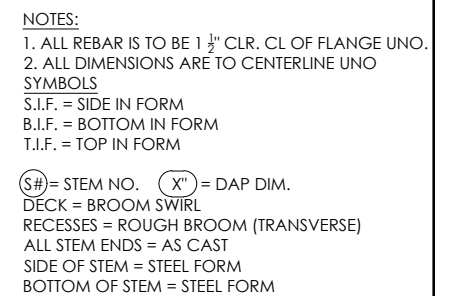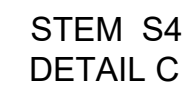

REL.	DESCRIPTION	DATE	BY
1	FOR PRODUCTION	07/22/2025	JMW

DRAWN: DAI
CHECKED: CO
ENG'D: BEM
PLOTTED: 06/25/2025

NORTHEAST PRECAST

4081 S. Lincoln Ave., Vineland, NJ 08361
OFFICE: 866-699-2557 FAX: 856-765-9087
www.northeastprecast.com

PROJECT: WOODBRIDGE METROPARK GARAGE

JOB NO.	PIECE MARK	SHEET NO.
24-NE1096	DT003	2 of 2