



REL.	DESCRIPTION	DATE	BY
1	FOR PRODUCTION	06/06/25	PS


DRAWN: AK	CHECKED: SS	ENGR: PP	PLOTTED: 6/6/2025 5:05 PM
-----------	-------------	----------	---------------------------

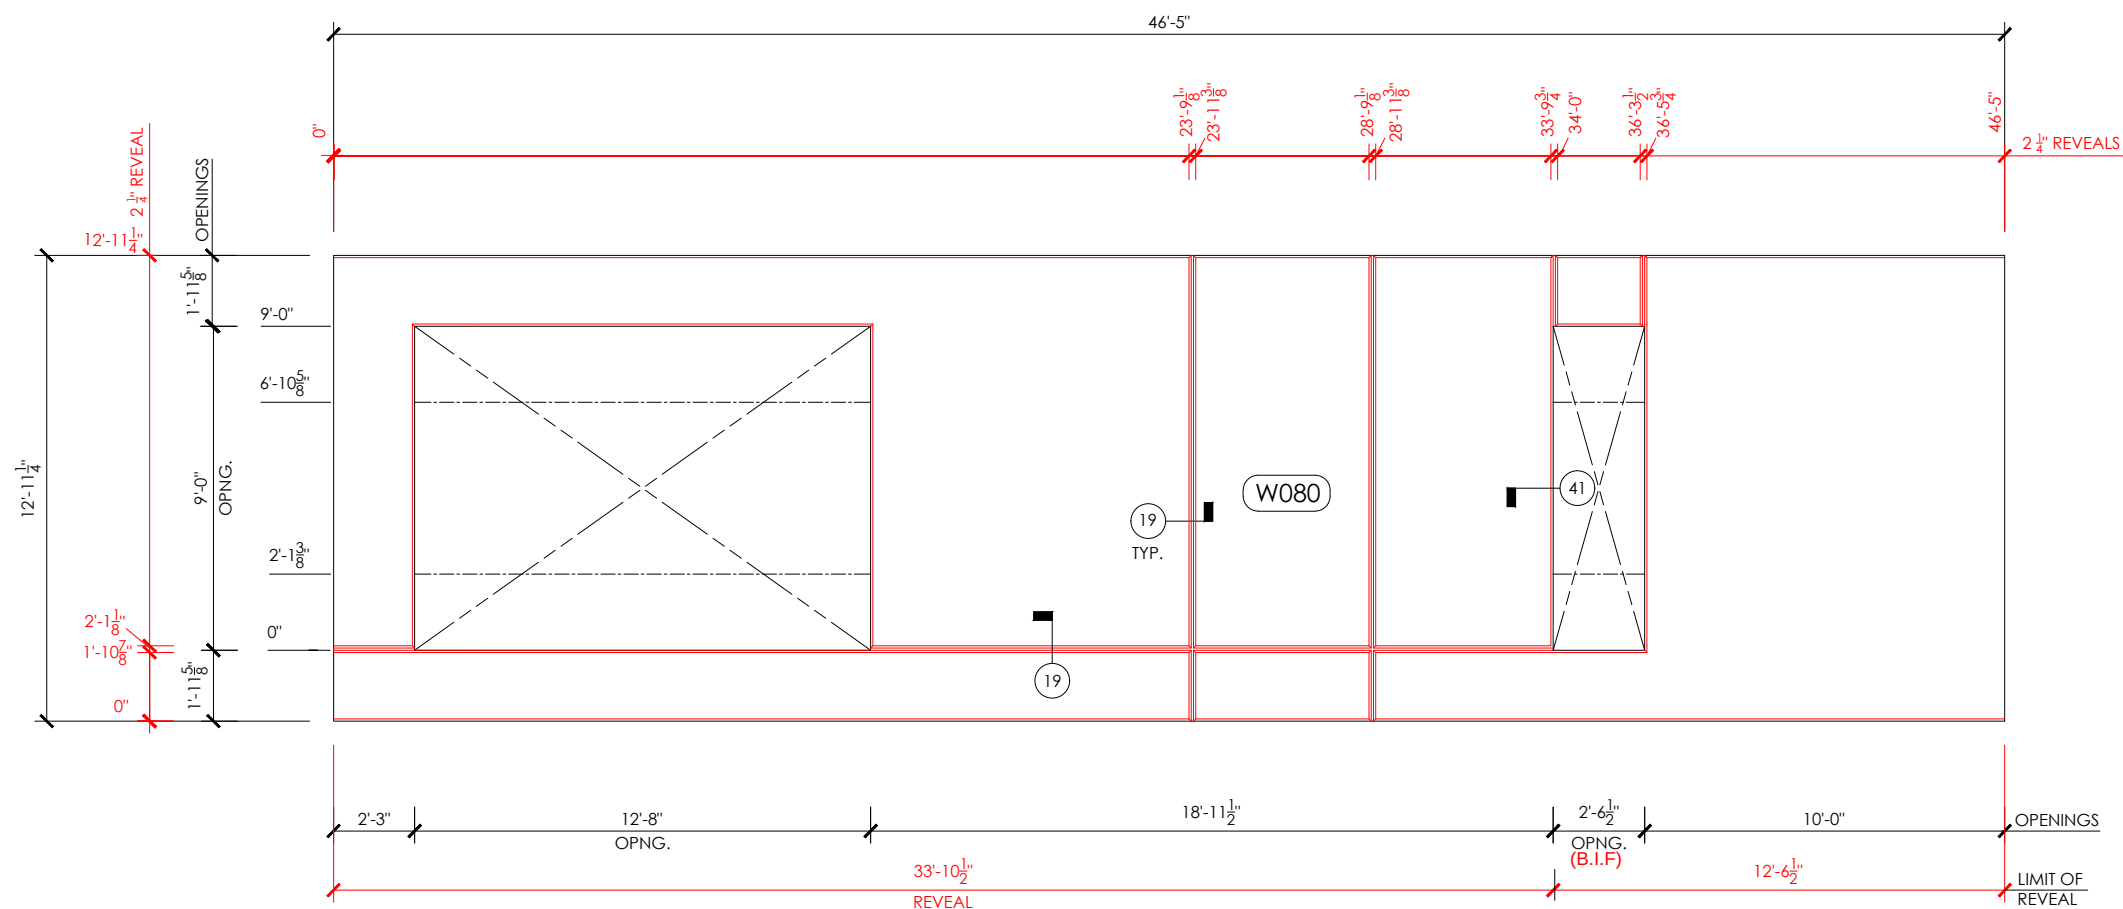

REVEAL DRAWING

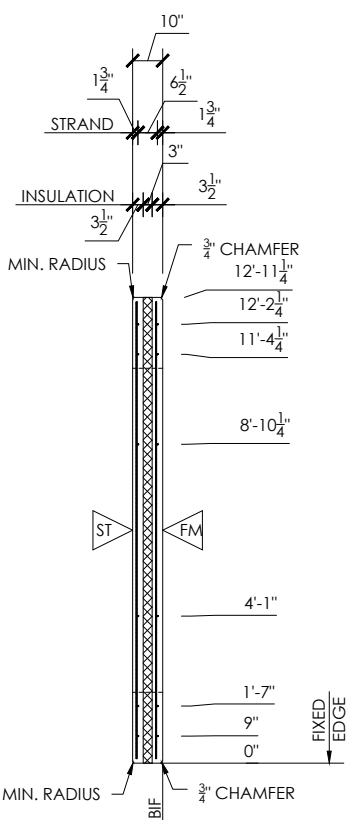

SECTION VIEW

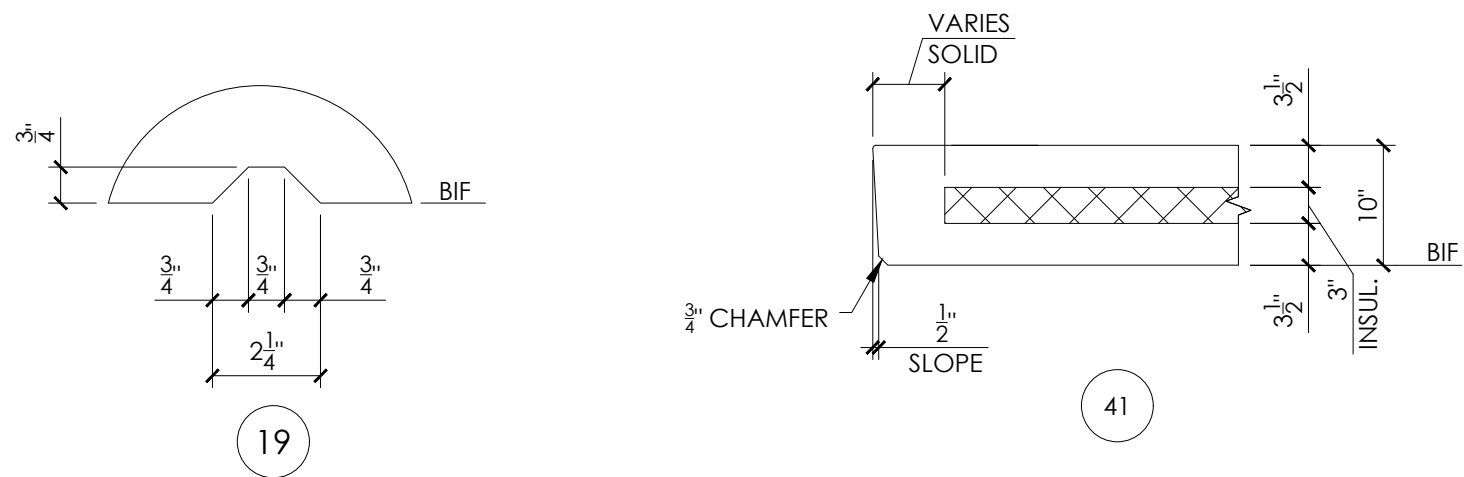

NOTES:
1. ALL REBAR IS TO BE 1" CLR. UNO
2. ALL DIMENSIONS ARE TO CENTERLINE UNO
3. SPLIT STRONGBACK C.Y. 50/50 FACE MIX / BACK MIX
4. PLACE REBAR 2" FROM EDGE OF ROUGH OPENINGS

SYMBOLS
S.I.F. = SIDE IN FORM
B.I.F. = BOTTOM IN FORM
T.I.F. = TOP IN FORM
E.O.P. = EDGE OF PLATE

ST = STEEL TROWEL
FM = FORM FINISH

REL.	DESCRIPTION	DATE	BY
1	FOR PRODUCTION	06/06/25	PS

DRAWN: AK	CHECKED: SS	ENGR: PP	PLOTTED: 6/6/2025 5:05 PM
-----------	-------------	----------	---------------------------

PRECAST ENGINEER:

BUILDING THEORY

18 KING ST. EAST SUITE 1400,
TORONTO ON M5C 1C4, CANADA
WWW.BUILDINGTHEORY.COM
TEL: +1-647-906-7812

NORTHEAST PRECAST

4081 S. LINCOLN AVE.
VINELAND, NJ 08361
OFFICE: 866-699-2557 FAX: 856-765-9087
www.northeastprecast.com

PROJECT: LINK - HYATT

JOB NO. 25-NE1204	PIECE MARK W080	SHEET NO. 3 of 3
-------------------	-----------------	------------------