
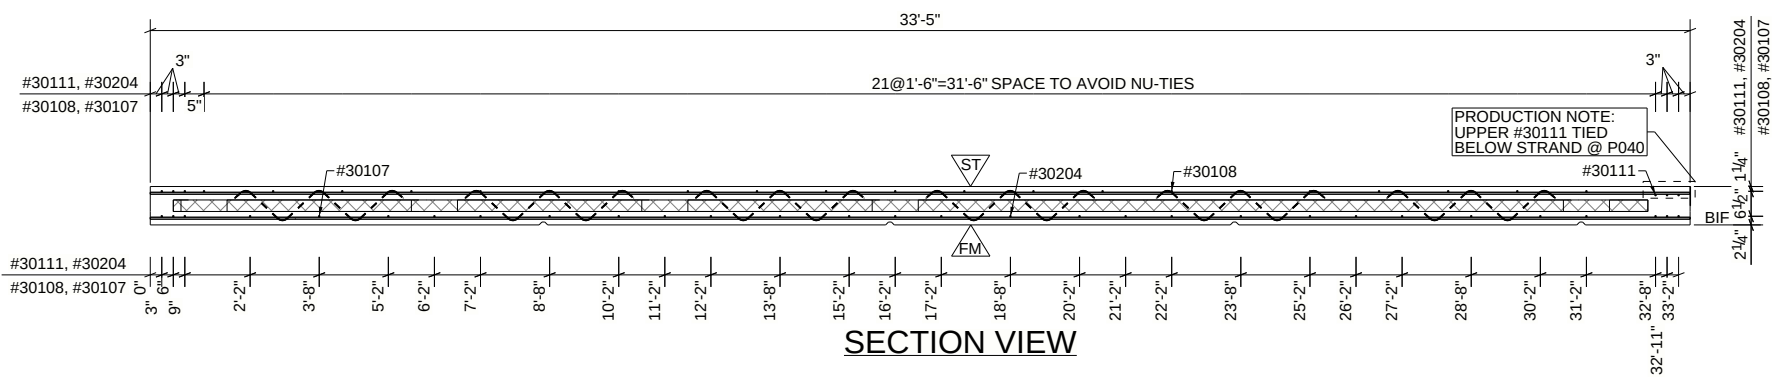
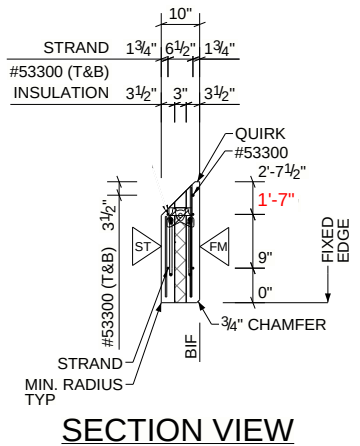


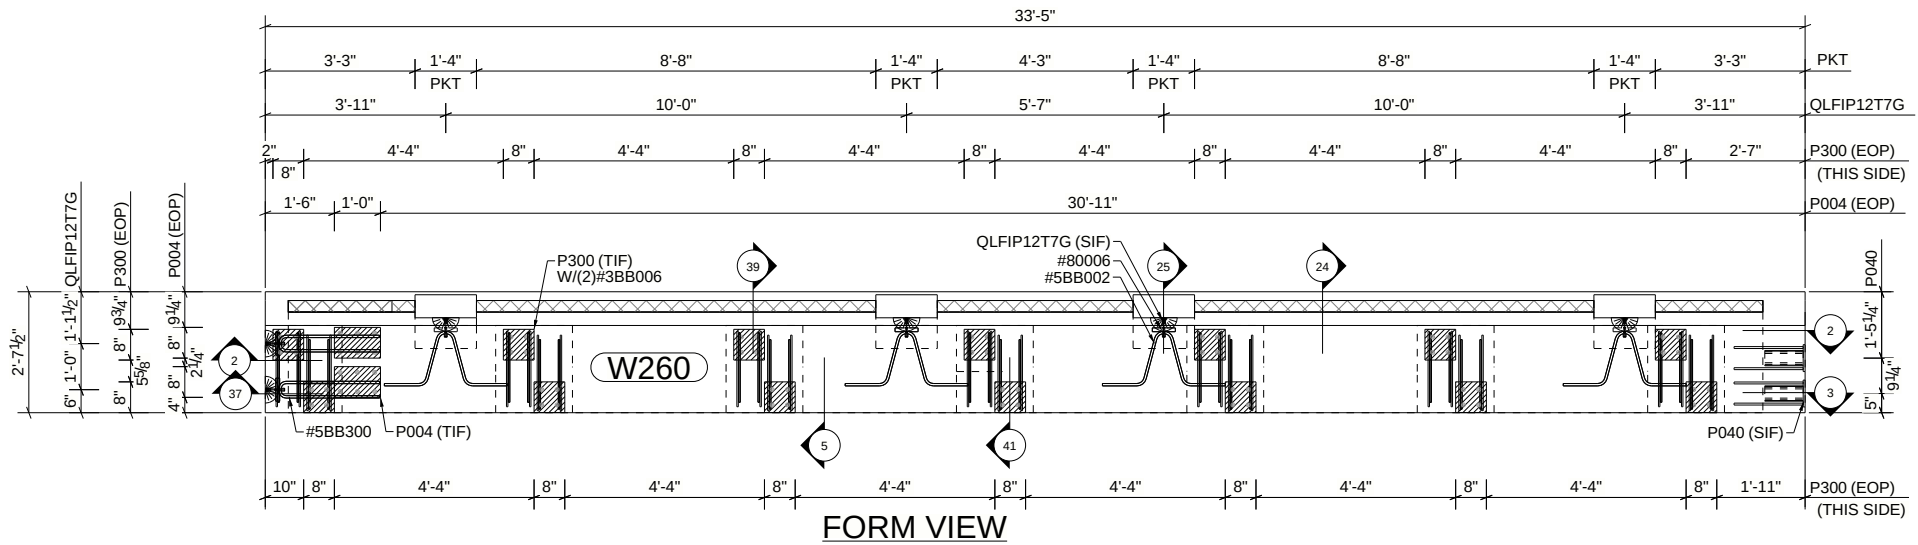

DIAGONAL = 33'-6 1/4"

PRODUCTION NOTE:
BOTTOM WYTHE MUST BE RAKED AT
ALL SOLID ZONE LOCATIONS

- NOTES:
- ALL REBAR IS TO BE 1 1/2" CLR. UNO
 - ALL DIMENSIONS ARE TO CENTERLINE UNO
 - ALL TRIM BARS TO BE 2" CLEAR FROM EDGE OF OPENING UNO

SYMBOLS
SIF = SIDE IN FORM
BIF = BOTTOM IN FORM
TIF = TOP IN FORM
EOP = EDGE OF PLATE

ST = STEEL TROWEL
FM = FORM FINISH
SPX = STRAND PATTERN

NU-TIE	7" NU-TIE	12	EA
P004	PL3/8X8X1'-0" W/ (6) 1/2" DIA X 2 5/8" HCA	2	EA
P040	PL3/4X4X0'-7" W/ (2) #4 X 1'-6"	2	EA
P300	PL3/8X8X8 W/ (4) 1/2" DIA X 6" LONG HCA & (2) #4 BARS	14	EA
QLFIP12T7G	12T SAND PANEL ANCHOR	6	EA
#30107	#3 REBAR X 1'-7" LONG	2	EA
#30108	#3 REBAR X 1'-8" LONG	24	EA
#30111	#3 REBAR X 1'-11" LONG	3	EA
#30204	#3 REBAR X 2'-4" LONG	28	EA
MARK	DESCRIPTION	QTY.	UOM

#3BB006	#3 BENT REBAR, SEE TABLE	28	EA
#53300	#5 REBAR X 33'-0" LONG	1	EA
#5BB002	#5 BENT REBAR, SEE TABLE	8	EA
#5BB300	#5 BENT REBAR, SEE TABLE	4	EA
#80006	#8 REBAR X 0'-6" LONG	12	EA
1/2 STRAND	1/2 DIAMETER STRAND 28.90 Kips	4	EA
MARK	DESCRIPTION	QTY.	UOM

MARK	DESCRIPTION	QTY.	UOM
------	-------------	------	-----

CONCRETE MIX		
MIX	CY	B/F
725N	1.16	B
700A	0.73	F
F _c (28 DAYS)		
6000 PSI		
F _c (SHIPPING)		
4000 PSI		
F _c (RELEASE)		
3500 PSI		

PIECES REQ'D:	1
WEIGHT:	7807 LBS
DESIGN:	SP1
CONTROL NO.:	260

REV.	DESCRIPTION	DATE	BY
0	ISSUED FOR PRODUCTION	07/01/2025	JOM
1			
2			
3			
4			
5			
DRAWN:	CHECKED:	ENGR:	PLOTTED:
JOM	AMC	AJC	08/21/2025


NORTHEAST PRECAST
4081 S. LINCOLN AVE
VINELAND, NJ 08361
OFFICE: 866-699-2557 FAX: 856-765-9087
www.northeastprecast.com

PROJECT:
NEWBURGH SOUTH LOGISTICS CENTER



JOB NO.:
25-NE1212

PIECE MARK:
W260

SHEET NO.:
1 OF 3

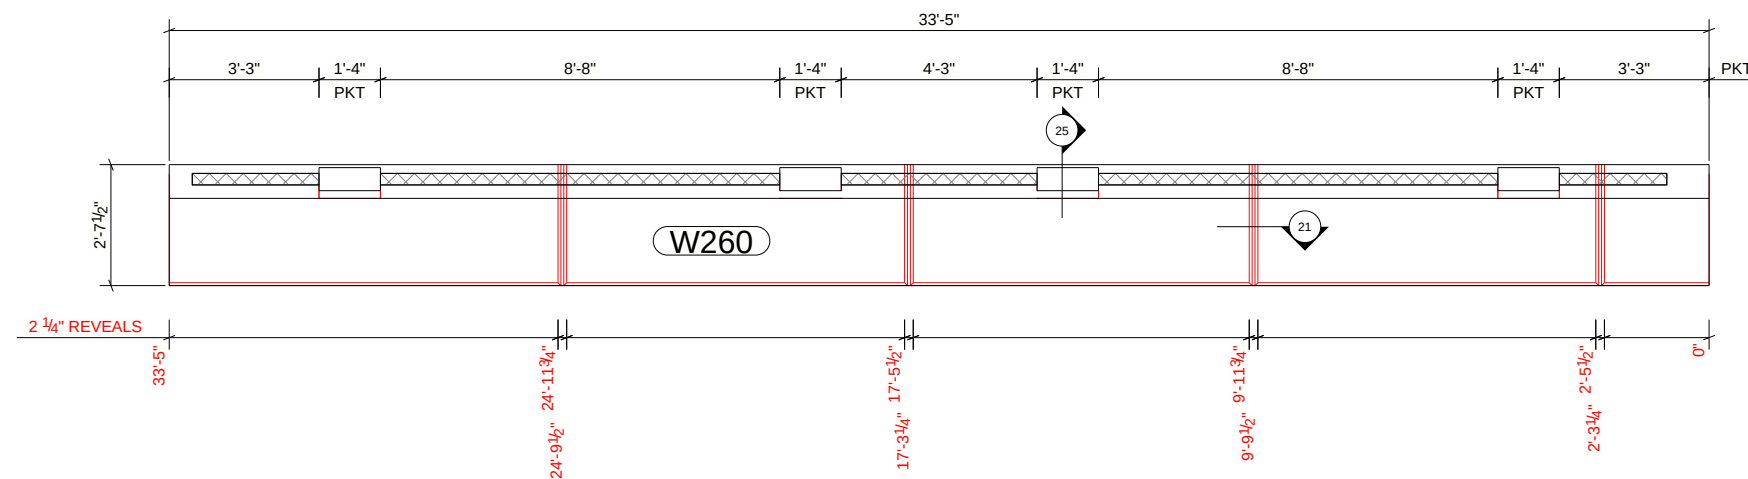

REVEAL DRAWING

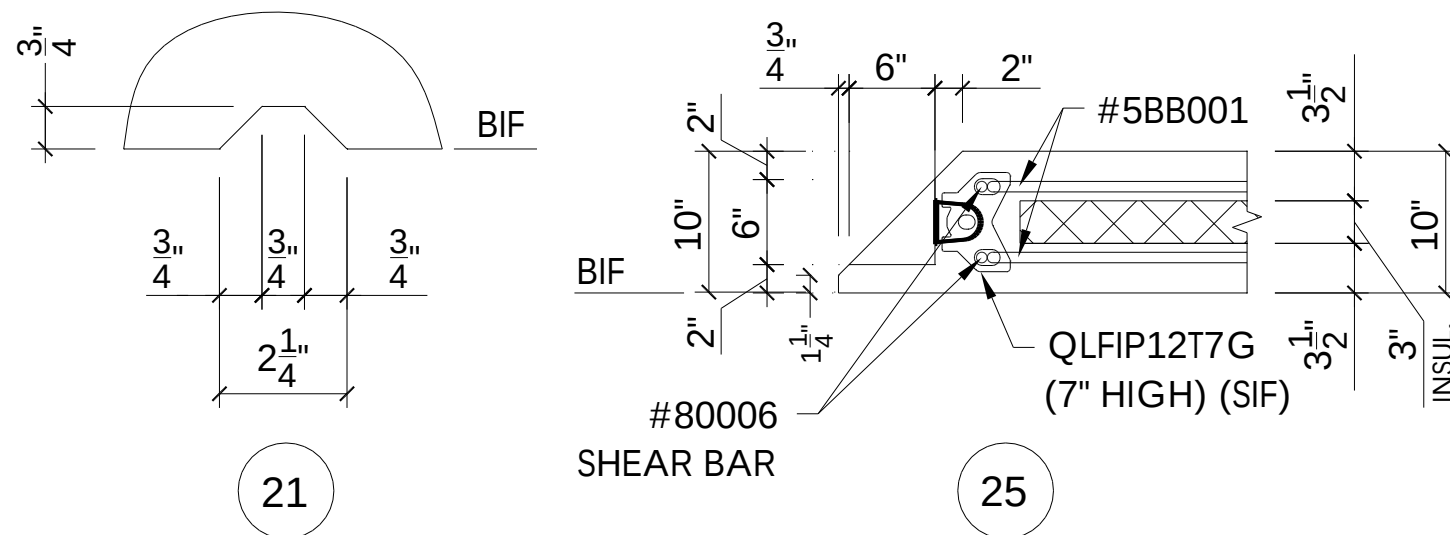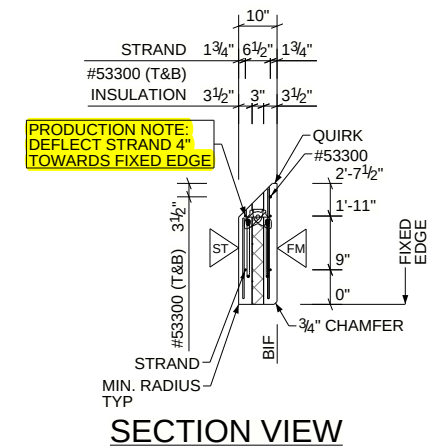

- NOTES:
1. ALL REBAR IS TO BE 1 1/2" CLR. UNO
 2. ALL DIMENSIONS ARE TO CENTERLINE UNO
- SYMBOLS
- SIF = SIDE IN FORM
- BIF = BOTTOM IN FORM
- TIF = TOP IN FORM

REV.	DESCRIPTION	DATE	BY
0	ISSUED FOR PRODUCTION	07/01/2025	JOM
1			
2			
3			
4			
5			

DRAWN: JOM	CHECKED: AMC	ENGR: AJC	PLOTTED: 08/21/2025
---------------	-----------------	--------------	------------------------

PROJECT: NEWBURGH SOUTH LOGISTICS CE***	
JOB NO. 25-NE1212	PIECE MARK W260
SHEET NO. 3 OF 3	

NORTHEAST PRECAST	
4081 S. LINCOLN AVE VINELAND, NJ 08361	
OFFICE: 866-699-2557 FAX: 856-765-9087	
www.northeastprecast.com	